


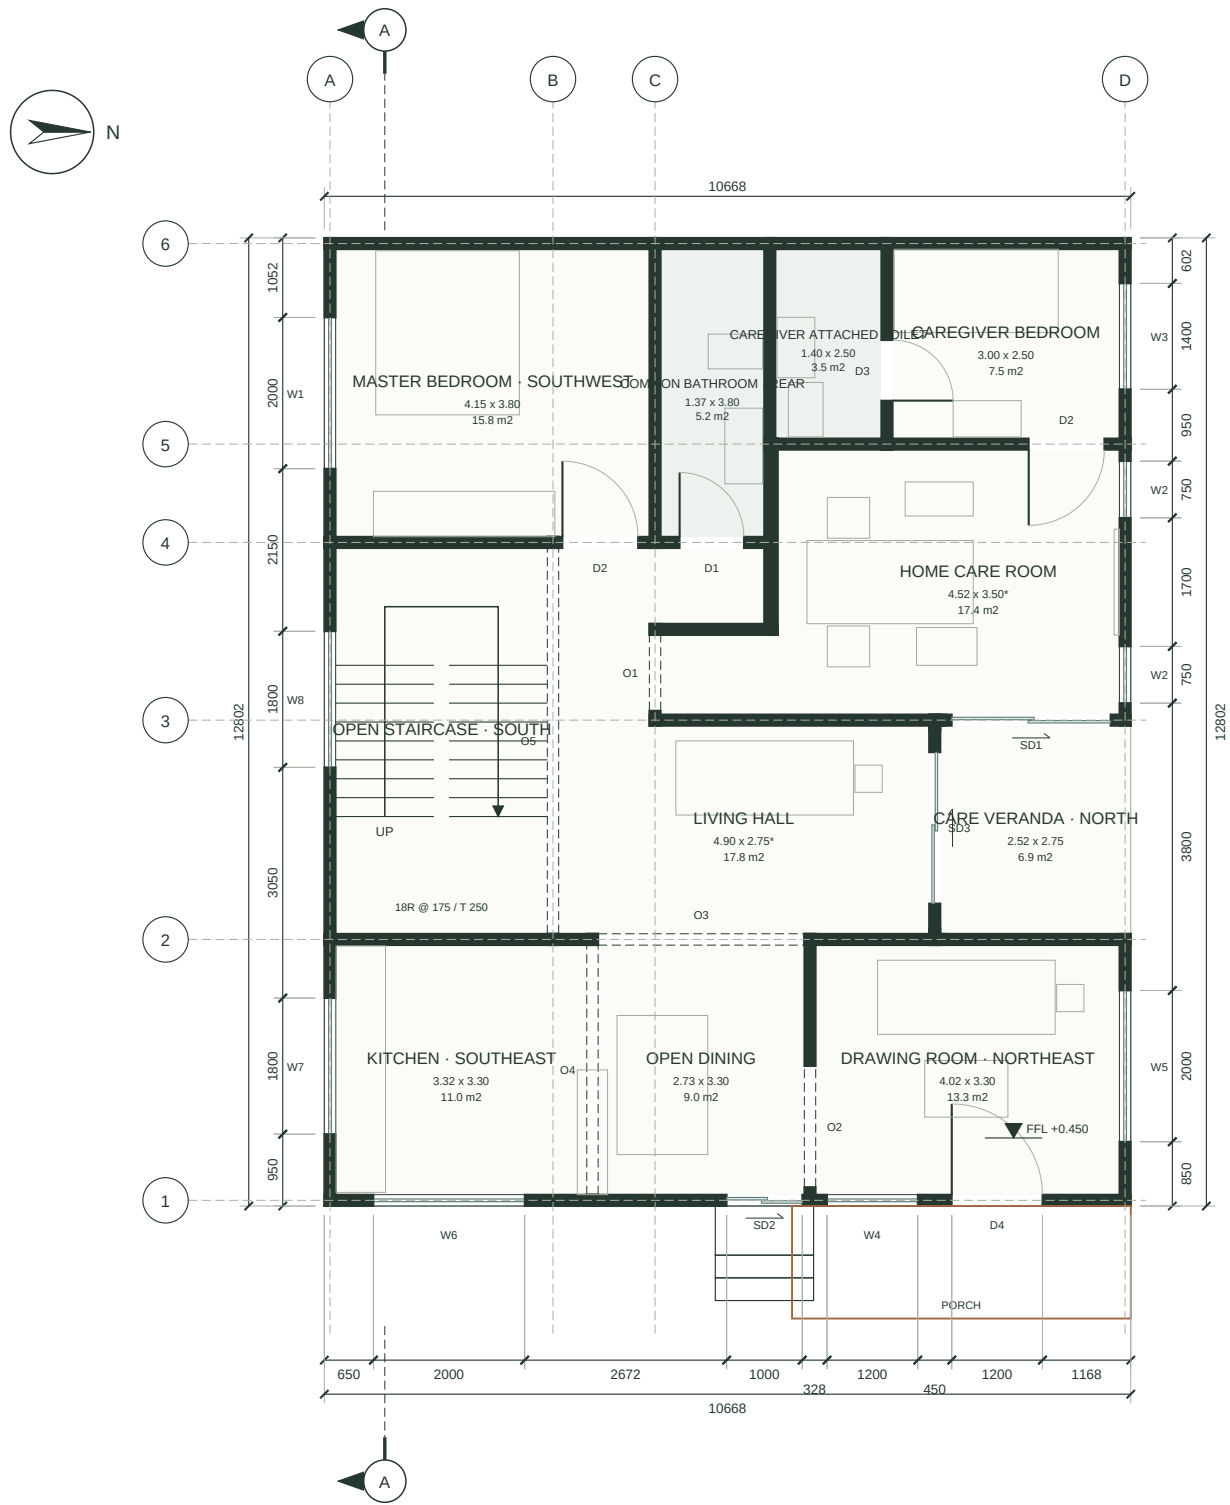

My Desired Home

SPACE	CLEAR SIZE m	AREA m2
Common bathroom · rear	1.37 x 3.80	5.20
Master bedroom · southwest	4.15 x 3.80	15.78
Home care room	4.52 x 3.50*	17.44
Caregiver bedroom	3.00 x 2.50	7.51
Caregiver attached toilet	1.40 x 2.50	3.50
Open dining	2.73 x 3.30	9.00
Drawing room · northeast	4.02 x 3.30	13.26
Kitchen · southeast	3.32 x 3.30	10.96
Living hall	4.90 x 2.75*	17.81
Care veranda · north	2.52 x 2.75	6.92

DRAWING NOTES

All dimensions in millimetres; levels in metres above natural ground level (NGL).

Room sizes are clear sizes between finished wall faces; * marks the principal rectangle of an L-shaped room.

Dimension chains: openings, walls, overall. Tags: D door, SD sliding door, O cased opening, W window, V ventilator (see A-601).


Door leaves are drawn in the room they open into. Windows above the +1.2 m cut are dashed; furniture is schematic at true scale.

Grid bubbles are coordination axes only, not column positions.

No certified IS 962 or local-code compliance is claimed.

SCALE 1:100 AT A3 / CUT +1200 mm

Dimensions govern; do not scale from a screen.

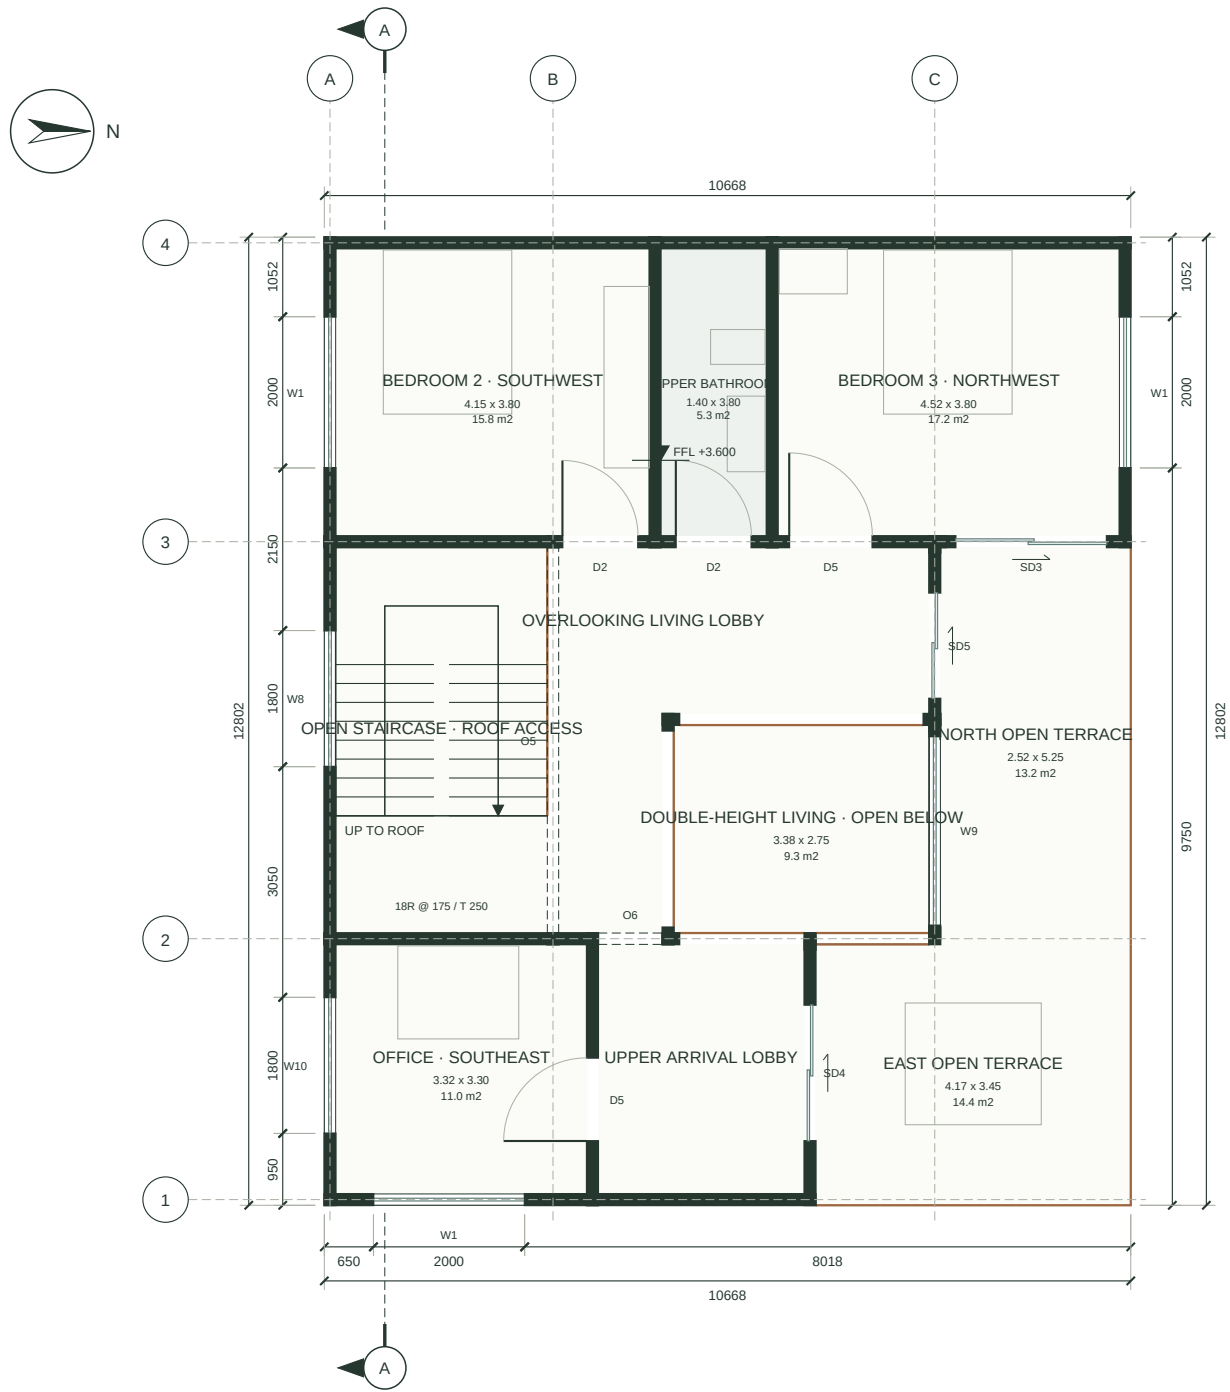

My Desired Home

SPACE	CLEAR SIZE m	AREA m2
Upper bathroom	1.40 x 3.80	5.32
Bedroom 3 · northwest	4.52 x 3.80	17.18
Bedroom 2 · southwest	4.15 x 3.80	15.78
Double-height living · open be	3.38 x 2.75	9.29
Upper arrival lobby	2.73 x 3.30	9.00
Overlooking living lobby	4.90 x 2.20*	14.76
Office · southeast	3.32 x 3.30	10.96
East open terrace	4.17 x 3.45	14.38
North open terrace	2.52 x 5.25	13.22

DRAWING NOTES

All dimensions in millimetres; levels in metres above natural ground level (NGL).

Room sizes are clear sizes between finished wall faces; * marks the principal rectangle of an L-shaped room.

Dimension chains: openings, walls, overall. Tags: D door, SD sliding door, O cased opening, W window, V ventilator (see A-601).

Door leaves are drawn in the room they open into. Windows above the +1.2 m cut are dashed; furniture is schematic at true scale.

Grid bubbles are coordination axes only, not column positions.

No certified IS 962 or local-code compliance is claimed.

SCALE 1:100 AT A3 / CUT +1200 mm

Dimensions govern; do not scale from a screen.



My Desired Home

SPACE	AREA m2
Open roof terrace	92.01

DRAWING NOTES


Roof access level, not an additional occupied storey.

Use the linked stair and its landing door to reach the guarded terrace.

Roof openings and headhouse positions follow the authored stair core.

SCALE 1:100 AT A3 / CUT +1200 mm

Dimensions govern; do not scale from a screen.

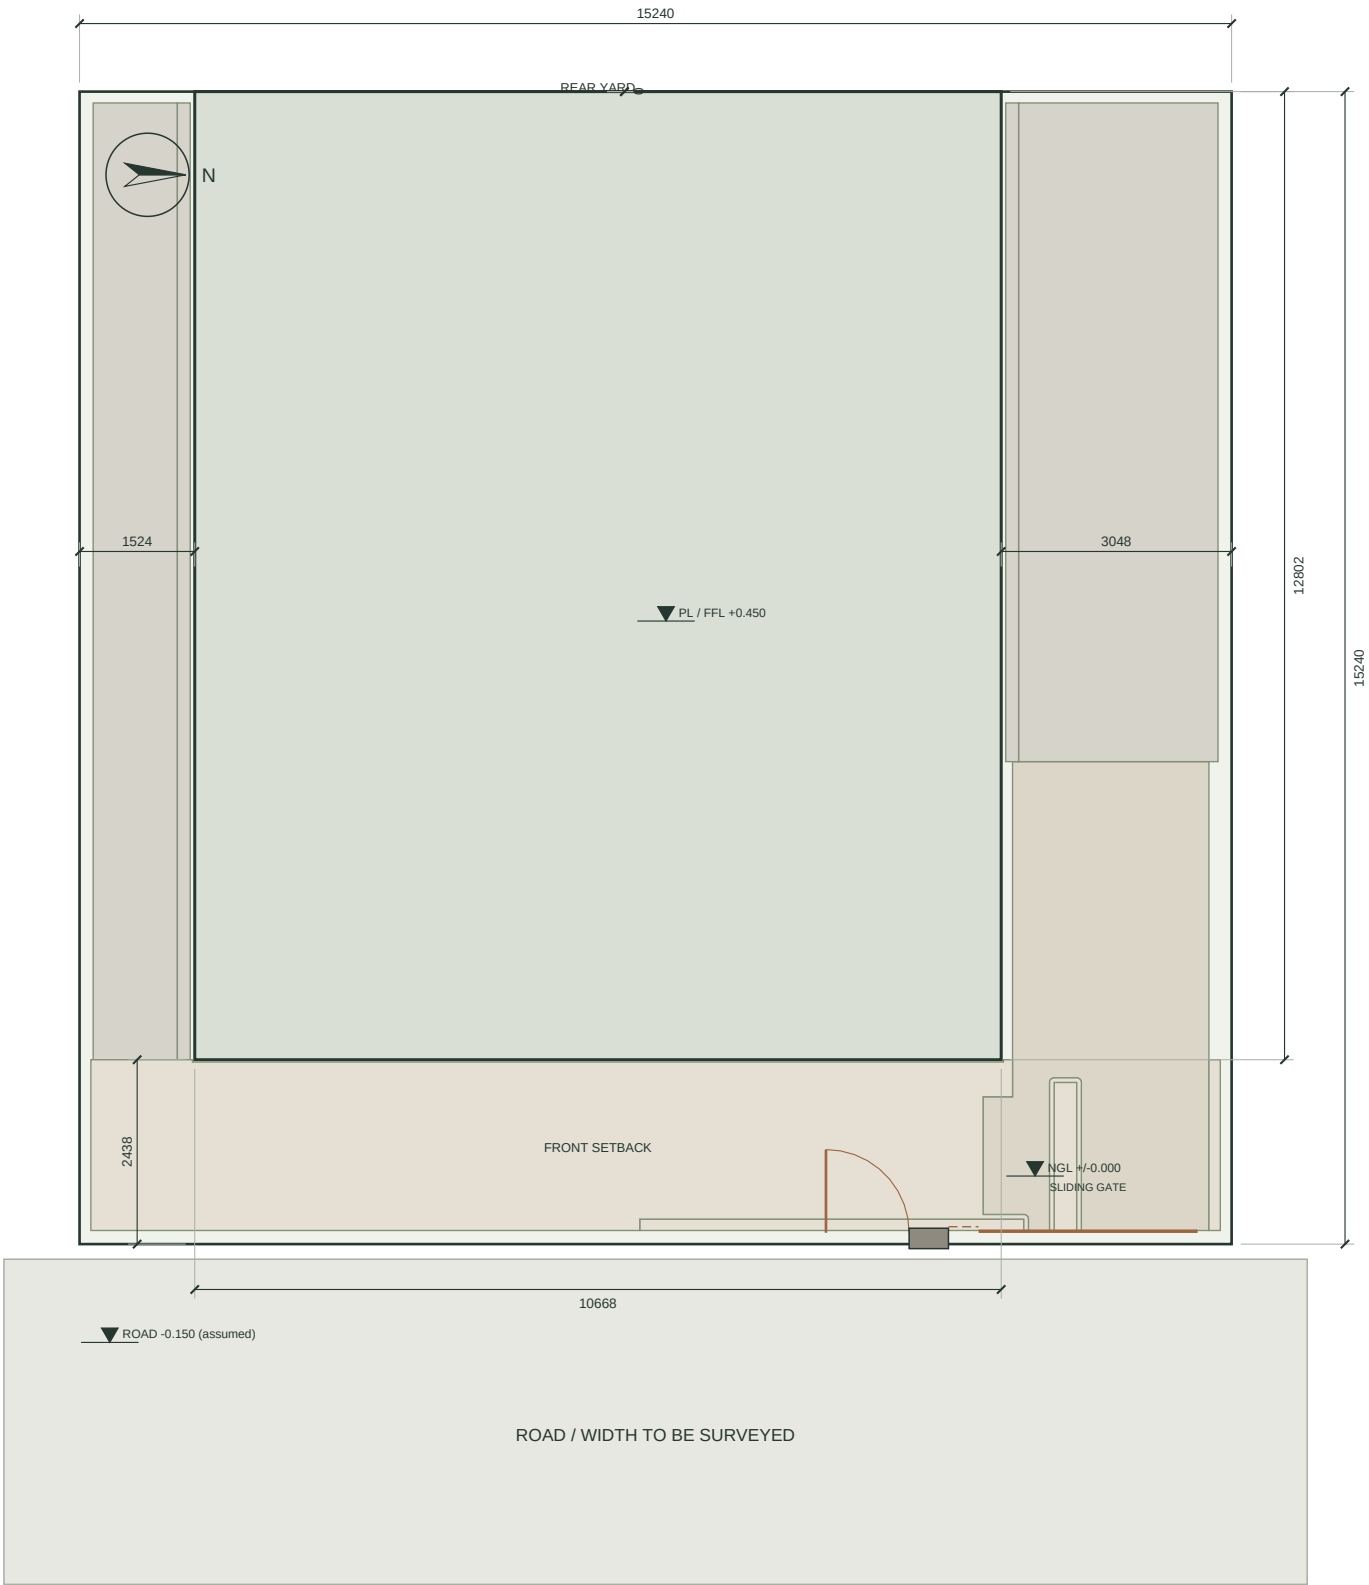

My Desired Home

AREA STATEMENT	VALUE	UNIT
Plot	232.258	m2
Footprint	136.572	m2
Gross floors	253.689	m2
Coverage	58.8	percent
Geometric FAR	1.092	ratio

DRAWING NOTES

Setbacks shown are design assumptions, not verified byelaws.

Road width, property line and levels need a survey.


No surveyed drainage fall or flood datum supplied.

Default steps are not a step-free route.

SCALE 1:100 AT A3 / CUT +1200 mm

Dimensions govern; do not scale from a screen.

Front elevation

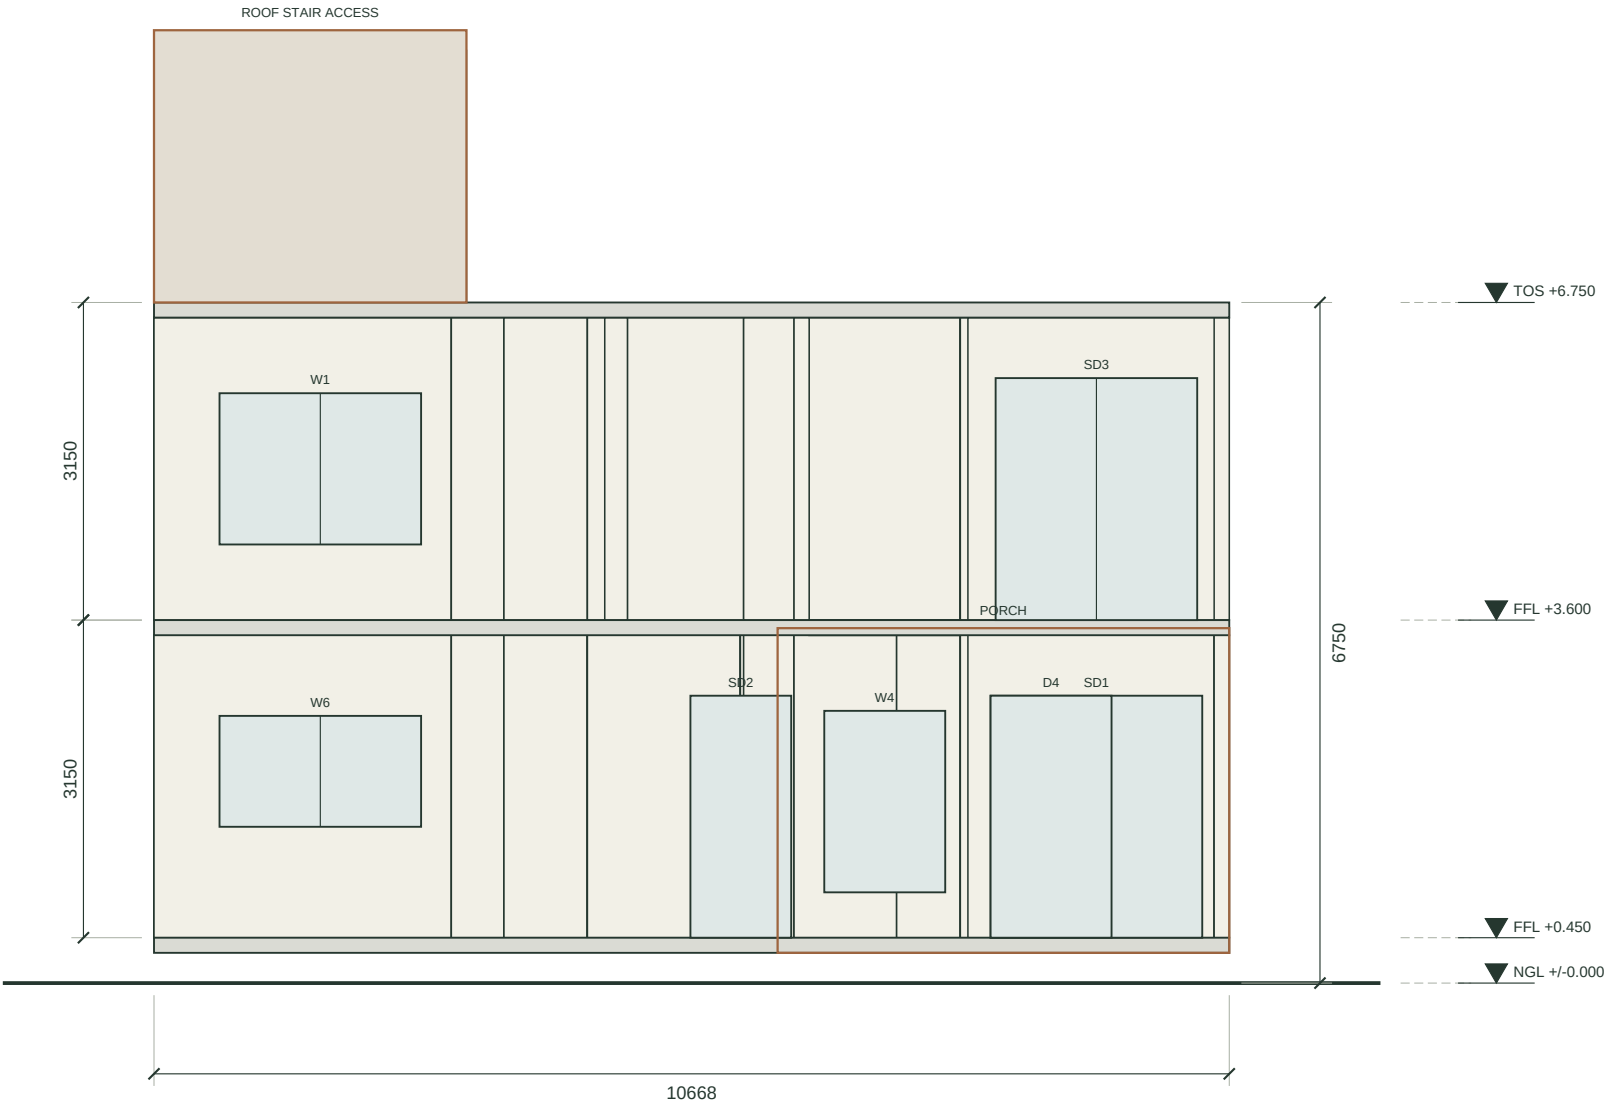

My Desired Home


DRAWING NOTES

- Wall and opening heights derive from the building model; levels in metres above NGL.
- This elevation records the primary wall plane.
- Decorative facade accessories are coordinated in 3D, not fully detailed here.
- No cladding anchors or construction joints are designed.

SCALE 1:75 AT A3 / CUT +1200 mm

Dimensions govern; do not scale from a screen.

Rear elevation

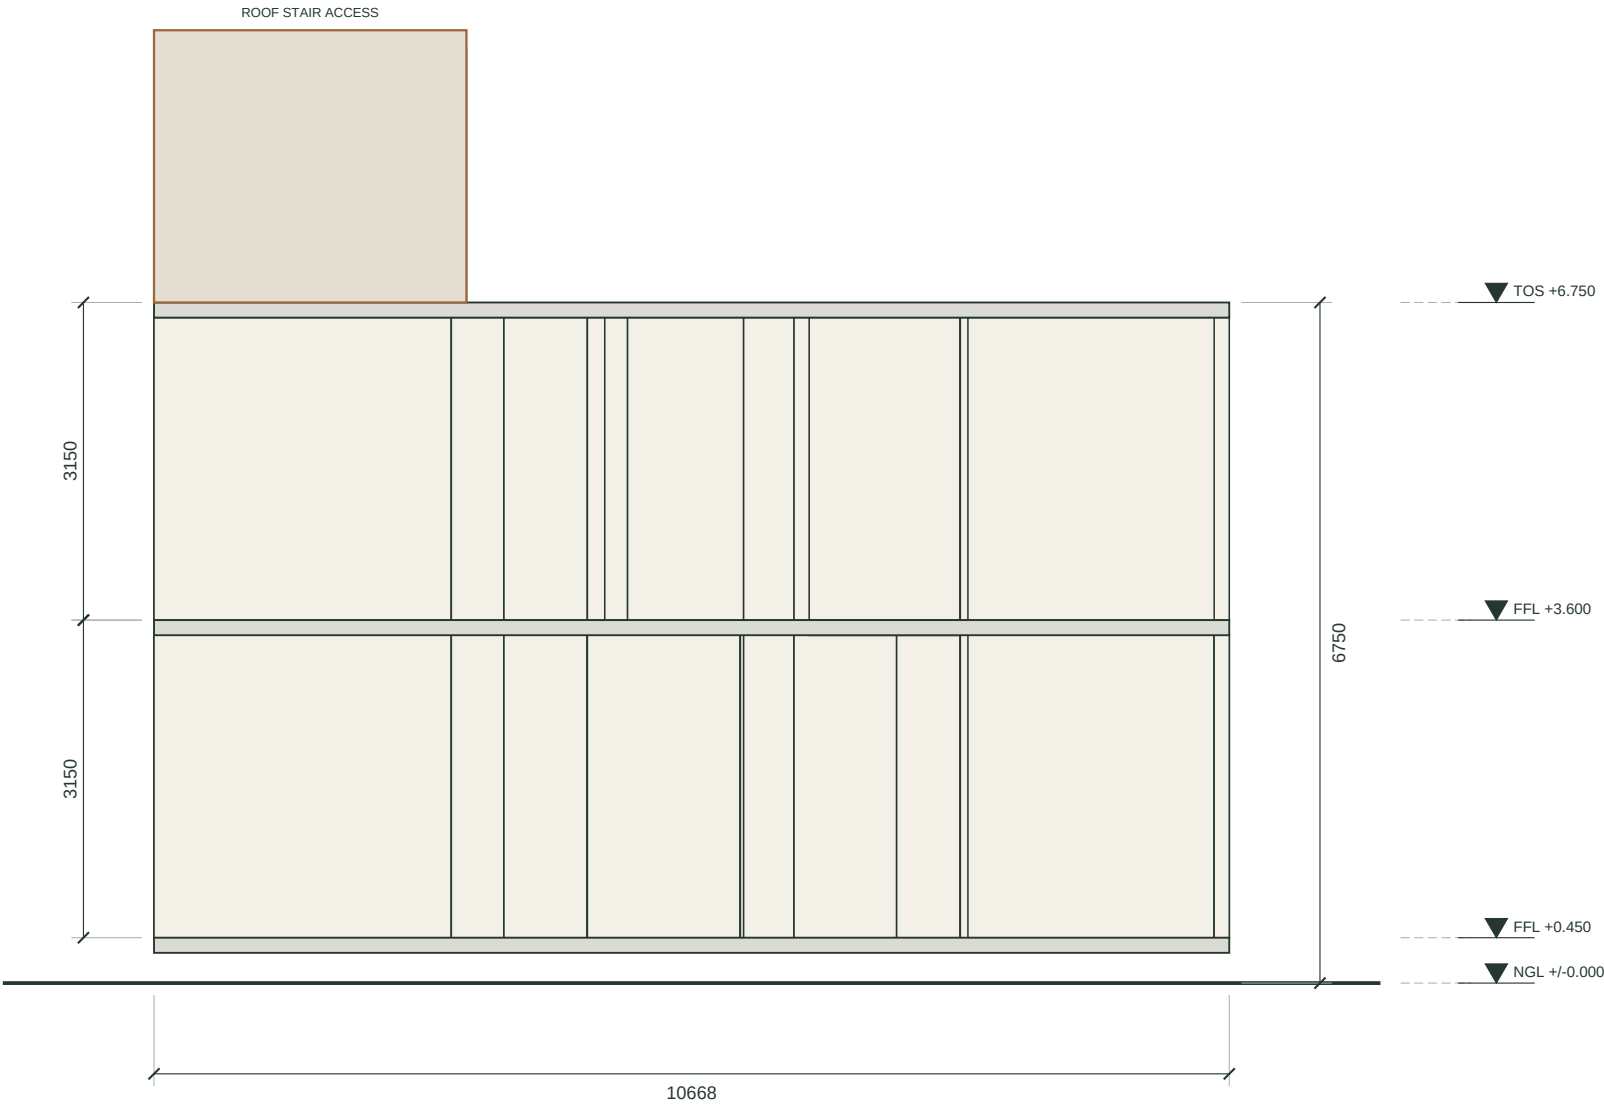

My Desired Home

DRAWING NOTES

Wall and opening heights derive from the building model; levels in metres above NGL.

This elevation records the primary wall plane.

Decorative facade accessories are coordinated in 3D, not fully detailed here.


No cladding anchors or construction joints are designed.

SCALE 1:75 AT A3 / CUT +1200 mm

Dimensions govern; do not scale from a screen.



Left elevation

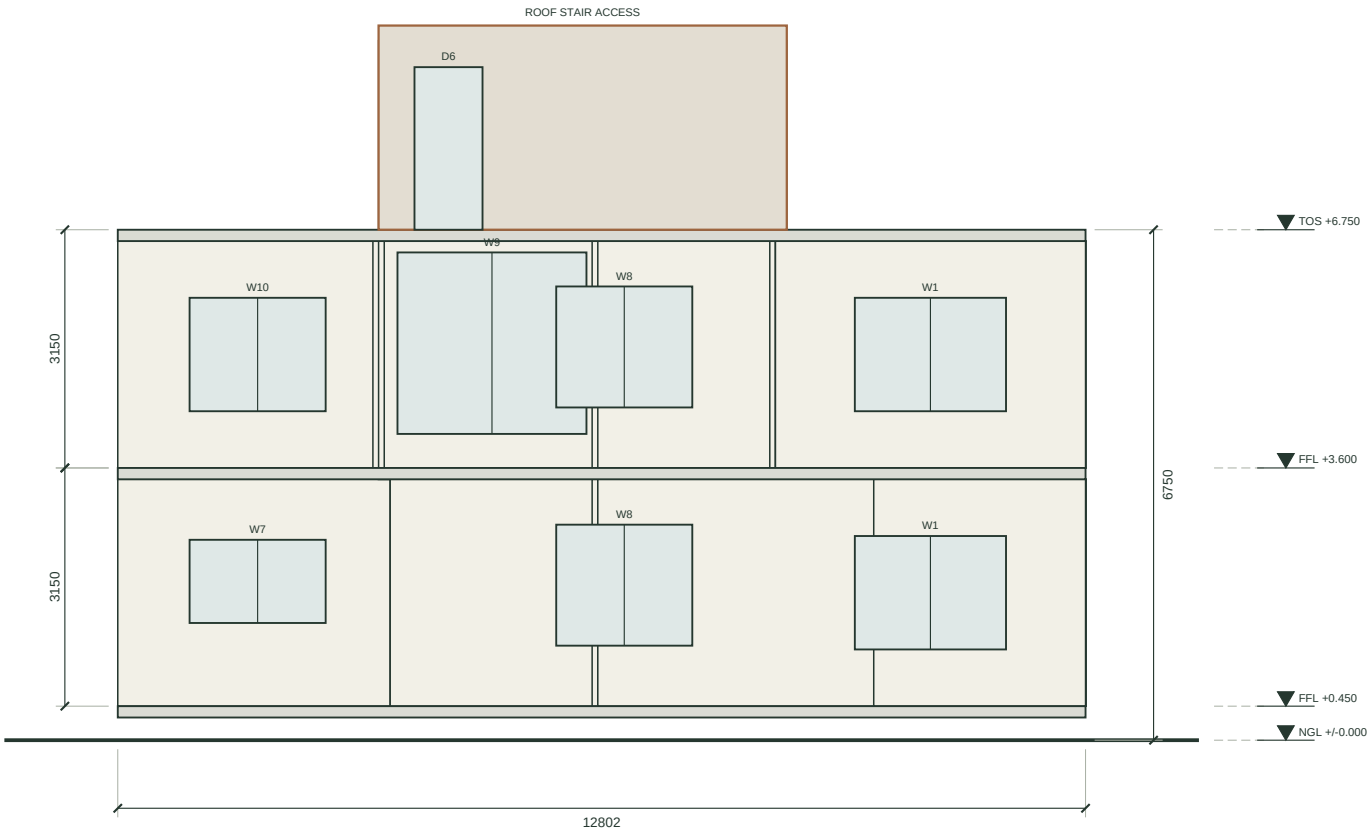

My Desired Home

DRAWING NOTES

Wall and opening heights derive from the building model; levels in metres above NGL.

This elevation records the primary wall plane.


Decorative facade accessories are coordinated in 3D, not fully detailed here.

No cladding anchors or construction joints are designed.


SCALE 1:100 AT A3 / CUT +1200 mm

Dimensions govern; do not scale from a screen.



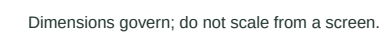

Section A-A / x = 0.80 m

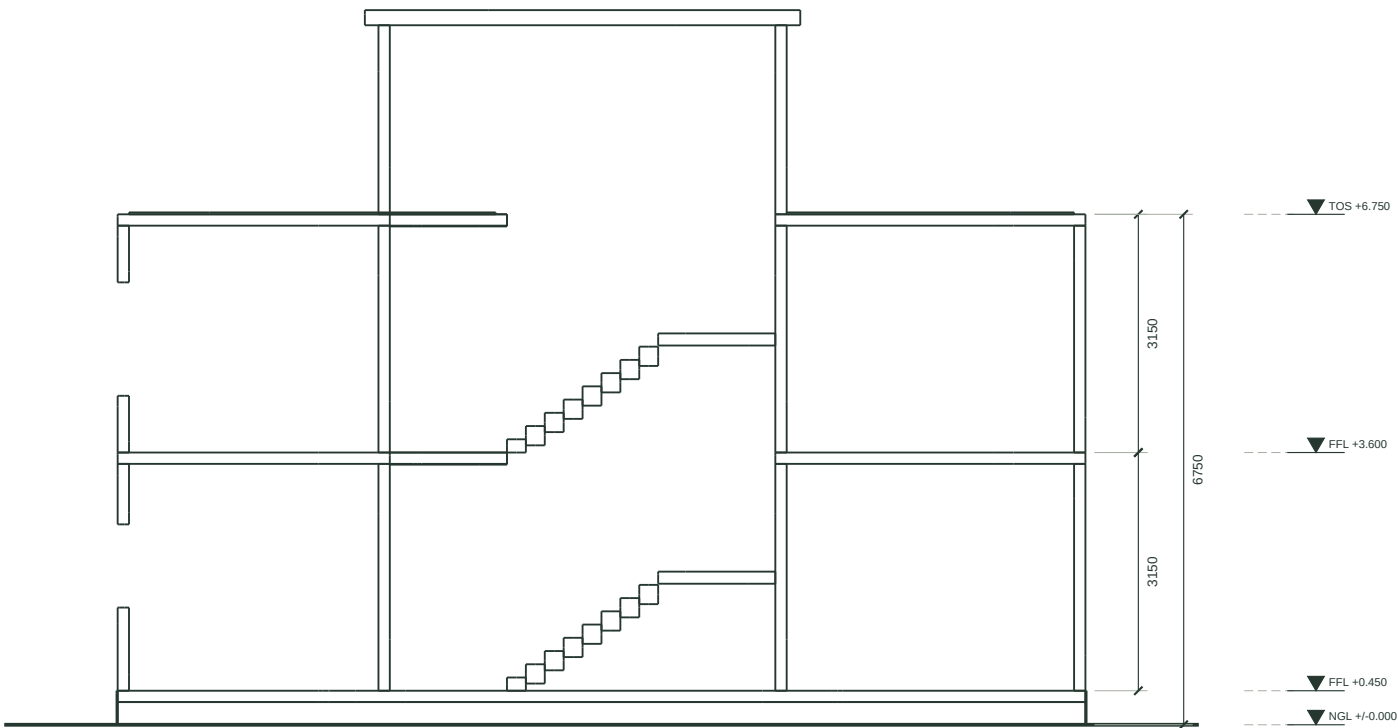

My Desired Home

DRAWING NOTES

Actual mesh-plane intersections, not a generic stair illustration.

Cut objects: walls, floor slabs, roof, stair and plinth. Levels in metres above NGL.

No reinforcement or foundation design is represented.

Stair headroom and handrails require a separate professional check.

SCALE 1:100 AT A3 / CUT +1200 mm


Dimensions govern; do not scale from a screen.

DOOR AND WINDOW SCHEDULE						ROOM SCHEDULE (CLEAR SIZE OF THE PRINCIPAL RECTANGLE)					
TAG	DESCRIPTION	SIZE W x H (mm)	SILL	NO.	LOCATION	SPACE	FLOOR	CLEAR SIZE (m)	CLEAR SIZE (ft-in)	AREA m2	AREA ft2
D1	Flush door, hardwood frame	850 x 2100	-	1	Common bathroom · rear	Common bathroom · rear	Ground	1.37 x 3.80	4'6" x 12'6"	5.20	56
D2	Flush door, hardwood frame	1000 x 2100	-	4	Master bedroom · southwest +3 more	Master bedroom · southwest	Ground	4.15 x 3.80	13'7" x 12'6"	15.78	170
D3	Flush door, water-resistant (WPC)	800 x 2100	-	1	Caregiver bedroom	Home care room	Ground	4.52 x 3.50	14'10" x 11'6"	17.44	188
D4	Main door, solid timber leaf in frame	1200 x 2400	-	1	Drawing room · northeast	Caregiver bedroom	Ground	3.00 x 2.50	9'10" x 8'3"	7.51	81
D5	Flush door, hardwood frame	1100 x 2100	-	2	Bedroom 3 · northwest, Office · southeast	Caregiver attached toilet	Ground	1.40 x 2.50	4'7" x 8'3"	3.50	38
D6	Flush door, hardwood frame	900 x 2150	-	1	Roof terrace	Open dining	Ground	2.73 x 3.30	8'11" x 10'10"	9.00	97
SD1	Sliding glazed door, aluminium	2100 x 2400	-	1	Home care room / Care veranda · north	Drawing room · northeast	Ground	4.02 x 3.30	13'2" x 10'10"	13.26	143
SD2	Sliding glazed door, aluminium	1000 x 2400	-	1	Open dining	Kitchen · southeast	Ground	3.32 x 3.30	10'11" x 10'10"	10.96	118
SD3	Sliding glazed door, aluminium	2000 x 2400	-	2	Living hall / Care veranda · north +1 more	Living hall	Ground	4.90 x 2.75	16'1" x 9'0"	17.81	192
SD4	Sliding glazed door, aluminium	1800 x 2400	-	1	Upper arrival lobby / East open terrace	Care veranda · north	Ground	2.52 x 2.75	8'3" x 9'0"	6.92	75
SD5	Sliding glazed door, aluminium	1400 x 2400	-	1	Overlooking living lobby / North open terrace	Upper bathroom	First	1.40 x 3.80	4'7" x 12'6"	5.32	57
O1	Cased opening, no leaf	1000 x 2400	-	1	Home care room / Living hall	Bedroom 3 · northwest	First	4.52 x 3.80	14'10" x 12'6"	17.18	185
O2	Cased opening, no leaf	1600 x 2400	-	1	Open dining / Drawing room · northeast	Bedroom 2 · southwest	First	4.15 x 3.80	13'7" x 12'6"	15.78	170
O3	Cased opening, no leaf	2728 x 3000	-	1	Open dining / Living hall	Double-height living · open below	First	3.38 x 2.75	11'1" x 9'0"	9.29	100
O4	Cased opening, no leaf	3300 x 3000	-	1	Open dining / Kitchen · southeast	Upper arrival lobby	First	2.73 x 3.30	8'11" x 10'10"	9.00	97
O5	Cased opening, no leaf	5100 x 3000	-	2	Living hall / Open staircase · south +1 more	Overlooking living lobby	First	4.90 x 2.20	16'1" x 7'3"	14.76	159
O6	Cased opening, no leaf	850 x 3000	-	1	Upper arrival lobby / Overlooking living lobby	Office · southeast	First	3.32 x 3.30	10'11" x 10'10"	10.96	118
W1	Sliding window, aluminium	2000 x 1500	750	4	Master bedroom · southwest +3 more	East open terrace	First	4.17 x 3.45	13'8" x 11'4"	14.38	155
W2	Sliding window, aluminium	750 x 1800	600	2	Home care room	North open terrace	First	2.52 x 5.25	8'3" x 17'3"	13.22	142
W3	Sliding window, aluminium	1400 x 1500	900	1	Caregiver bedroom	Roof terrace	Roof terrace	5.05 x 9.20	16'7" x 30'2"	92.01	990
W4	Sliding window, aluminium	1200 x 1800	450	1	Drawing room · northeast						
W5	Sliding window, aluminium	2000 x 1800	450	1	Drawing room · northeast						
W6	Sliding window, aluminium	2000 x 1100	1100	1	Kitchen · southeast						
W7	Sliding window, aluminium	1800 x 1100	1100	1	Kitchen · southeast						
W8	Sliding window, aluminium	1800 x 1600	800	2	Open staircase · south +1 more						
W9	Sliding window, aluminium	2500 x 2400	450	1	Double-height living · open below						
W10	Sliding window, aluminium	1800 x 1500	750	1	Office · southeast						

Nominal structural opening sizes; frames, tolerances and clear passage widths need detailing.

Room sizes are clear dimensions of the principal rectangle between finished wall faces.

Coordination axes / NOT a structural design

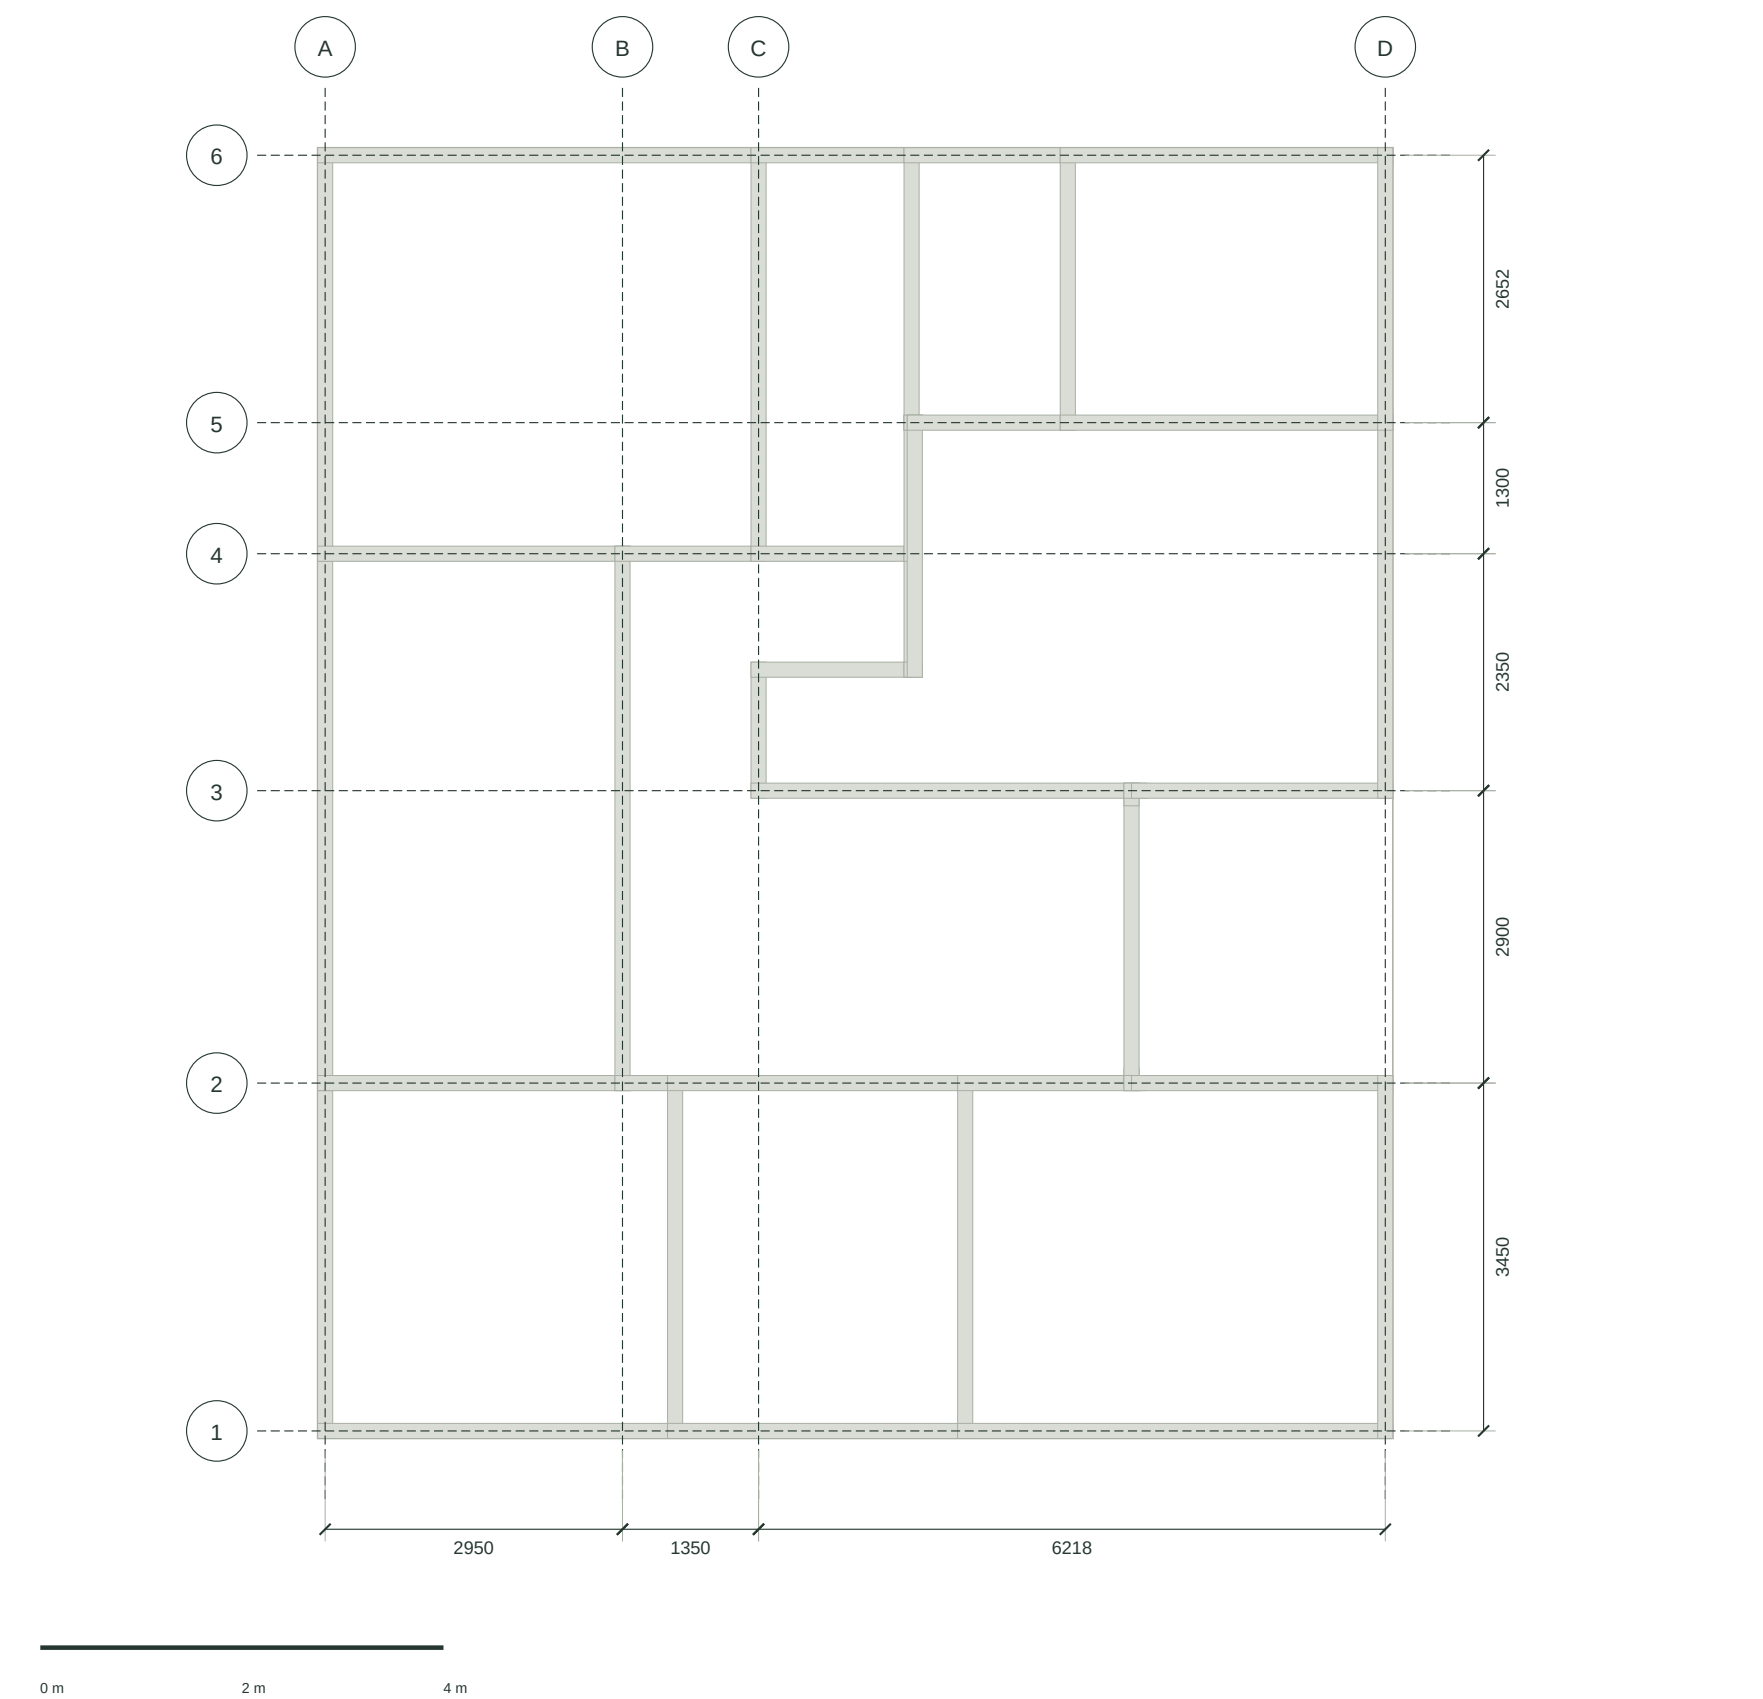

My Desired Home

DRAWING NOTES

- Axes follow the outer walls and the long interior walls; they are NOT column locations.
- No column, beam, slab or footing is sized or certified.
- Engineer must establish an actual load path and lateral system.
- No soil-bearing capacity is inferred from a soil photograph.

SCALE 1:75 AT A3 / CUT +1200 mm

Dimensions govern; do not scale from a screen.

FLOORFORGE / REVIEW / SCOPE

Geometry	preliminary_geometry_pass
Regulatory	NOT EVALUATED
Structure	NOT DESIGNED
Accessibility	NOT CERTIFIED

Passing geometric checks is not evidence of construction safety or statutory compliance.

Warning: Common bathroom · rear: mechanical exhaust selected; duct route and capacity require design.

Warning: Caregiver attached toilet: mechanical exhaust selected; duct route and capacity require design.

Warning: Upper bathroom: mechanical exhaust selected; duct route and capacity require design.

FLOORFORGE / COST / SCENARIO

Gross floor area	2730.69 ft2
Illustrative range	INR 60.08 - 84.11 lakh
Owner budget	INR 65.0 lakh
Rates	[2000.0, 2800.0] INR/ft2

Illustrative user-editable gross-plan-envelope rates, including open terrace cells. NOT a quote, tender, BOQ or market survey.

Excluded: land, approvals and professional fees, tax treatment, abnormal foundations, lifts, loose furniture, external services

No reinforcement quantities or cement bag counts are invented from floor area.

FLOORFORGE / SITE / SERVICES / STRUCTURE

Soil	unknown
Foundation recommendation	NOT PROVIDED: requires geotechnical design
Solar elevation	47.93 degrees
Vastu score	93 / advisory only

A soil name or photograph cannot establish bearing capacity, swelling or an appropriate foundation.

Cluster wet areas; a plumbing designer must size and route stacks, vents and gradients.

No electrical cable sizing, protection coordination or circuit approval.

No medical gas, life-support power or ICU services design.

Preference heuristic from supplied brief, not a safety or scientific rating. Strict requests are flagged, not guaranteed.

Solar method: NOAA-style closed-form solar study; no atmospheric refraction

FLOORFORGE / TIMELINE / ASSUMPTIONS

Survey, soil and approvals	Week 0 + 6 weeks
Foundations and substructure	Week 6 + 5 weeks
Frame and roof	Week 11 + 12 weeks
Masonry and services	Week 19 + 7 weeks
Finishes and joinery	Week 26 + 8 weeks
Testing and handover	Week 34 + 2 weeks

Illustrative overlapping phases, not a contractual or local construction schedule.

No government review period or supply lead time has been verified.

FLOORFORGE / OPENING SCHEDULE

D1	x1	Flush door, hardwood frame / 850 x 2100 / sill 0 mm
D2	x4	Flush door, hardwood frame / 1000 x 2100 / sill 0 mm
D3	x1	Flush door, water-resistant (WPC) / 800 x 2100 / sill 0 mm
D4	x1	Main door, solid timber leaf in frame / 1200 x 2400 / sill 0 mm
D5	x2	Flush door, hardwood frame / 1100 x 2100 / sill 0 mm
D6	x1	Flush door, hardwood frame / 900 x 2150 / sill 0 mm
SD1	x1	Sliding glazed door, aluminium / 2100 x 2400 / sill 0 mm
SD2	x1	Sliding glazed door, aluminium / 1000 x 2400 / sill 0 mm
SD3	x2	Sliding glazed door, aluminium / 2000 x 2400 / sill 0 mm
SD4	x1	Sliding glazed door, aluminium / 1800 x 2400 / sill 0 mm
SD5	x1	Sliding glazed door, aluminium / 1400 x 2400 / sill 0 mm
O1	x1	Cased opening, no leaf / 1000 x 2400 / sill 0 mm
O2	x1	Cased opening, no leaf / 1600 x 2400 / sill 0 mm
O3	x1	Cased opening, no leaf / 2728 x 3000 / sill 0 mm
O4	x1	Cased opening, no leaf / 3300 x 3000 / sill 0 mm
O5	x2	Cased opening, no leaf / 5100 x 3000 / sill 0 mm
O6	x1	Cased opening, no leaf / 850 x 3000 / sill 0 mm
W1	x4	Sliding window, aluminium / 2000 x 1500 / sill 750 mm
W2	x2	Sliding window, aluminium / 750 x 1800 / sill 600 mm
W3	x1	Sliding window, aluminium / 1400 x 1500 / sill 900 mm
W4	x1	Sliding window, aluminium / 1200 x 1800 / sill 450 mm
W5	x1	Sliding window, aluminium / 2000 x 1800 / sill 450 mm
W6	x1	Sliding window, aluminium / 2000 x 1100 / sill 1100 mm

Nominal wall opening dimensions. Frames, tolerances and clear passage require detailing.

FLOORFORGE / OPENING SCHEDULE

W7	x1	Sliding window, aluminium / 1800 x 1100 / sill 1100 mm
W8	x2	Sliding window, aluminium / 1800 x 1600 / sill 800 mm
W9	x1	Sliding window, aluminium / 2500 x 2400 / sill 450 mm
W10	x1	Sliding window, aluminium / 1800 x 1500 / sill 750 mm

Nominal wall opening dimensions. Frames, tolerances and clear passage require detailing.