


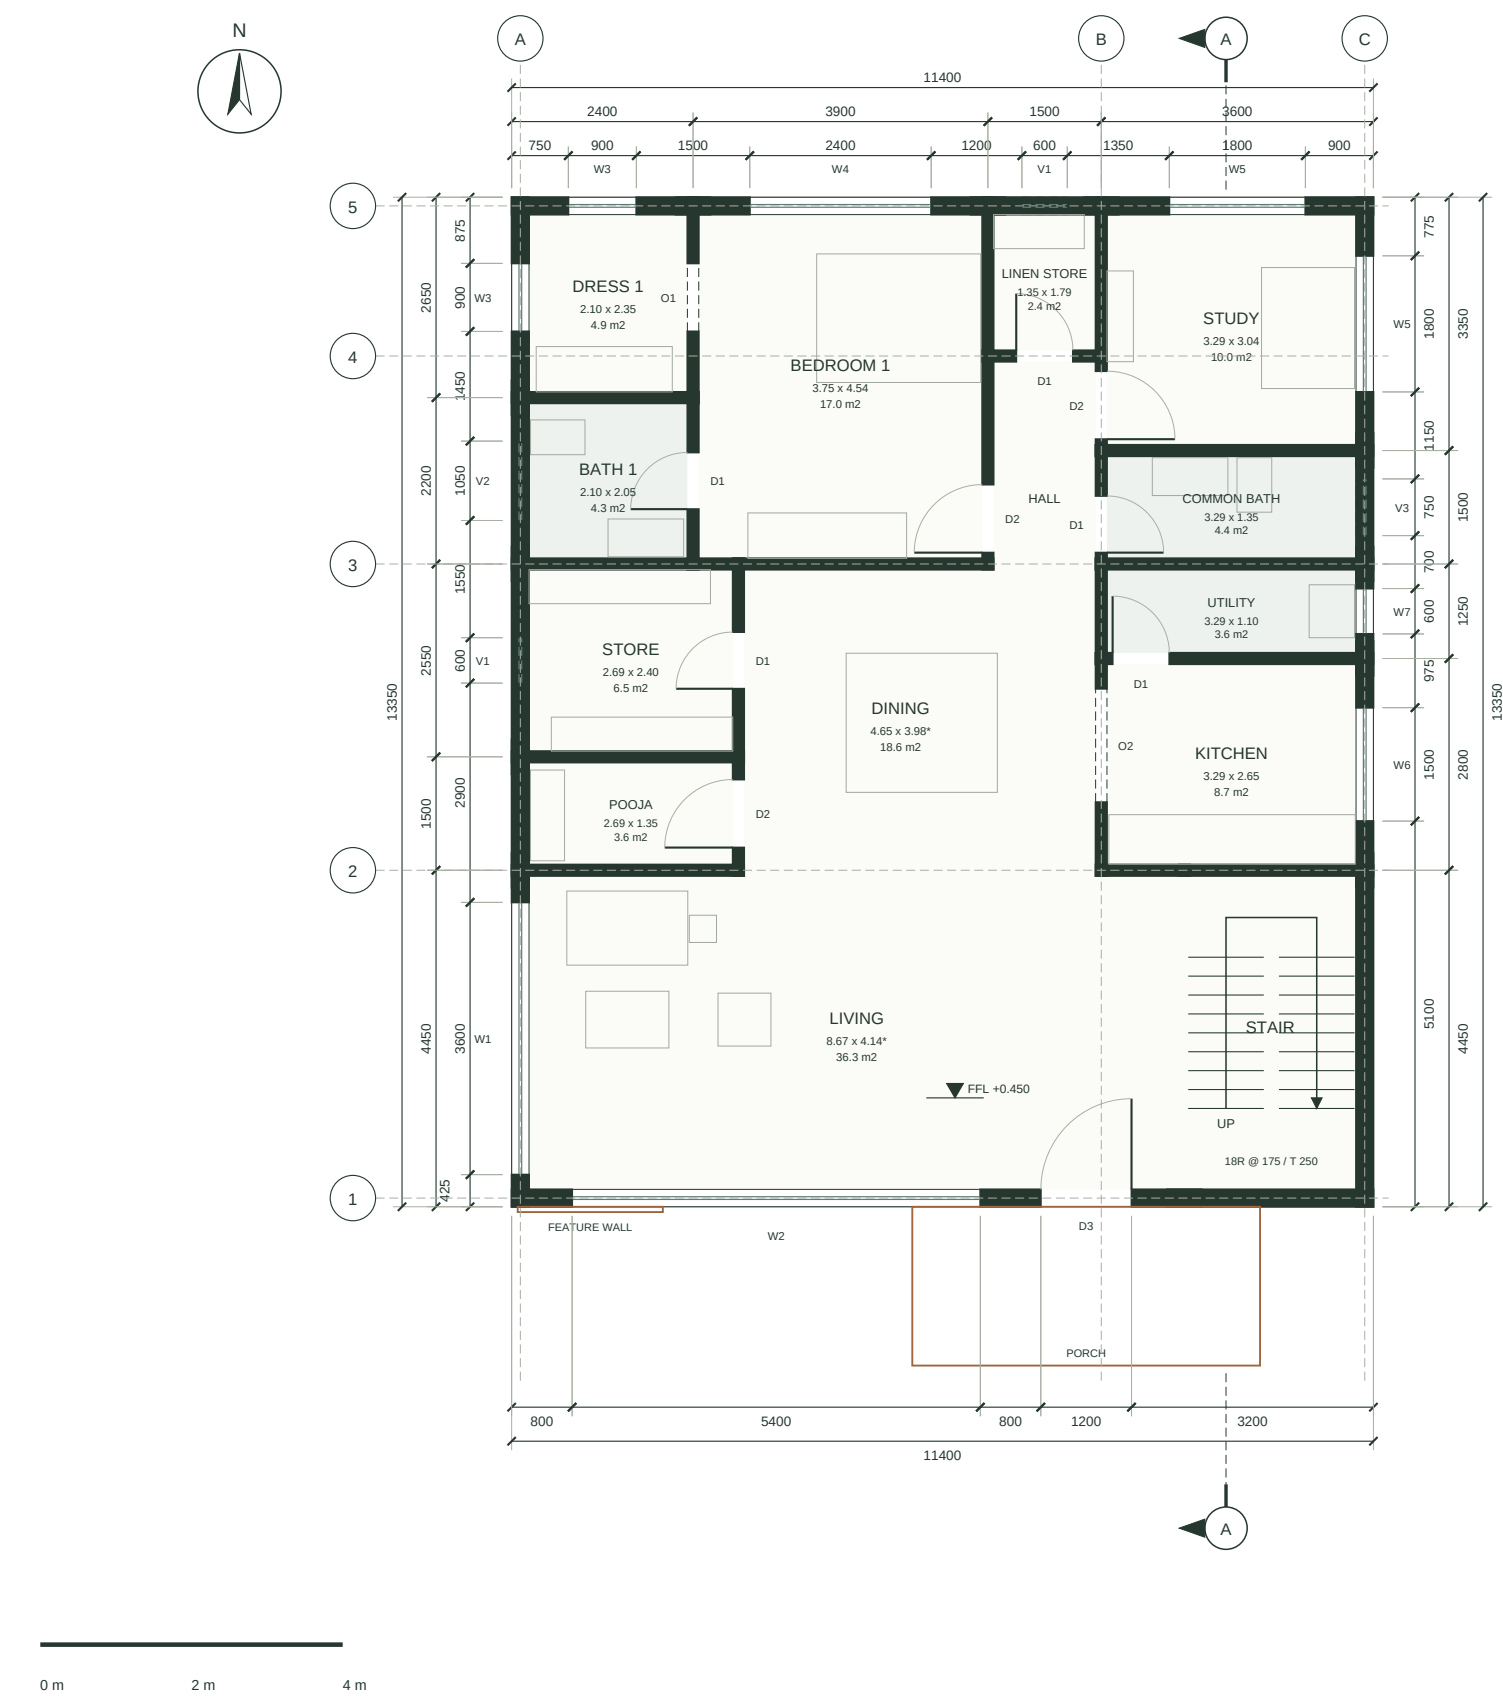

The Verandah House

SPACE	CLEAR SIZE m	AREA m2
Living	8.67 x 4.14*	36.29
Kitchen	3.29 x 2.65	8.73
Utility	3.29 x 1.10	3.62
Dining	4.65 x 3.98*	18.59
Pooja	2.69 x 1.35	3.64
Store	2.69 x 2.40	6.47
Hall	1.35 x 2.67	3.61
Linen store	1.35 x 1.79	2.42
Common bath	3.29 x 1.35	4.45
Study	3.29 x 3.04	10.03
Bedroom 1	3.75 x 4.54	17.04
Dress 1	2.10 x 2.35	4.91
Bath 1	2.10 x 2.05	4.29

DRAWING NOTES

All dimensions in millimetres; levels in metres above natural ground level (NGL).

Room sizes are clear sizes between finished wall faces; * marks the principal rectangle of an L-shaped room.

Dimension chains: openings, walls, overall. Tags: D door, SD sliding door, O cased opening, W window, V ventilator (see A-601).

Door leaves are drawn in the room they open into. Windows above the +1.2 m cut are dashed; furniture is schematic at true scale.

Grid bubbles are coordination axes only, not column positions.

No certified IS 962 or local-code compliance is claimed.

SCALE 1:100 AT A3 / CUT +1200 mm

Dimensions govern; do not scale from a screen.



The Verandah House

SPACE	CLEAR SIZE m	AREA m2
Family lounge	8.67 x 2.71*	28.66
Open terrace	4.79 x 1.44*	7.32
Hall	1.20 x 4.53	5.43
Study	5.25 x 3.20	16.78
Bedroom 2	4.65 x 4.00*	22.70
Dress 2	1.79 x 2.75	4.93
Bath 2	1.79 x 2.35	4.22
Master bedroom	4.20 x 6.05	25.38
Master dress	1.95 x 2.40	4.67
Master bath	2.10 x 2.40	5.02

DRAWING NOTES

All dimensions in millimetres; levels in metres above natural ground level (NGL).

Room sizes are clear sizes between finished wall faces; * marks the principal rectangle of an L-shaped room.


Dimension chains: openings, walls, overall. Tags: D door, SD sliding door, O cased opening, W window, V ventilator (see A-601).

Door leaves are drawn in the room they open into. Windows above the +1.2 m cut are dashed; furniture is schematic at true scale.

Grid bubbles are coordination axes only, not column positions. No certified IS 962 or local-code compliance is claimed.

SCALE 1:100 AT A3 / CUT +1200 mm

Dimensions govern; do not scale from a screen.

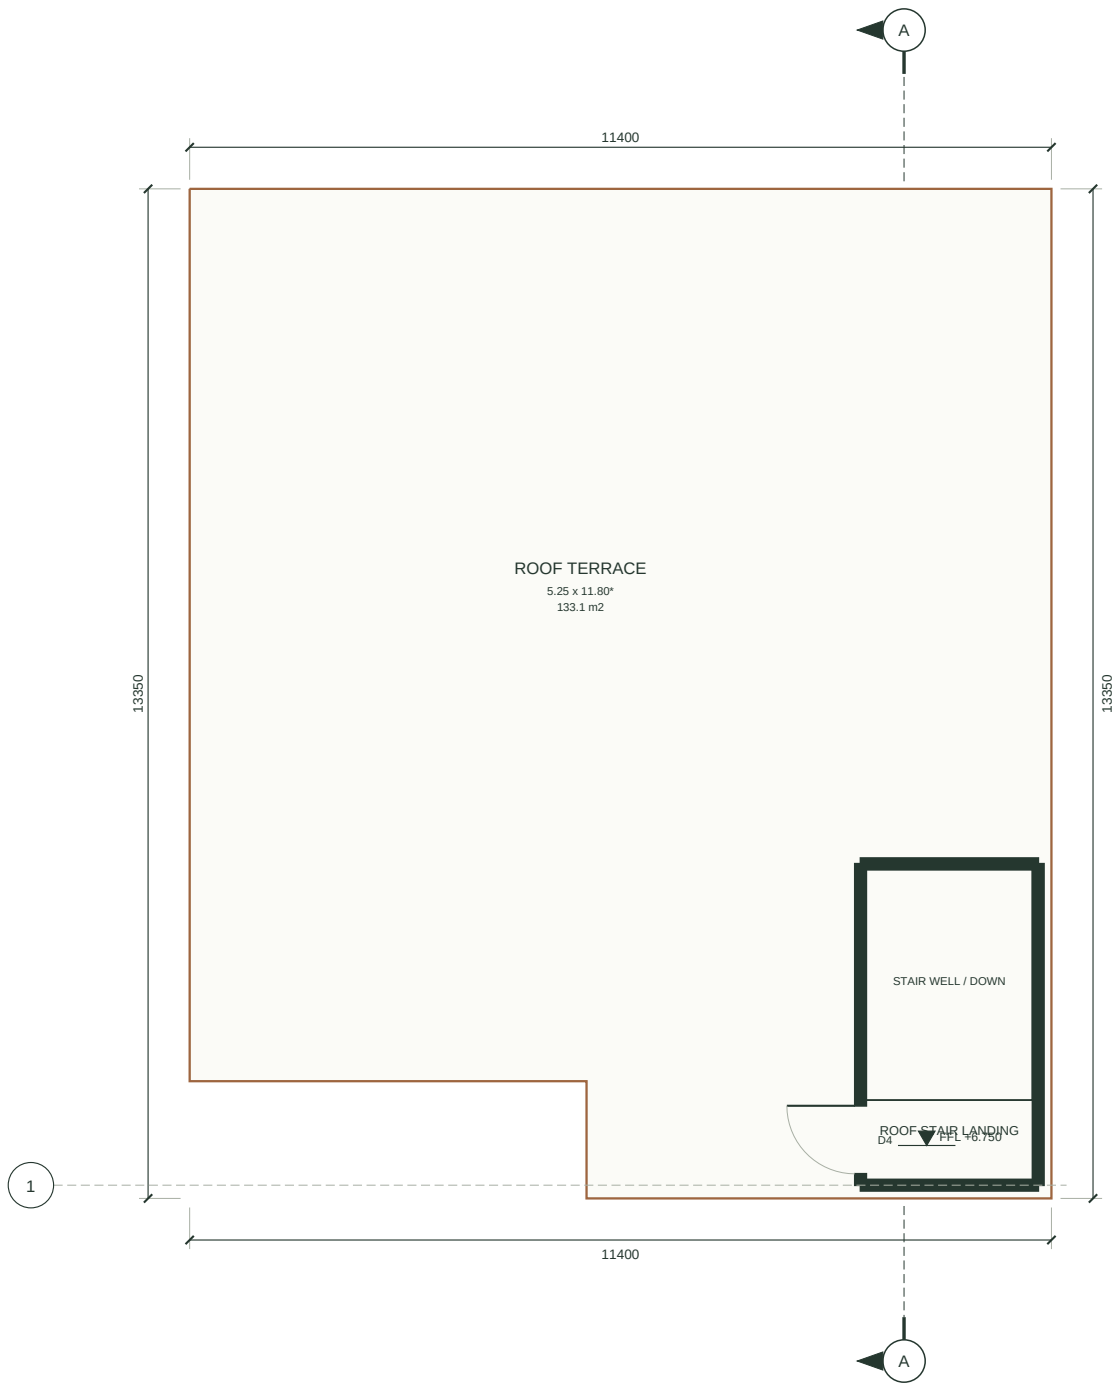

The Verandah House

SPACE	AREA m2
Open roof terrace	133.05

DRAWING NOTES


Roof access level, not an additional occupied storey.

Use the linked stair and its landing door to reach the guarded terrace.

Roof openings and headhouse positions follow the authored stair core.

SCALE 1:100 AT A3 / CUT +1200 mm

Dimensions govern; do not scale from a screen.

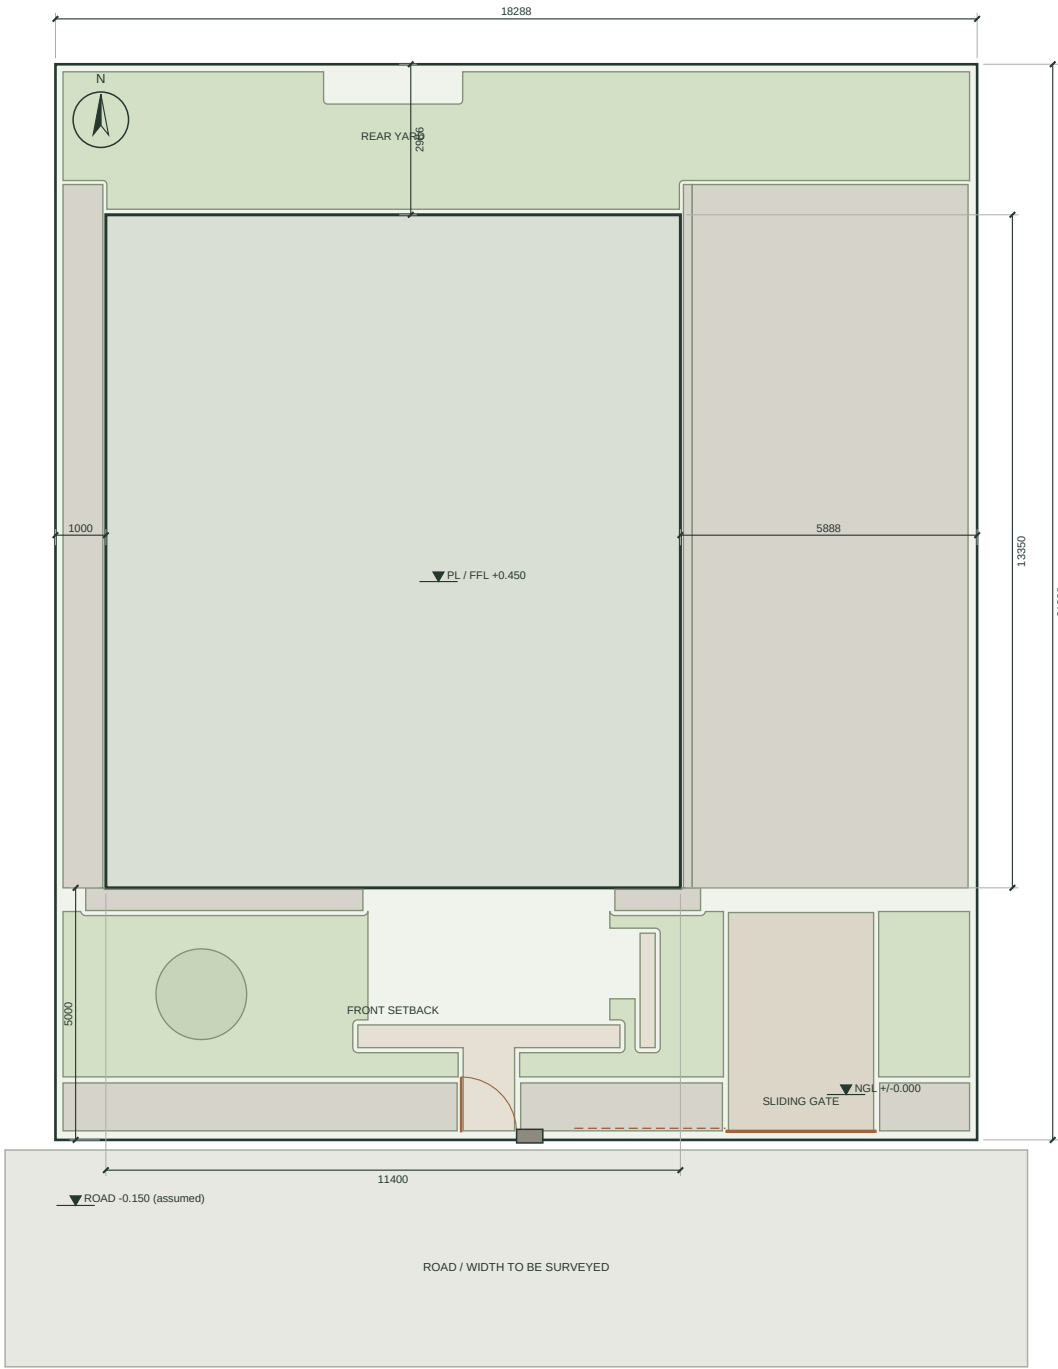

The Verandah House

AREA STATEMENT	VALUE	UNIT
Plot	390.193	m2
Footprint	152.19	m2
Gross floors	304.38	m2
Coverage	39.0	percent
Geometric FAR	0.78	ratio

DRAWING NOTES


- Setbacks shown are design assumptions, not verified byelaws.
- Road width, property line and levels need a survey.
- No surveyed drainage fall or flood datum supplied.
- Default steps are not a step-free route.

SCALE 1:150 AT A3 / CUT +1200 mm

Dimensions govern; do not scale from a screen.



Front elevation

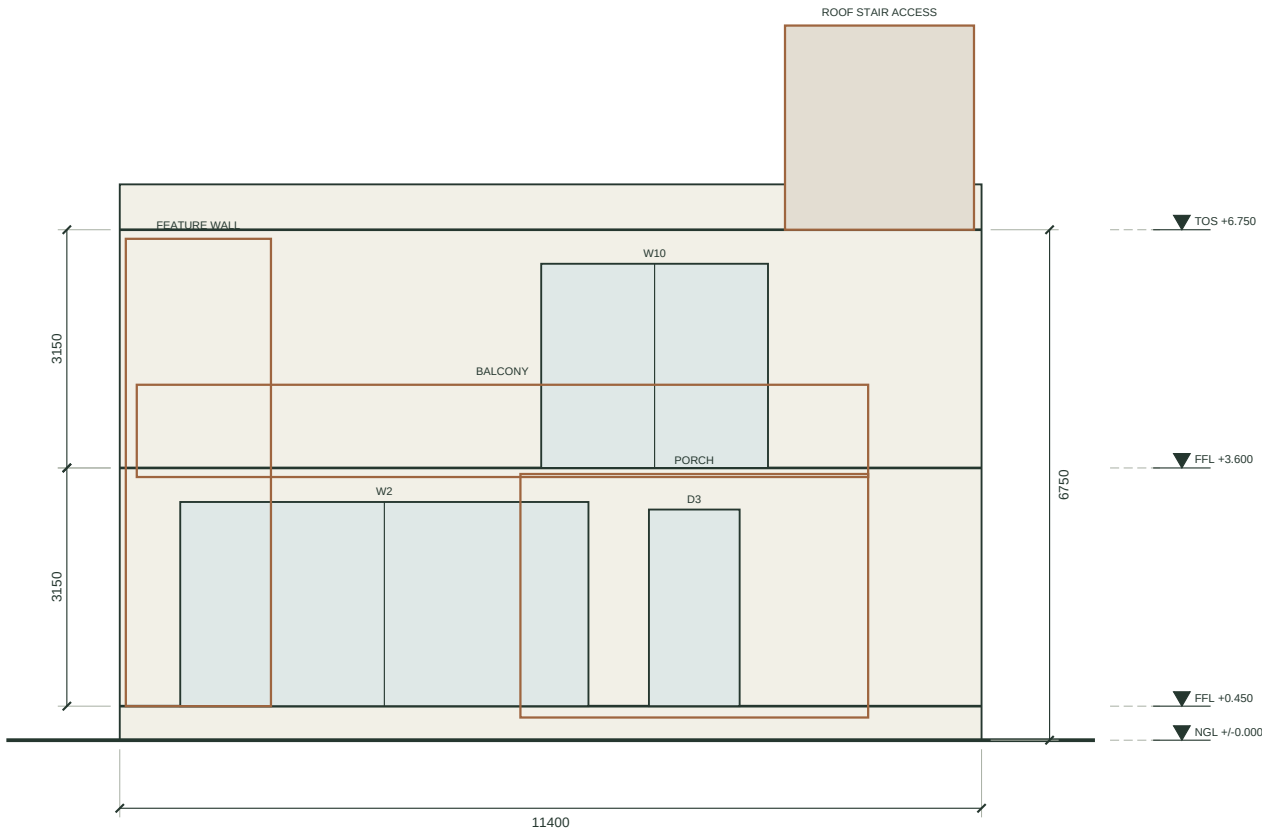

The Verandah House

DRAWING NOTES

Wall and opening heights derive from the building model; levels in metres above NGL.

This elevation records the primary wall plane.

Decorative facade accessories are coordinated in 3D, not fully detailed here.


No cladding anchors or construction joints are designed.

SCALE 1:100 AT A3 / CUT +1200 mm

Dimensions govern; do not scale from a screen.



Rear elevation

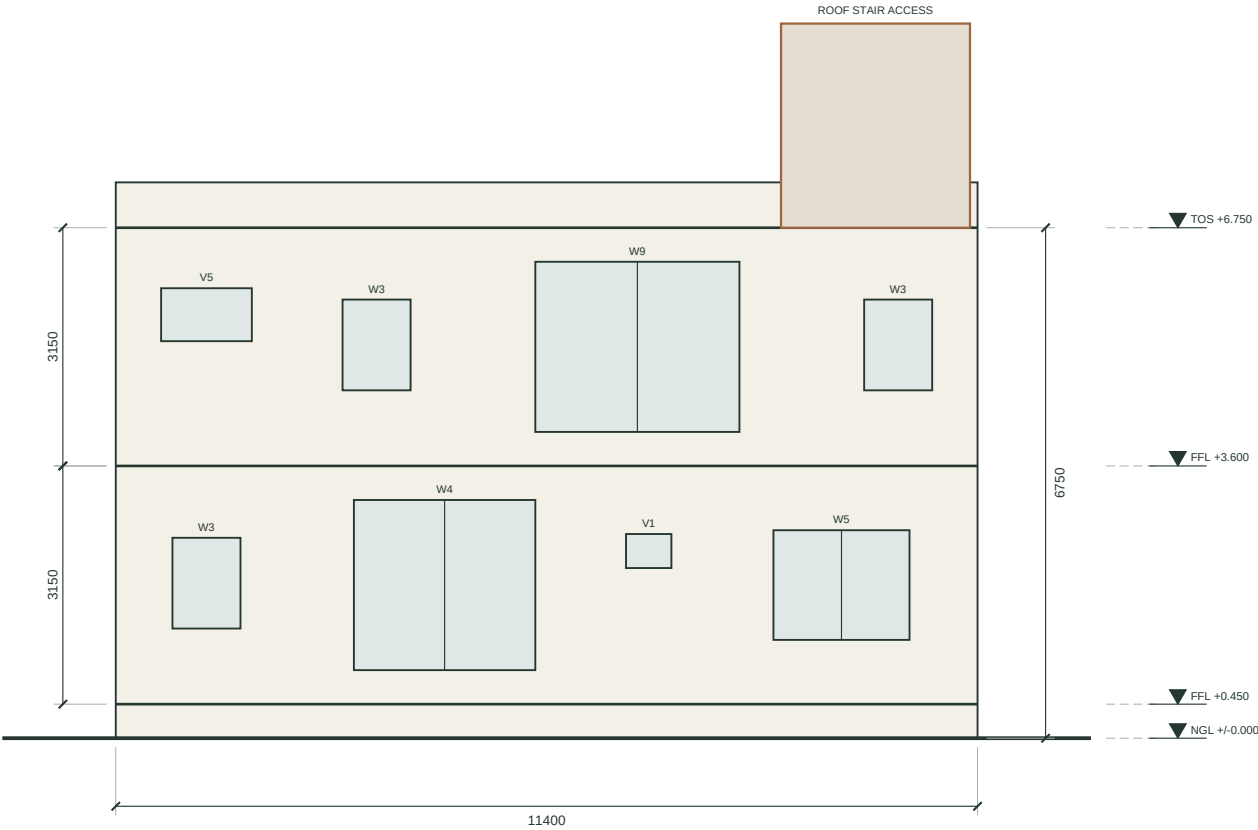

The Verandah House

DRAWING NOTES

Wall and opening heights derive from the building model; levels in metres above NGL.

This elevation records the primary wall plane.


Decorative facade accessories are coordinated in 3D, not fully detailed here.

No cladding anchors or construction joints are designed.

SCALE 1:100 AT A3 / CUT +1200 mm

Dimensions govern; do not scale from a screen.

Left elevation

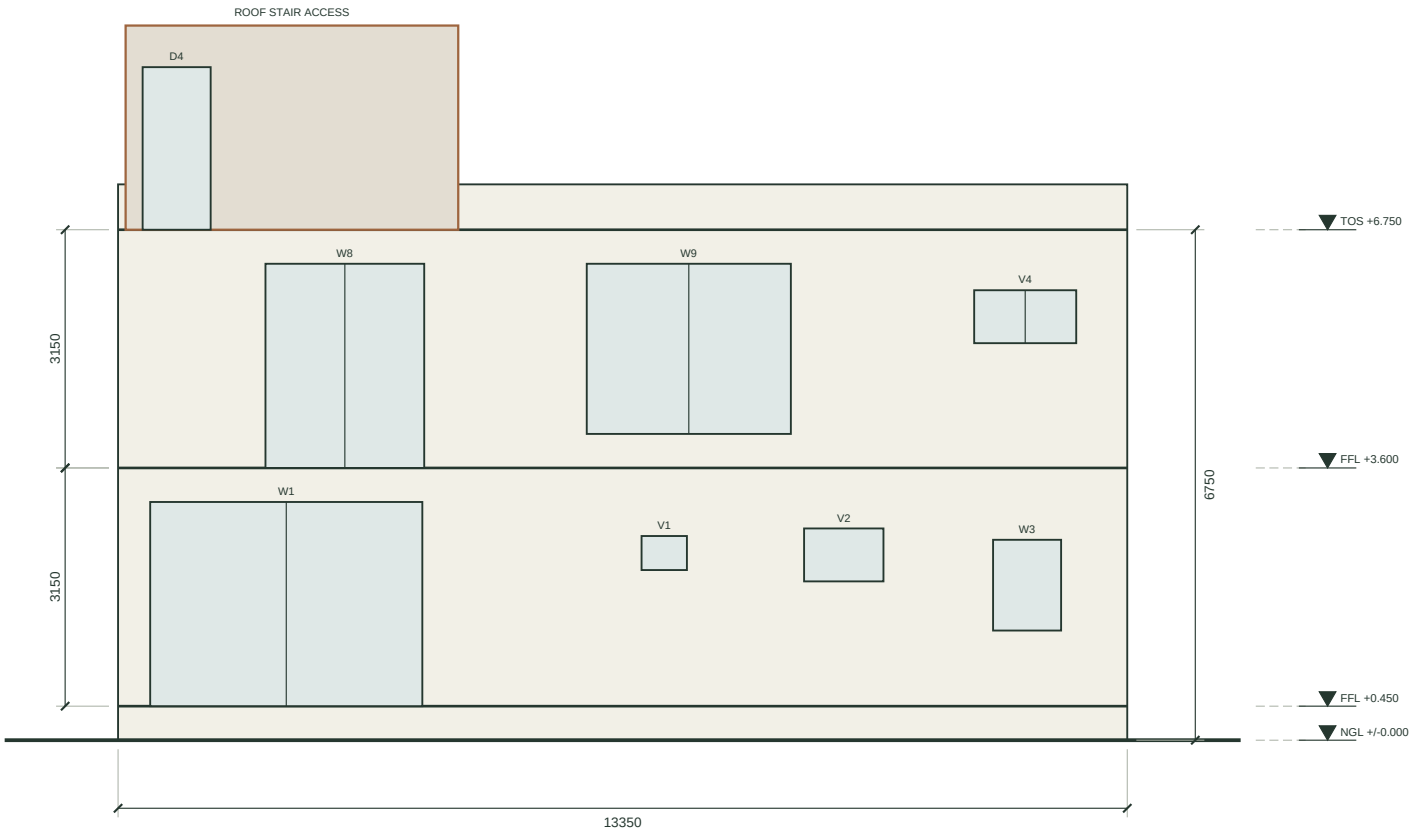

The Verandah House

DRAWING NOTES

Wall and opening heights derive from the building model; levels in metres above NGL.

This elevation records the primary wall plane.


Decorative facade accessories are coordinated in 3D, not fully detailed here.

No cladding anchors or construction joints are designed.

SCALE 1:100 AT A3 / CUT +1200 mm

Dimensions govern; do not scale from a screen.

Right elevation

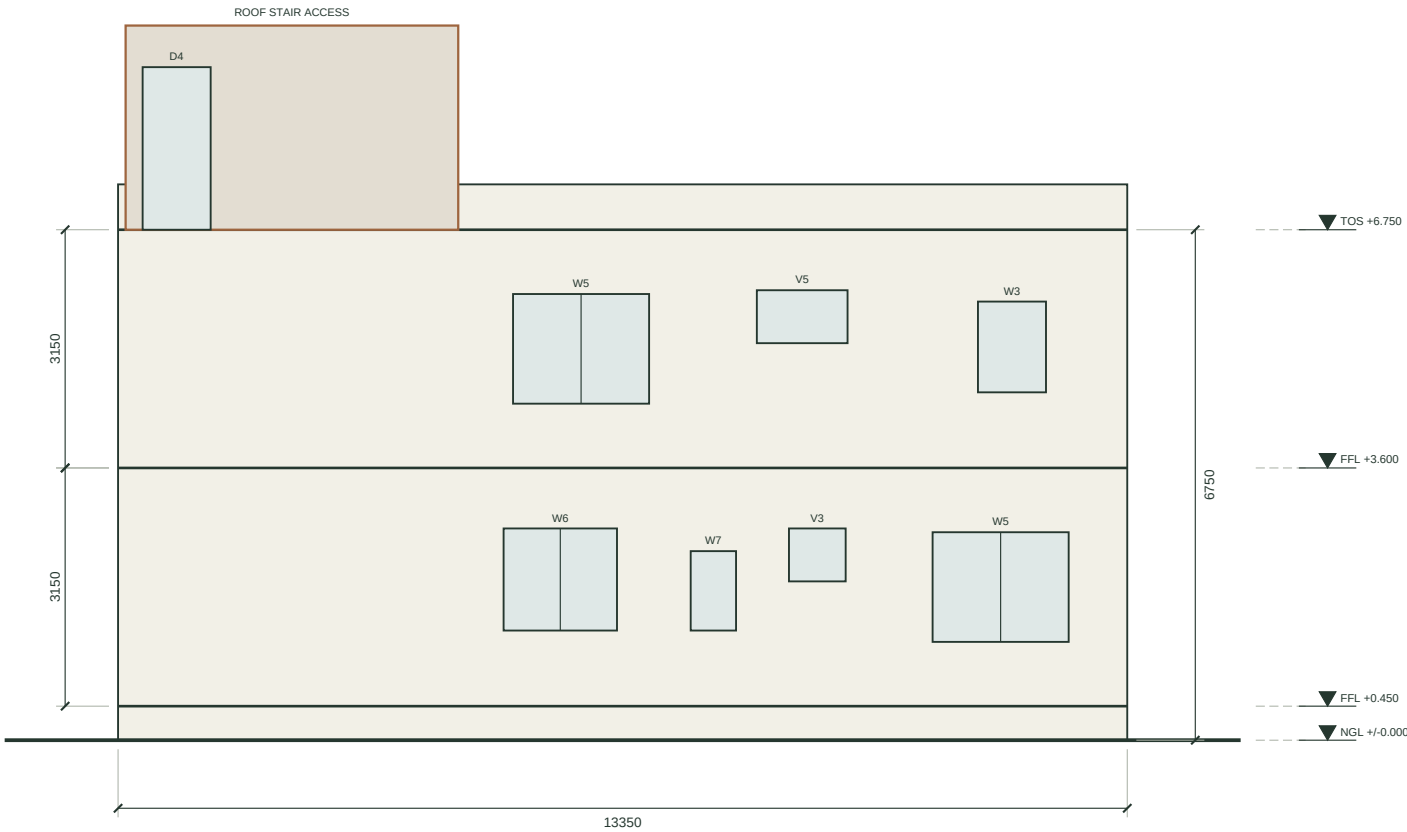

The Verandah House

DRAWING NOTES

Wall and opening heights derive from the building model; levels in metres above NGL.

This elevation records the primary wall plane.

Decorative facade accessories are coordinated in 3D, not fully detailed here.


No cladding anchors or construction joints are designed.

SCALE 1:100 AT A3 / CUT +1200 mm

Dimensions govern; do not scale from a screen.



Section A-A / x = 9.45 m

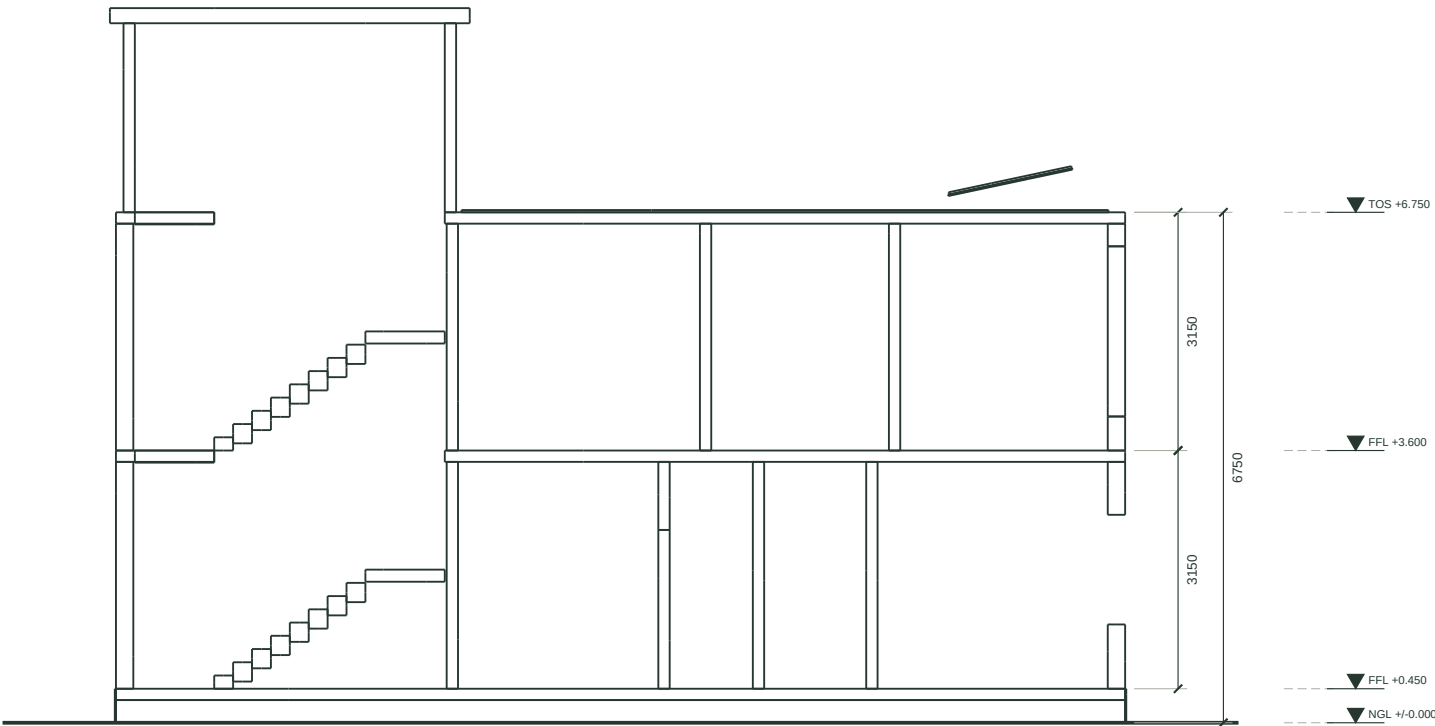

The Verandah House

DRAWING NOTES

Actual mesh-plane intersections, not a generic stair illustration.

Cut objects: walls, floor slabs, roof, stair and plinth. Levels in metres above NGL.

No reinforcement or foundation design is represented.

Stair headroom and handrails require a separate professional check.

SCALE 1:100 AT A3 / CUT +1200 mm


Dimensions govern; do not scale from a screen.



DOOR AND WINDOW SCHEDULE						ROOM SCHEDULE (CLEAR SIZE OF THE PRINCIPAL RECTANGLE)					
TAG	DESCRIPTION	SIZE W x H (mm)	SILL	NO.	LOCATION	SPACE	FLOOR	CLEAR SIZE (m)	CLEAR SIZE (ft-in)	AREA m2	AREA ft2
D1	Flush door, water-resistant (WPC)	750 x 2100	-	7	Bath 1, Common bath, Linen store +4 more	Living	Ground	8.67 x 4.14	28'5" x 13'7"	36.29	391
D2	Flush door, hardwood frame	900 x 2100	-	6	Bedroom 1, Pooja, Study, Bedroom 2 +1 more	Kitchen	Ground	3.29 x 2.65	10'10" x 8'8"	8.73	94
D3	Main door, solid timber leaf in frame	1200 x 2600	-	1	Living	Utility	Ground	3.29 x 1.10	10'10" x 3'7"	3.62	39
D4	Flush door, hardwood frame	900 x 2150	-	1	Roof terrace	Dining	Ground	4.65 x 3.98	15'3" x 13'0"	18.59	200
SD1	Sliding glazed door, aluminium	2700 x 2600	-	1	Family lounge / Open terrace	Pooja	Ground	2.69 x 1.35	8'10" x 4'5"	3.64	39
O1	Cased opening, no leaf	900 x 2100	-	3	Bedroom 1 / Dress 1 +2 more	Store	Ground	2.69 x 2.40	8'10" x 7'10"	6.47	70
O2	Cased opening, no leaf	1500 x 2100	-	1	Dining / Kitchen	Hall	Ground	1.35 x 2.67	4'5" x 8'9"	3.61	39
W1	Sliding window, aluminium	3600 x 2700	-	1	Living	Linen store	Ground	1.35 x 1.79	4'5" x 5'11"	2.42	26
W2	Sliding window, aluminium	5400 x 2700	-	1	Living	Common bath	Ground	3.29 x 1.35	10'10" x 4'5"	4.45	48
W3	Sliding window, aluminium	900 x 1200	1000	5	Dress 1, Master dress, Dress 2	Study	Ground	3.29 x 3.04	10'10" x 10'0"	10.03	108
W4	Sliding window, aluminium	2400 x 2250	450	1	Bedroom 1	Bedroom 1	Ground	3.75 x 4.54	12'4" x 14'11"	17.04	183
W5	Sliding window, aluminium	1800 x 1450	850	3	Study	Dress 1	Ground	2.10 x 2.35	6'10" x 7'8"	4.91	53
W6	Sliding window, aluminium	1500 x 1350	1000	1	Kitchen	Bath 1	Ground	2.10 x 2.05	6'10" x 6'9"	4.29	46
W7	Sliding window, aluminium	600 x 1050	1000	1	Utility	Family lounge	First	8.67 x 2.71	28'5" x 8'11"	28.66	308
W8	Sliding window, aluminium	2100 x 2700	-	1	Family lounge	Open terrace	First	4.79 x 1.44	15'9" x 4'8"	7.32	79
W9	Sliding window, aluminium	2700 x 2250	450	2	Master bedroom, Bedroom 2	Hall	First	1.20 x 4.53	3'11" x 14'10"	5.43	58
W10	Sliding window, aluminium	3000 x 2700	-	1	Family lounge	Study	First	5.25 x 3.20	17'2" x 10'6"	16.78	181
V1	Ventilator, obscured glass / louvres	600 x 450	1800	2	Store, Linen store	Bedroom 2	First	4.65 x 4.00	15'3" x 13'1"	22.70	244
V2	Ventilator, obscured glass / louvres	1050 x 700	1650	1	Bath 1	Dress 2	First	1.79 x 2.75	5'11" x 9'0"	4.93	53
V3	Ventilator, obscured glass / louvres	750 x 700	1650	1	Common bath	Bath 2	First	1.79 x 2.35	5'11" x 7'9"	4.22	45
V4	Ventilator, obscured glass / louvres	1350 x 700	1650	1	Master bath	Master bedroom	First	4.20 x 6.05	13'9" x 19'10"	25.38	273
V5	Ventilator, obscured glass / louvres	1200 x 700	1650	2	Master bath, Bath 2	Master dress	First	1.95 x 2.40	6'5" x 7'10"	4.67	50
						Master bath	First	2.10 x 2.40	6'10" x 7'10"	5.02	54
						Roof terrace	Roof terrace	11.40 x 11.80	37'5" x 38'9"	133.05	1432

Nominal structural opening sizes; frames, tolerances and clear passage widths need detailing.

Room sizes are clear dimensions of the principal rectangle between finished wall faces.

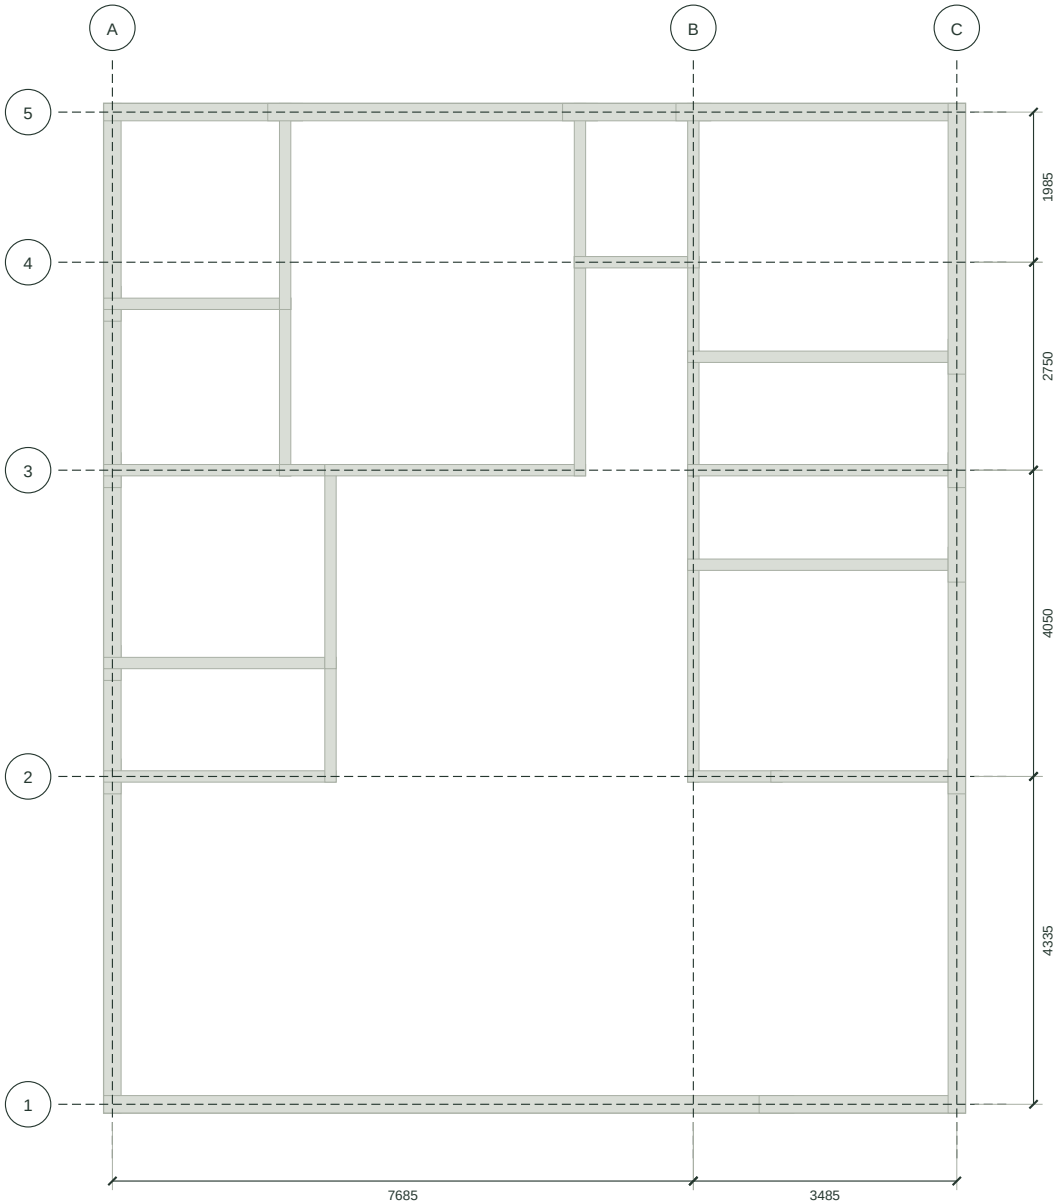

The Verandah House

DRAWING NOTES

Axes follow the outer walls and the long interior walls; they are NOT column locations.

No column, beam, slab or footing is sized or certified.

Engineer must establish an actual load path and lateral system.

No soil-bearing capacity is inferred from a soil photograph.

SCALE 1:100 AT A3 / CUT +1200 mm

Dimensions govern; do not scale from a screen.



FLOORFORGE / REVIEW / SCOPE

Geometry	preliminary_geometry_pass
Regulatory	NOT EVALUATED
Structure	NOT DESIGNED
Accessibility	NOT CERTIFIED

Passing geometric checks is not evidence of construction safety or statutory compliance.

FLOORFORGE / COST / SCENARIO

Gross floor area	3276.32 ft2
Illustrative range	INR 72.08 - 100.91 lakh
Owner budget	INR 65 lakh
Rates	[2000, 2800] INR/ft2

Illustrative user-editable gross-plan-envelope rates, including open terrace cells. NOT a quote, tender, BOQ or market survey.

Excluded: land, approvals and professional fees, tax treatment, abnormal foundations, lifts, loose furniture, external services

No reinforcement quantities or cement bag counts are invented from floor area.

FLOORFORGE / SITE / SERVICES / STRUCTURE

Soil	unknown
Foundation recommendation	NOT PROVIDED: requires geotechnical design
Solar elevation	47.93 degrees
Vastu score	19 / advisory only

A soil name or photograph cannot establish bearing capacity, swelling or an appropriate foundation.

Cluster wet areas; a plumbing designer must size and route stacks, vents and gradients.

No electrical cable sizing, protection coordination or circuit approval.

No medical gas, life-support power or ICU services design.

Preference heuristic from supplied brief, not a safety or scientific rating. Strict requests are flagged, not guaranteed.

Solar method: NOAA-style closed-form solar study; no atmospheric refraction

FLOORFORGE / TIMELINE / ASSUMPTIONS

Survey, soil and approvals	Week 0 + 6 weeks
Foundations and substructure	Week 6 + 5 weeks
Frame and roof	Week 11 + 12 weeks
Masonry and services	Week 19 + 7 weeks
Finishes and joinery	Week 26 + 8 weeks
Testing and handover	Week 34 + 2 weeks

Illustrative overlapping phases, not a contractual or local construction schedule.

No government review period or supply lead time has been verified.

FLOORFORGE / OPENING SCHEDULE

D1	x7	Flush door, water-resistant (WPC) / 750 x 2100 / sill 0 mm
D2	x6	Flush door, hardwood frame / 900 x 2100 / sill 0 mm
D3	x1	Main door, solid timber leaf in frame / 1200 x 2600 / sill 0 mm
D4	x1	Flush door, hardwood frame / 900 x 2150 / sill 0 mm
SD1	x1	Sliding glazed door, aluminium / 2700 x 2600 / sill 0 mm
O1	x3	Cased opening, no leaf / 900 x 2100 / sill 0 mm
O2	x1	Cased opening, no leaf / 1500 x 2100 / sill 0 mm
W1	x1	Sliding window, aluminium / 3600 x 2700 / sill 0 mm
W2	x1	Sliding window, aluminium / 5400 x 2700 / sill 0 mm
W3	x5	Sliding window, aluminium / 900 x 1200 / sill 1000 mm
W4	x1	Sliding window, aluminium / 2400 x 2250 / sill 450 mm
W5	x3	Sliding window, aluminium / 1800 x 1450 / sill 850 mm
W6	x1	Sliding window, aluminium / 1500 x 1350 / sill 1000 mm
W7	x1	Sliding window, aluminium / 600 x 1050 / sill 1000 mm
W8	x1	Sliding window, aluminium / 2100 x 2700 / sill 0 mm
W9	x2	Sliding window, aluminium / 2700 x 2250 / sill 450 mm
W10	x1	Sliding window, aluminium / 3000 x 2700 / sill 0 mm
V1	x2	Ventilator, obscured glass / louvres / 600 x 450 / sill 1800 mm
V2	x1	Ventilator, obscured glass / louvres / 1050 x 700 / sill 1650 mm
V3	x1	Ventilator, obscured glass / louvres / 750 x 700 / sill 1650 mm
V4	x1	Ventilator, obscured glass / louvres / 1350 x 700 / sill 1650 mm
V5	x2	Ventilator, obscured glass / louvres / 1200 x 700 / sill 1650 mm

Nominal wall opening dimensions. Frames, tolerances and clear passage require detailing.