


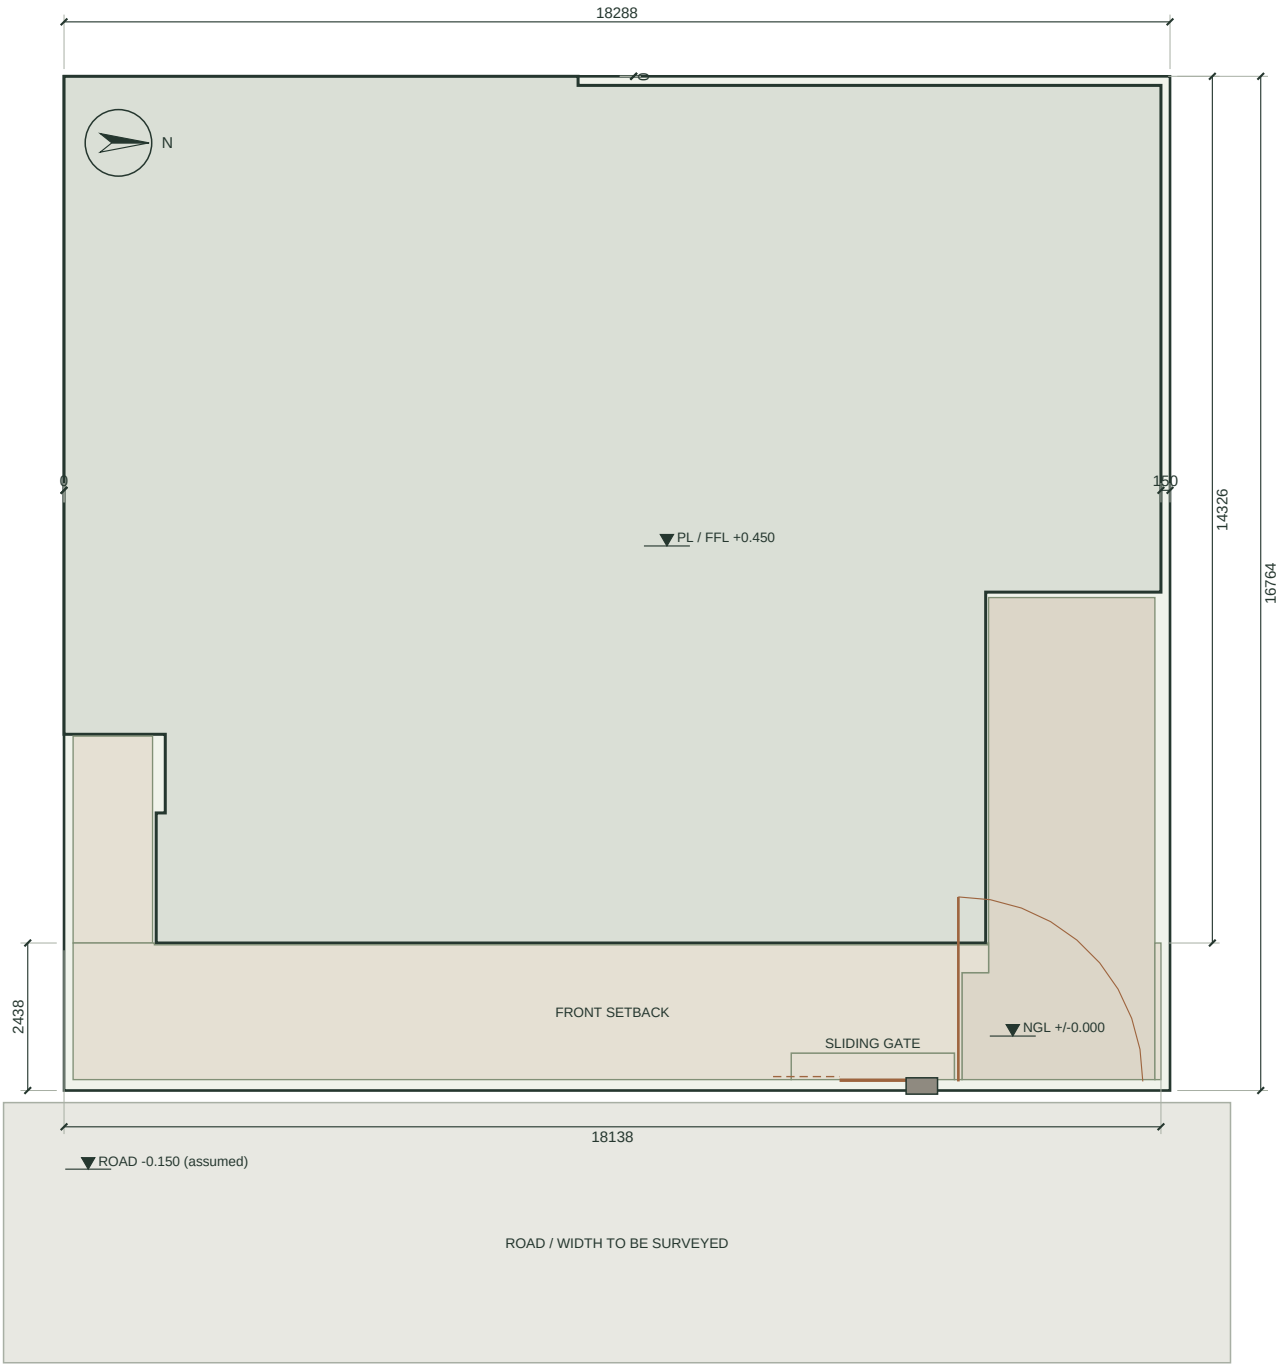

PROJECT BRIEF

PLOT
18288 x 16764 mm / 60 x 55 ft

ORIENTATION
East road / north points right

STOREYS
Ground + first + roof access

PLOT AREA
306.58 m2 / 3300 ft2


FLOOR RISE
3150 mm between occupied floors

MODEL WALLS
150 mm nominal thickness

PRINT SET CONTENTS

- | | |
|-------|--------------------------------|
| A-101 | Ground floor / 1:100 |
| A-102 | First floor / 1:100 |
| A-104 | Roof and stair access / 1:100 |
| A-301 | Measured model section / 1:100 |
| P-101 | Ground floor 3D cutaway |
| P-102 | First floor 3D cutaway |
| P-103 | Exterior and roof 3D views |
| A-601 | Clear room sizes and areas |
| A-602 | Door and window sizes |
| A-901 | Civil engineer review brief |

The 2438 mm front court and boundary-reaching side / rear portions are authored assumptions. Local setbacks, road width and property levels must be checked before this layout is adopted.

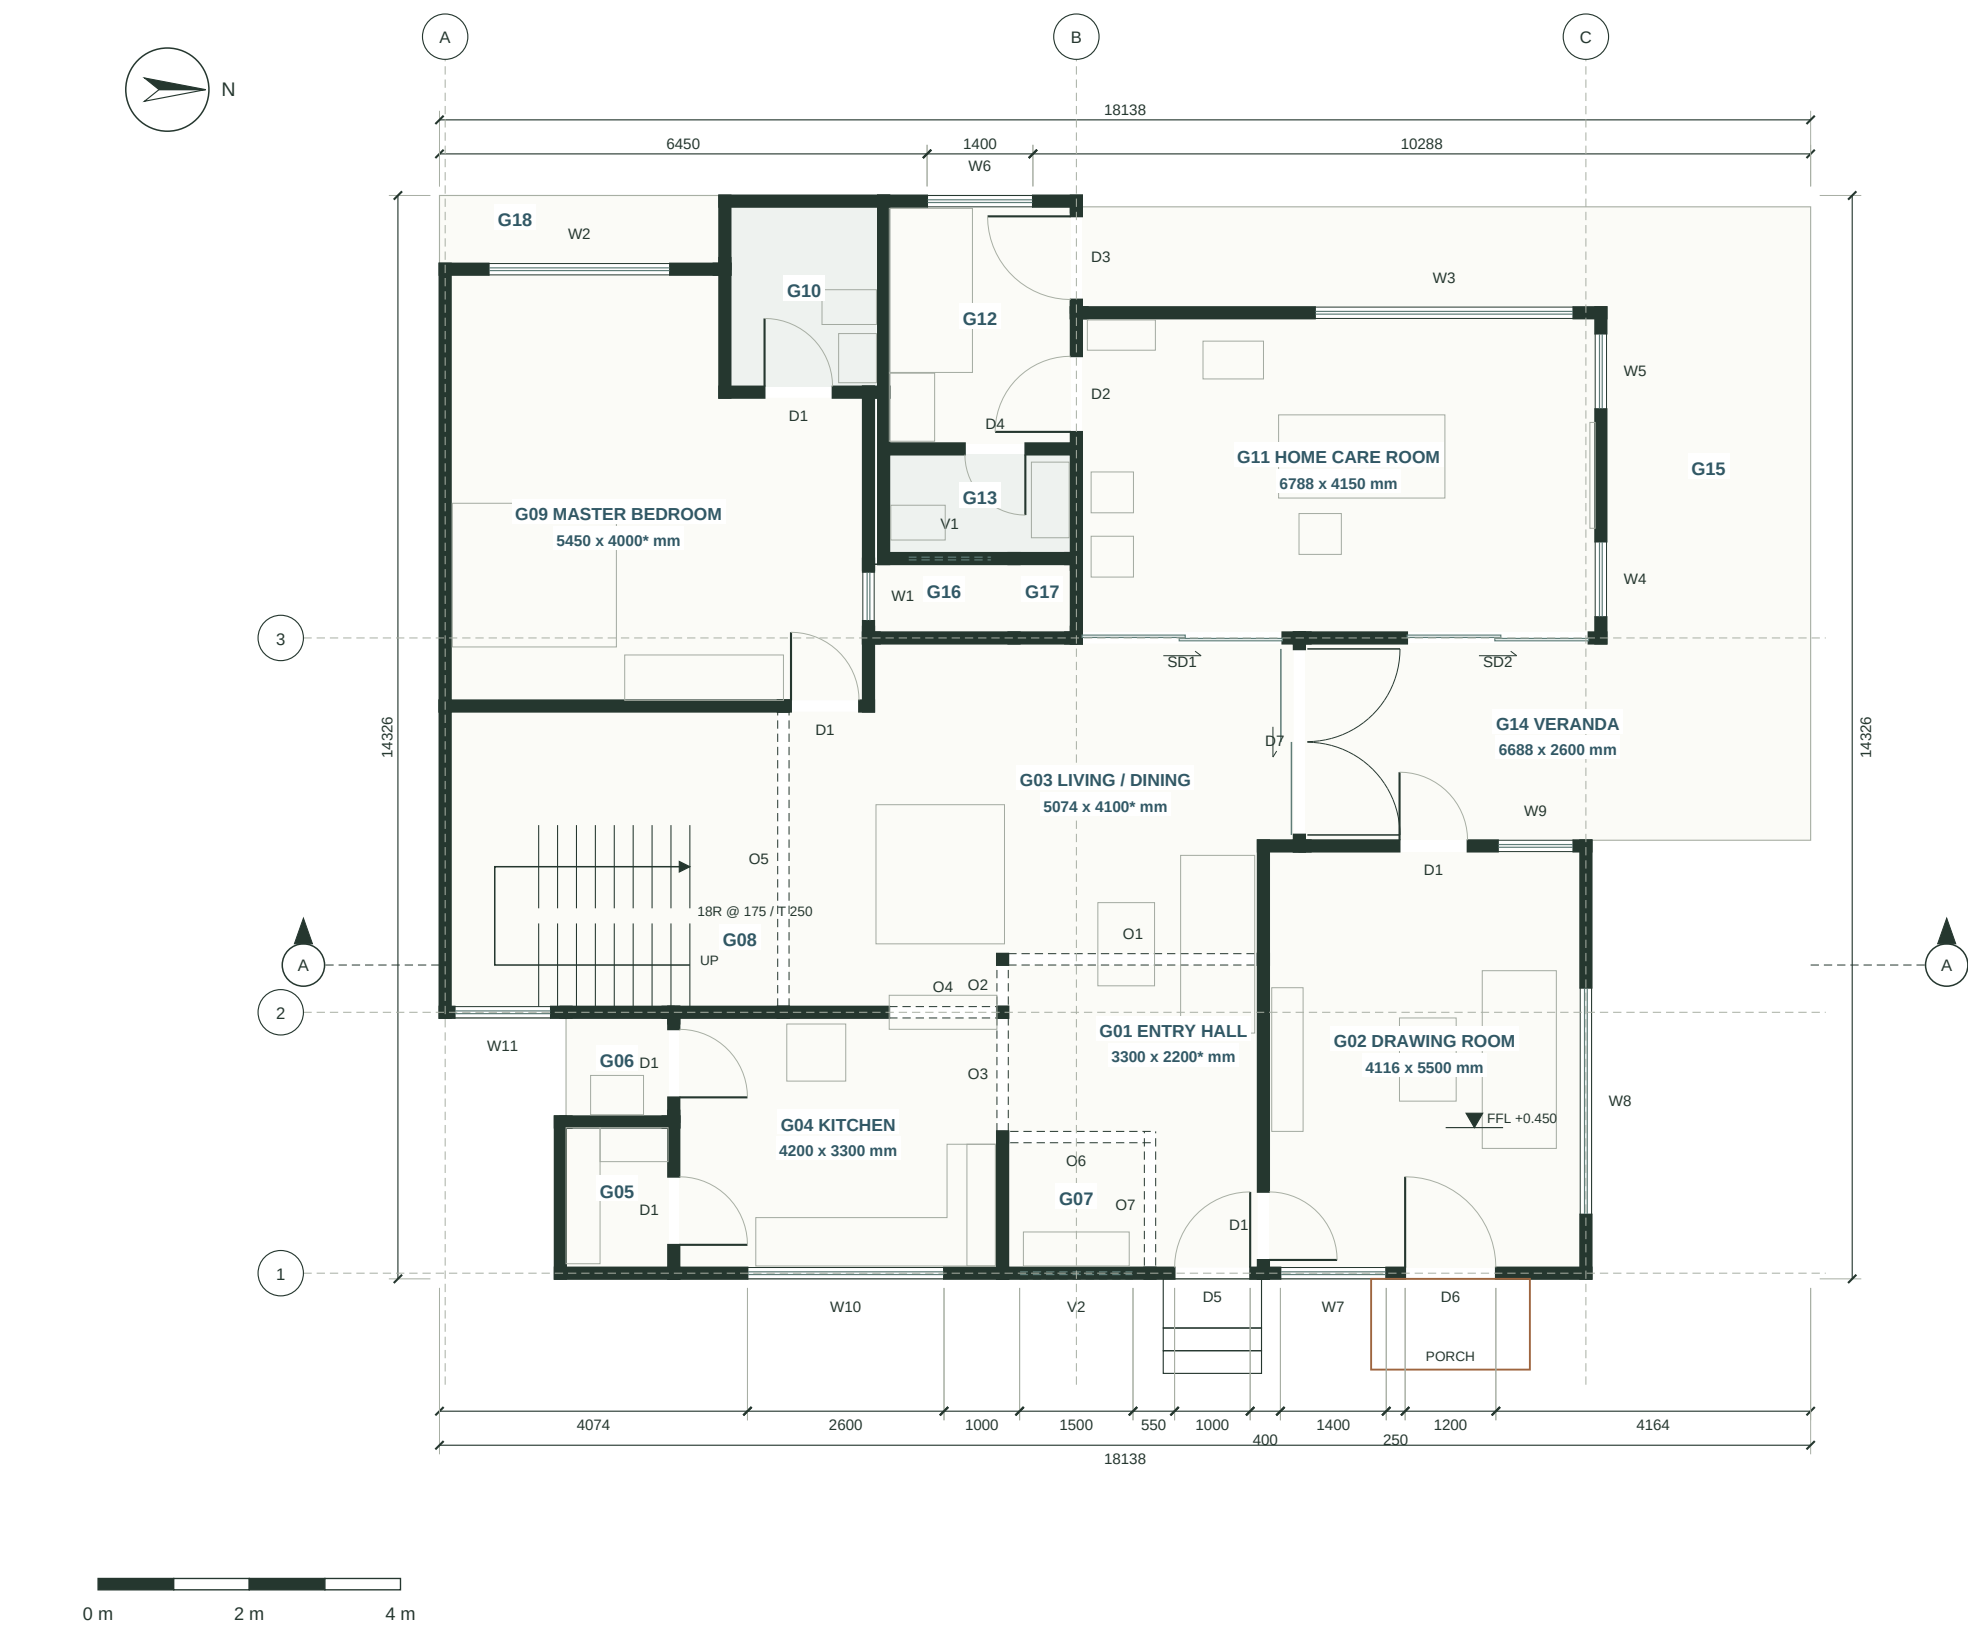

GROUND FLOOR KEY

REF / SPACE		AREA m2
G01	Entry Hall	9.69
G02	Drawing Room	22.64
G03	Living / Dining	27.57
G04	Kitchen	13.86
G05	Pantry	2.50
G06	Wash Area	1.75
G07	Puja	2.97
G08	Staircase	16.86
G09	Master Bedroom	27.57
G10	Attached Bath	4.63
G11	Home Care Room	28.17
G12	Caregiver Room	7.50
G13	Caregiver Wc	3.12
G14	Veranda	17.39
G15	Lawn / Garden Path	24.79
G16	Lightwell	1.67
G17	Covered Lightwell Edge	0.68
G18	Rear Ventilation Recess	3.33

READ THIS DRAWING

Dimensions in millimetres. Levels in metres relative to the assumed natural ground level (NGL).


* = principal clear rectangle within an irregular room; see A-601 for sizes and actual polygon areas.

D = door; SD = sliding glazing; O = open / cased opening; W = window; V = ventilator. See A-602.

Solid walls are cut at +1200 mm above the selected floor. Dashed windows sit above the cut plane.

Furniture is schematic. Grid bubbles A/B/C and 1/2/3 are coordination axes, not column locations.

Ground FFL +0.450 m. Timber door daylight and bathroom exhaust remain open review items.

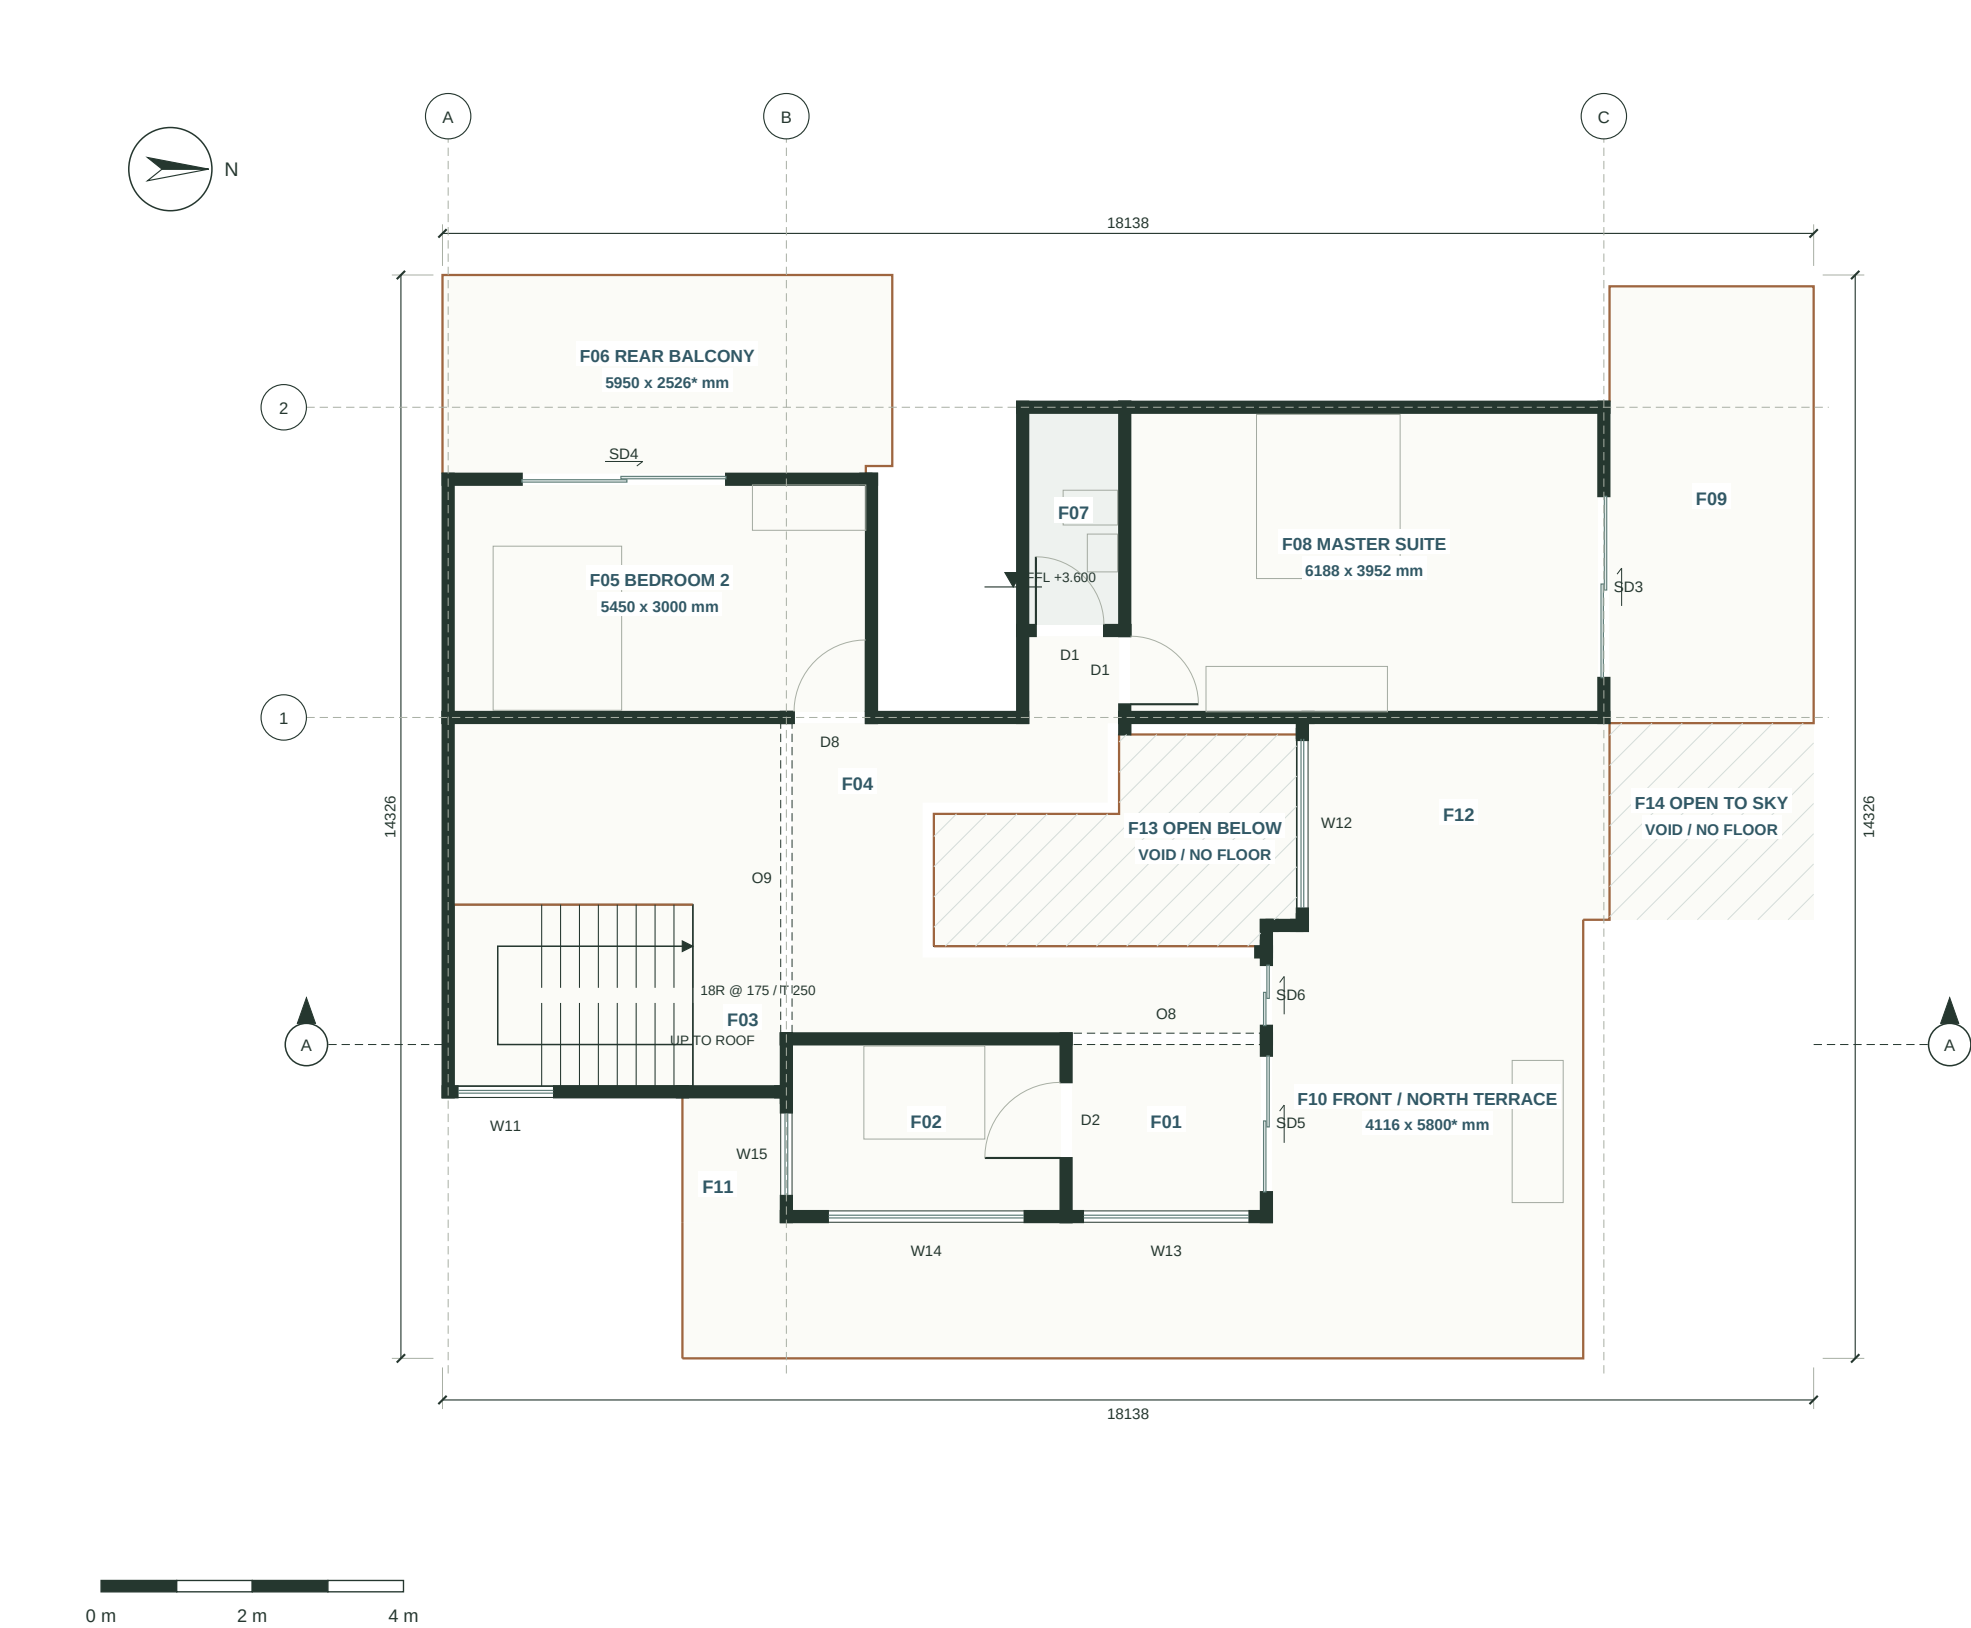

FIRST FLOOR KEY

REF / SPACE		AREA m2
F01	Arrival Lobby	5.50
F02	Studio / Office	7.81
F03	Staircase	20.76
F04	Overlooking Lobby	15.50
F05	Bedroom 2	16.35
F06	Rear Balcony	15.59
F07	Shared Bath	3.36
F08	Master Suite	24.45
F09	Garden Balcony	15.60
F10	Front / North Terrace	37.91
F11	Terrace Return	2.15
F12	Veranda Roof Terrace	10.37
F13	Open Below	10.70 v
F14	Open To Sky	7.02 v

READ THIS DRAWING

Dimensions in millimetres. Levels in metres relative to the assumed natural ground level (NGL).

* = principal clear rectangle within an irregular room; see A-601 for sizes and actual polygon areas.

D = door; SD = sliding glazing; O = open / cased opening; W = window; V = ventilator. See A-602.

Solid walls are cut at +1200 mm above the selected floor. Dashed windows sit above the cut plane.

Furniture is schematic. Grid bubbles A/B/C and 1/2/3 are coordination axes, not column locations.

First FFL +3.600 m. F13 is open below; F14 remains open to sky. Neither is usable floor area.




Section A-A through the south stair flight

OWNER / CIVIL ENGINEER HANDOVER

Section position is marked A on the plans. Model cut at local y = 4150 mm, along the rotated stair run.

REV A | 02 OCT 2026

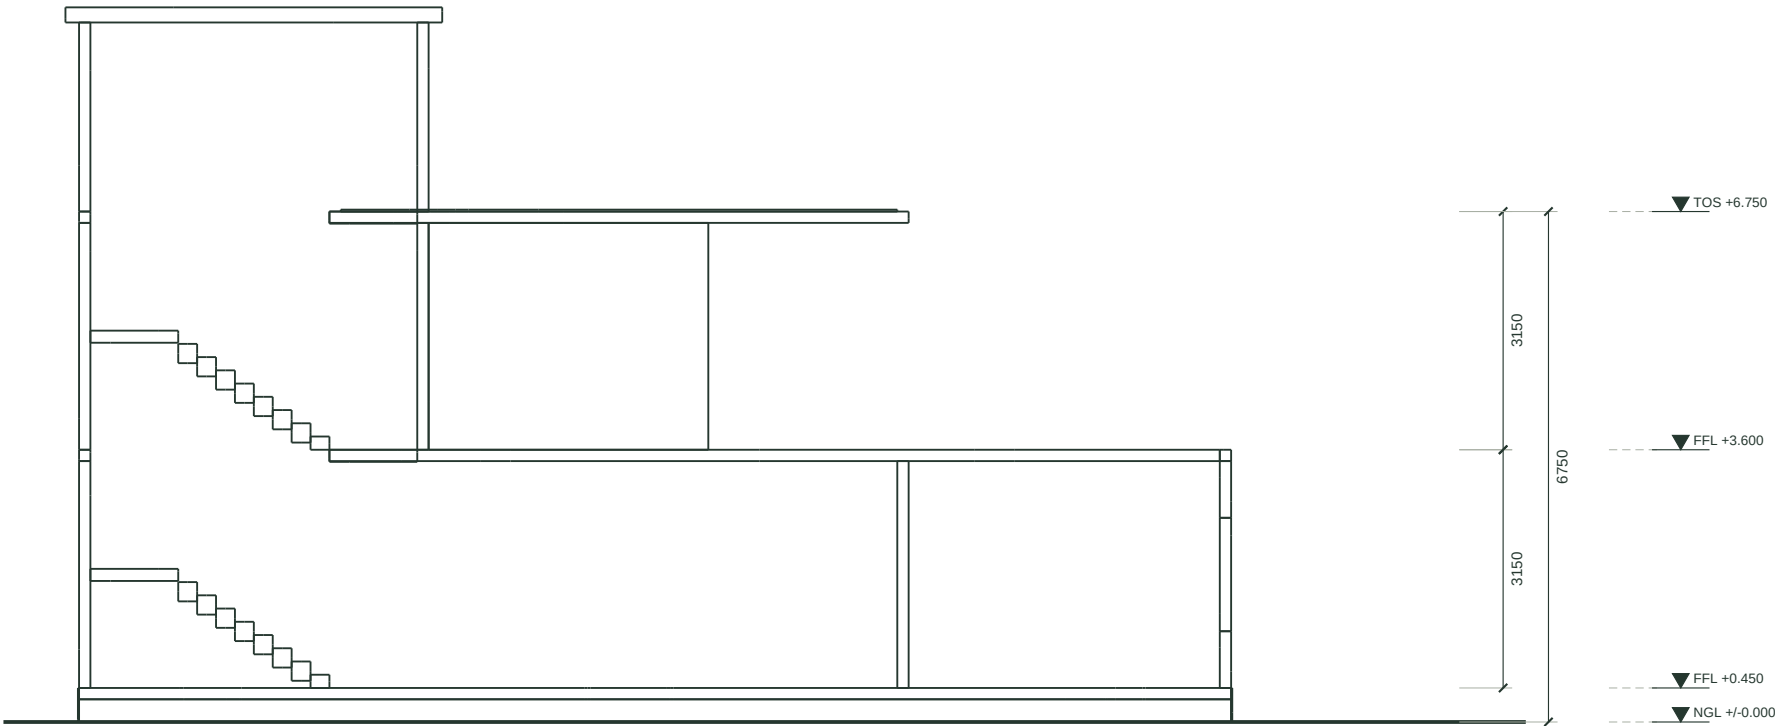

LEVELS / STAIR

Natural ground

+/-0.000 m, assumed

Ground finished floor

+0.450 m

First finished floor

+3.600 m

Roof slab datum

+6.750 m

Rise between floors

3150 mm

Each storey flight pair

18 risers at 175 mm

Tread / flight width

250 mm / 1100 mm

Turning landing

1162 mm nominal

SECTION SCOPE


The section intersects the saved wall, floor, stair, roof and plinth meshes. It documents the concept geometry. It does not provide RCC member sizes, reinforcement or foundations.

Stair headroom, handrails, guards, slab openings and the double-height edge need coordinated architectural and structural review.

How to use this sheet

Use it to discuss the stair route from the ground floor to the first floor and roof. The two linked stair cores stay aligned. Floor finish build-ups and structural slab thicknesses must be resolved by the engineer before setting levels on site.



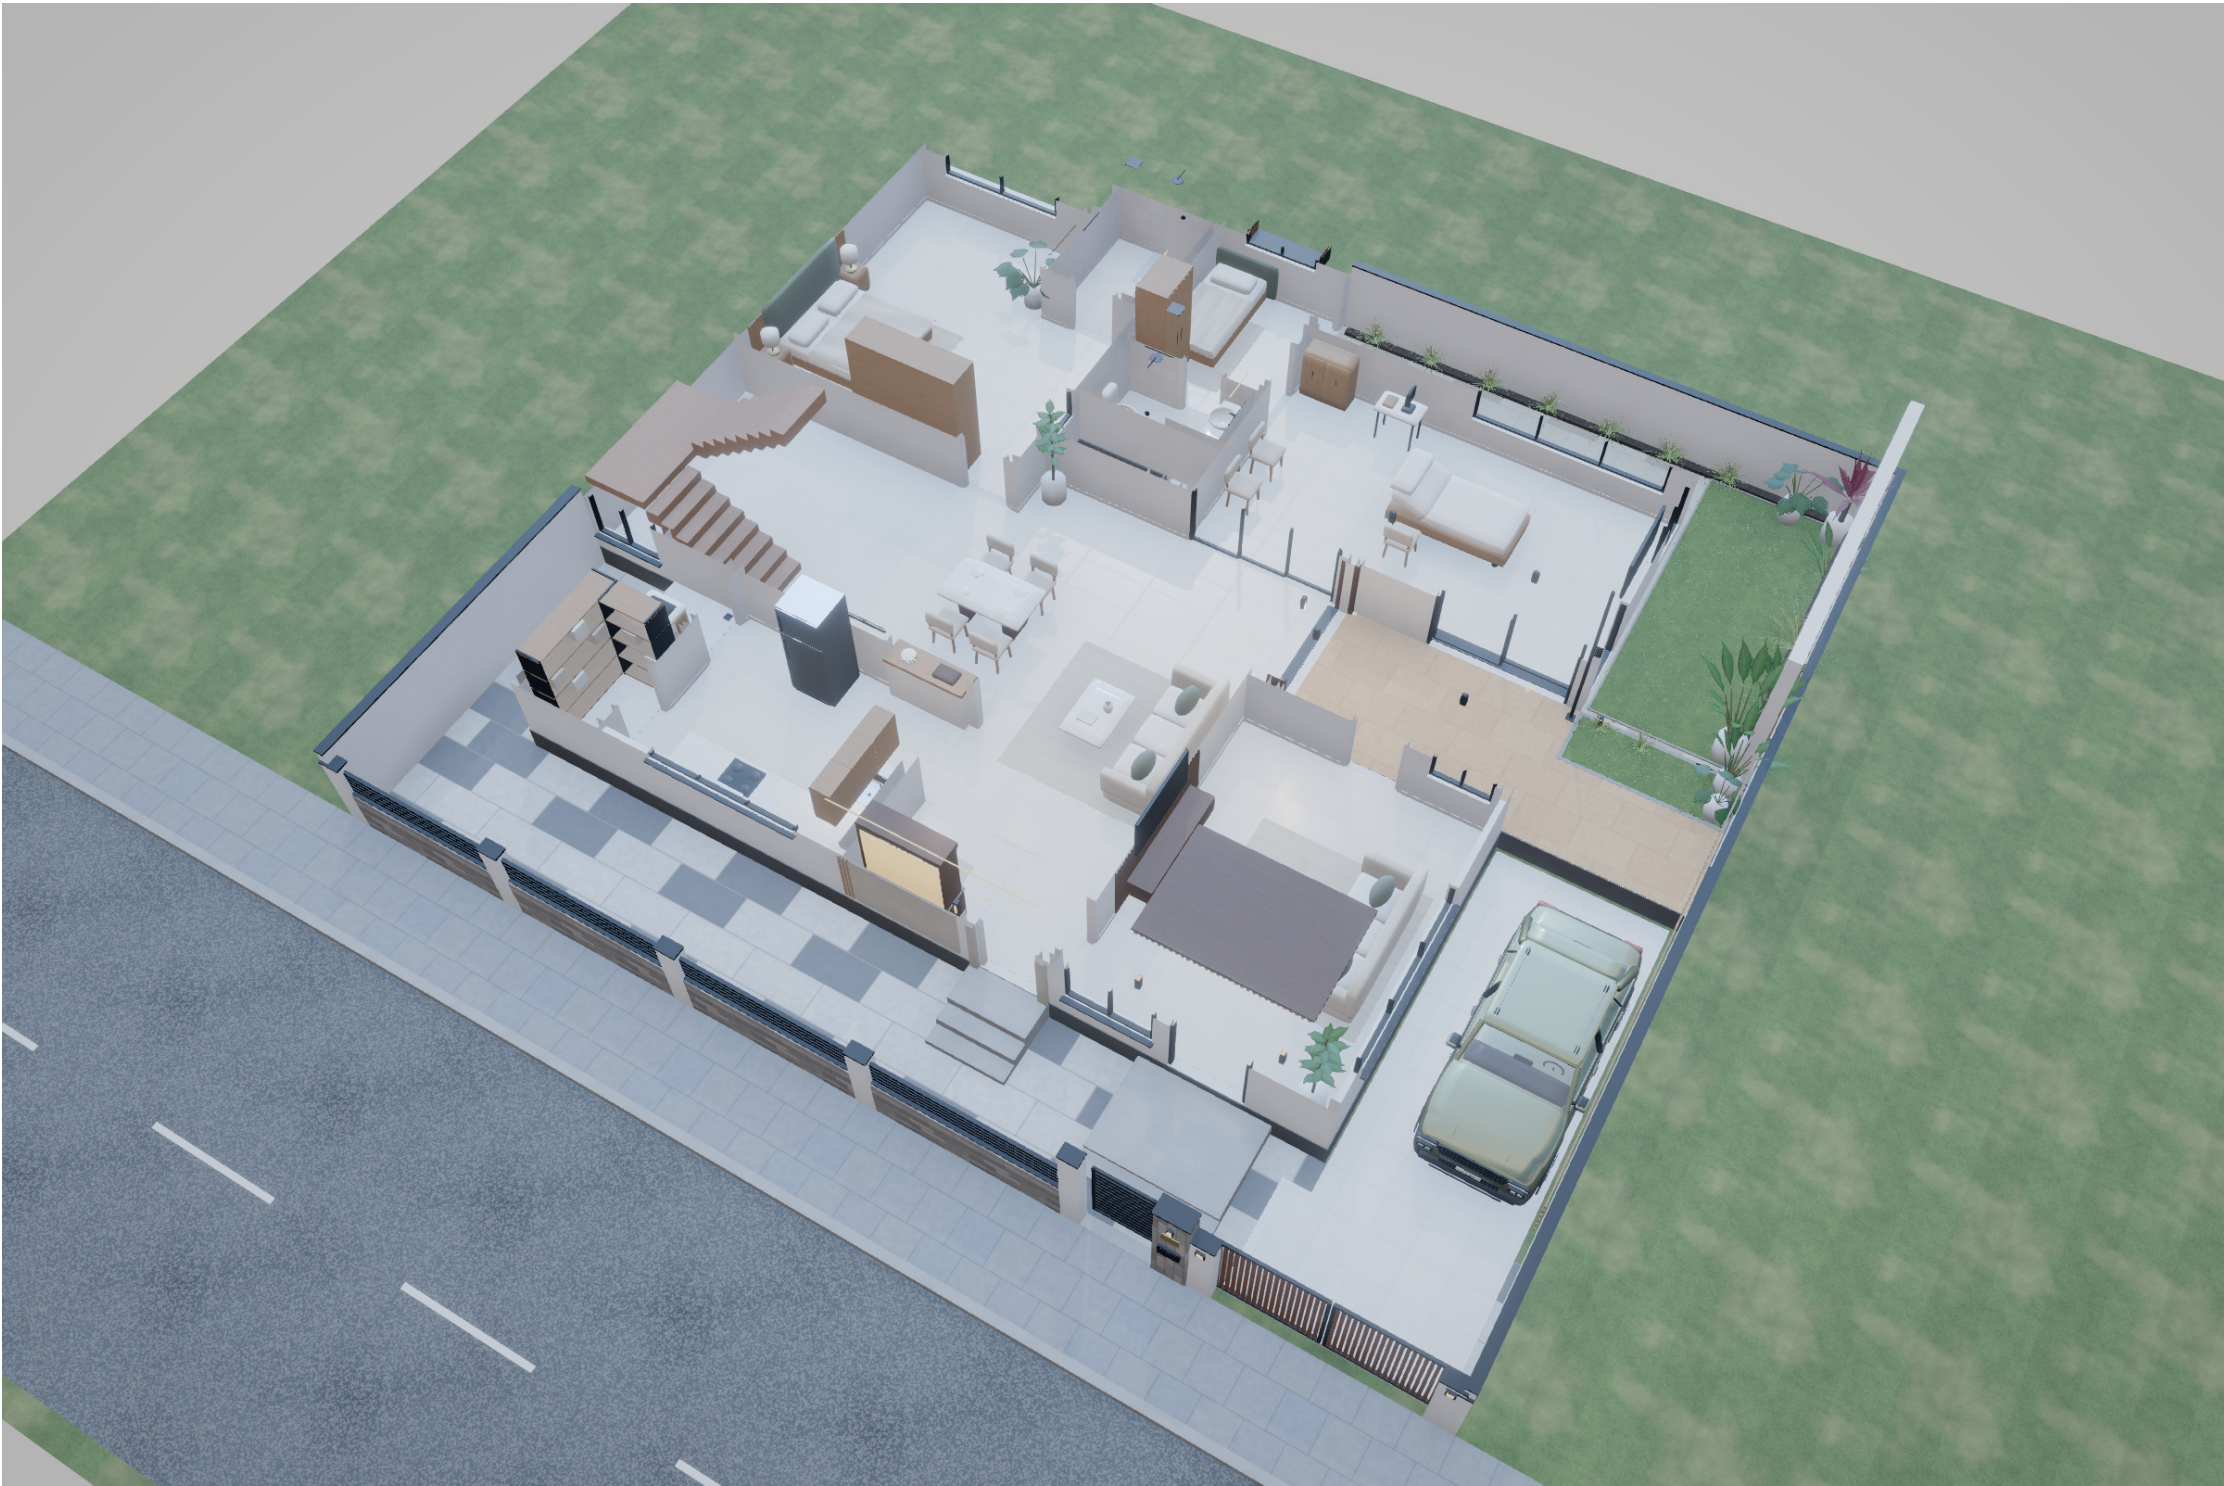

DESIGN TO DISCUSS

Arrival and privacy

Entry hall and separate drawing room retain independent front access.

Family zone

Kitchen, puja, dining, living and the south staircase share the main circulation.

Master bedroom

Southwest master bedroom has a private attached bathroom.

Care suite

Garden-facing care room connects to living, veranda and caregiver bedroom.

Independent caregiver route

Caregiver bedroom and attached toilet sit along the rear strip, with their own garden exit.

Outdoor space

Veranda opens toward the north lawn and garden path.

Use the 2D plans for dimensions. Furniture, materials, plants and car are presentation objects.



DESIGN TO DISCUSS

Private rooms

Two bedrooms occupy the rear of the first floor.

Arrival and work

The upper lobby and studio open toward the east terrace.

Double-height living

The guarded opening looks down to the ground-floor family living area.

Terraces

Front / north shared terraces remain distinct from the private bedroom balconies.


Daylight gap

The outer 2700 x 2600 mm sky opening remains unbuilt above the veranda edge.

Roof access

The retained staircase continues to the roof landing and guarded terrace.

Use the 2D plans for dimensions. Furniture, materials, plants and car are presentation objects.

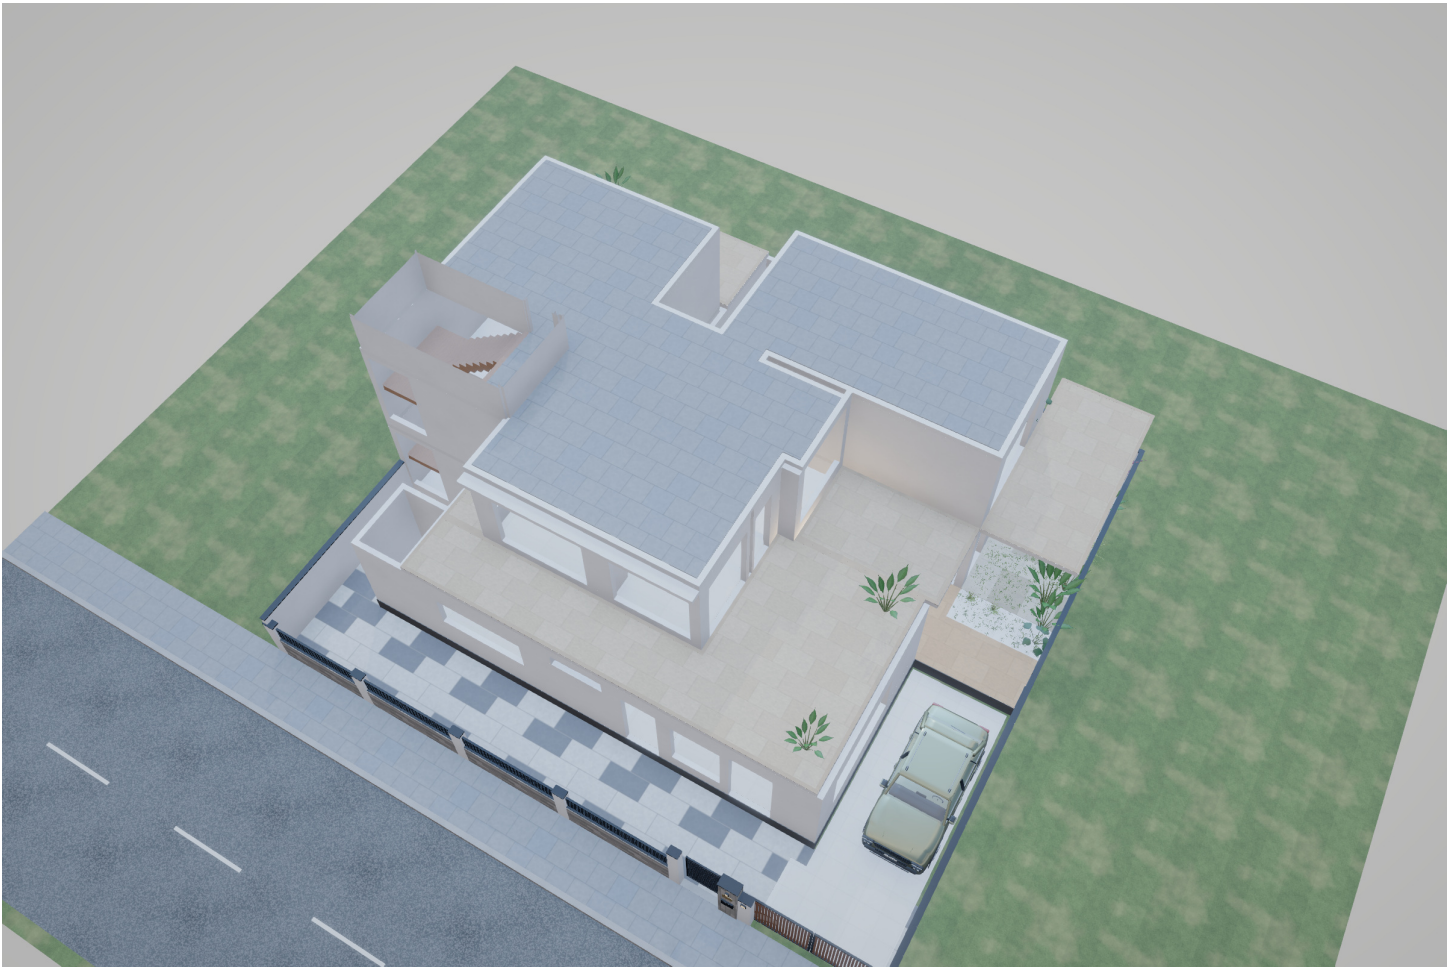

01 / Exterior massing

G+1 house, open terraces, private balconies and roof stair headhouse. Facade finishes and canopy supports are design studies requiring construction details.

02 / Roof access and terrace

The roof is accessed from the aligned south staircase. Terrace area is 106.049 m2 in the saved model. Guard geometry is visible; structural anchorage, falls, outlets and waterproofing remain to be designed.

GROUND FLOOR

REF	SPACE	CLEAR SIZE mm	APPROX. ft	AREA m2
G01	Entry Hall	3300 x 2200*	10.8 x 7.2	9.69
G02	Drawing Room	4116 x 5500	13.5 x 18.0	22.64
G03	Living / Dining	5074 x 4100*	16.6 x 13.5	27.57
G04	Kitchen	4200 x 3300	13.8 x 10.8	13.86
G05	Pantry	1350 x 1850	4.4 x 6.1	2.50
G06	Wash Area	1350 x 1300	4.4 x 4.3	1.75
G07	Puja	1800 x 1650	5.9 x 5.4	2.97
G08	Staircase	4324 x 3900	14.2 x 12.8	16.86
G09	Master Bedroom	5450 x 4000*	17.9 x 13.1	27.57
G10	Attached Bath	1950 x 2376	6.4 x 7.8	4.63
G11	Home Care Room	6788 x 4150	22.3 x 13.6	28.17
G12	Caregiver Room	2400 x 3126	7.9 x 10.3	7.50
G13	Caregiver Wc	2400 x 1300	7.9 x 4.3	3.12
G14	Veranda	6688 x 2600	21.9 x 8.5	17.39
G15	Lawn / Garden Path	2700 x 5776*	8.9 x 19.0	24.79
G16	Lightwell	1850 x 900	6.1 x 3.0	1.67
G17	Covered Lightwell Edge	750 x 900	2.5 x 3.0	0.68
G18	Rear Ventilation Recess	3700 x 900	12.1 x 3.0	3.33

FIRST FLOOR

REF	SPACE	CLEAR SIZE mm	APPROX. ft	AREA m2
F01	Arrival Lobby	2500 x 2200	8.2 x 7.2	5.50
F02	Studio / Office	3550 x 2200	11.6 x 7.2	7.81
F03	Staircase	4324 x 4800	14.2 x 15.7	20.76
F04	Overlooking Lobby	1726 x 4100*	5.7 x 13.5	15.50
F05	Bedroom 2	5450 x 3000	17.9 x 9.8	16.35
F06	Rear Balcony	5950 x 2526*	19.5 x 8.3	15.59
F07	Shared Bath	1200 x 2802	3.9 x 9.2	3.36
F08	Master Suite	6188 x 3952	20.3 x 13.0	24.45
F09	Garden Balcony	2700 x 5776	8.9 x 19.0	15.60
F10	Front / North Terrace	4116 x 5800*	13.5 x 19.0	37.91
F11	Terrace Return	1300 x 1650	4.3 x 5.4	2.15
F12	Veranda Roof Terrace	3988 x 2600	13.1 x 8.5	10.37
F13	Open Below	4324 x 1750*	14.2 x 5.7	10.70 v
F14	Open To Sky	2700 x 2600	8.9 x 8.5	7.02 v

ROOF LEVEL

R01	Roof Landing	2.789
R02	Roof Terrace	106.049

Roof landing is the clear arrival patch beside the stair well. Roof terrace is open access space, not another occupied storey.

* Irregular / L-shaped space: clear size is its largest inscribed rectangle; area is the actual clear polygon. v = void, excluded from usable floor area. Stair room areas include the circulation envelope. Dimensions are model values and must be checked against site measurements.

Type tags correspond to A-101, A-102 and A-104. Width / height / sill are in millimetres.

DOORS / PASSAGES

TAG	WIDTH	HEIGHT	SILL	QTY	LEVEL	TYPE
D1	900	2100	0	8	G/F	Hinged door
D2	1000	2100	0	2	G/F	Hinged door
D3	1100	2400	0	1	G	Hinged door
D4	800	2100	0	1	G	Hinged door
D5	1000	2400	0	1	G	Hinged door
D6	1200	2400	0	1	G	Entry door
D7	2600	2400	0	1	G	Timber / mesh assembly
D8	950	2100	0	1	F	Hinged door
D9	900	2150	0	1	R	Hinged door
SD1	2650	2400	0	1	G	Sliding glazing
SD2	2400	2400	0	1	G	Wall-stacking glazing
SD3	2400	2400	0	1	F	Sliding glazing
SD4	2700	2400	0	1	F	Sliding glazing
SD5	1800	2400	0	1	F	Sliding glazing
SD6	800	2400	0	1	F	Sliding glazing
O1	3300	3000	0	1	G	Cased / open passage
O2	850	3000	0	1	G	Cased / open passage
O3	1500	3000	0	1	G	Cased / open passage
O4	1425	2700	0	1	G	Cased / open passage
O5	3900	3000	0	1	G	Cased / open passage
O6	2100	3000	0	1	G	Cased / open passage
O7	1950	3000	0	1	G	Cased / open passage
O8	2800	3000	0	1	F	Cased / open passage
O9	4100	3000	0	1	F	Cased / open passage

SCHEDULE NOTES

These are nominal model opening sizes, not frame manufacturing sizes or guaranteed clear passage widths. Sill levels are above the respective finished floor. G = ground; F = first; R = roof landing. D/SD tags group by geometry; specialist timber/mesh and glass assemblies need their own detailing.

Confirm door handing, tracks, thresholds, ventilation performance and safety glazing with the engineer / supplier. No frame deductions, fabrication tolerances or glazing thickness specification is supplied.

WINDOWS / VENTS

TAG	WIDTH	HEIGHT	SILL	QTY	LEVEL	TYPE
W1	650	1700	650	1	G	Window glazing
W2	2400	1600	800	1	G	Window glazing
W3	3420	1700	600	1	G	Window glazing
W4	1000	2400	0	1	G	Fixed glazing
W5	1000	2100	300	1	G	Window glazing
W6	1400	1300	1000	1	G	Window glazing
W7	1400	1800	450	1	G	Window glazing
W8	3000	1500	750	1	G	Window glazing
W9	1000	1500	750	1	G	Window glazing
W10	2600	1100	1100	1	G	Window glazing
W11	1274	2500	350	2	G/F	Window glazing
W12	2250	2400	450	1	F	Window glazing
W13	2200	2100	300	1	F	Window glazing
W14	2600	2100	300	1	F	Window glazing
W15	1100	1500	750	1	F	Window glazing
V1	1100	800	1500	1	G	High-level vent / glazing
V2	1500	450	2200	1	G	High-level vent / glazing

01 / Site and local approvals

Survey all plot corners, road width, north direction and levels. Confirm the 60 x 55 ft plot and actual boundary position. The model assumes a 2438 mm front court with boundary-reaching side / rear wings; establish legal setbacks and permissible development before adoption.

02 / Structure and soil

Arrange the site and soil assessment needed for foundation design. Develop the structural system, columns, beams, slabs, load paths, balcony / canopy supports and reinforcement. The coordination grid on these plans is not a column or foundation layout.

03 / Double-height living and stairs

Resolve the F13 slab opening, guard anchorage and its interface with the living room below. Check the aligned staircase, 18 x 175 mm risers, 250 mm treads, 1100 mm flights, 1162 mm landing, headroom, handrails and slab-edge details.

04 / Daylight and exhaust

The saved review flags the living hall timber door: daylight is blocked when its timber leaves are closed. Review permanent glazing. Mechanical exhaust is selected for G10, G13 and F07; design duct routes, outlet positions and capacities.

05 / Water, drainage and terraces

Coordinate bathroom and kitchen water supply, soil / waste pipes, traps, drain routes and inspection access. Resolve roof and balcony falls, outlets, gutters, downpipes, waterproofing and level changes at thresholds.

06 / Care room and access

Confirm the care room brief, equipment clearances and circulation with the owner. The model is a residential care concept. Review entry steps, practical mobility access and door clear widths for the intended users.

07 / Wall and opening details

Model walls are 150 mm nominal. Confirm the wall system, lintels, damp-proofing, materials, facade anchors, frames, glass, timber / mesh assemblies, sliding tracks and tolerances. Furniture shown establishes intent and is schematic.

08 / Freeze a surveyed revision

Record agreed changes, issue coordinated architectural, structural and service drawings, and obtain the required professional and authority approvals. Use an approved revision for site setting-out and construction.

ENGINEER / OWNER REVIEW RECORD

Engineer / firm: _____ Owner: _____ Date: _____

Surveyed plot confirmed: _____ Revision requested: _____ Approval / drawing reference: _____