


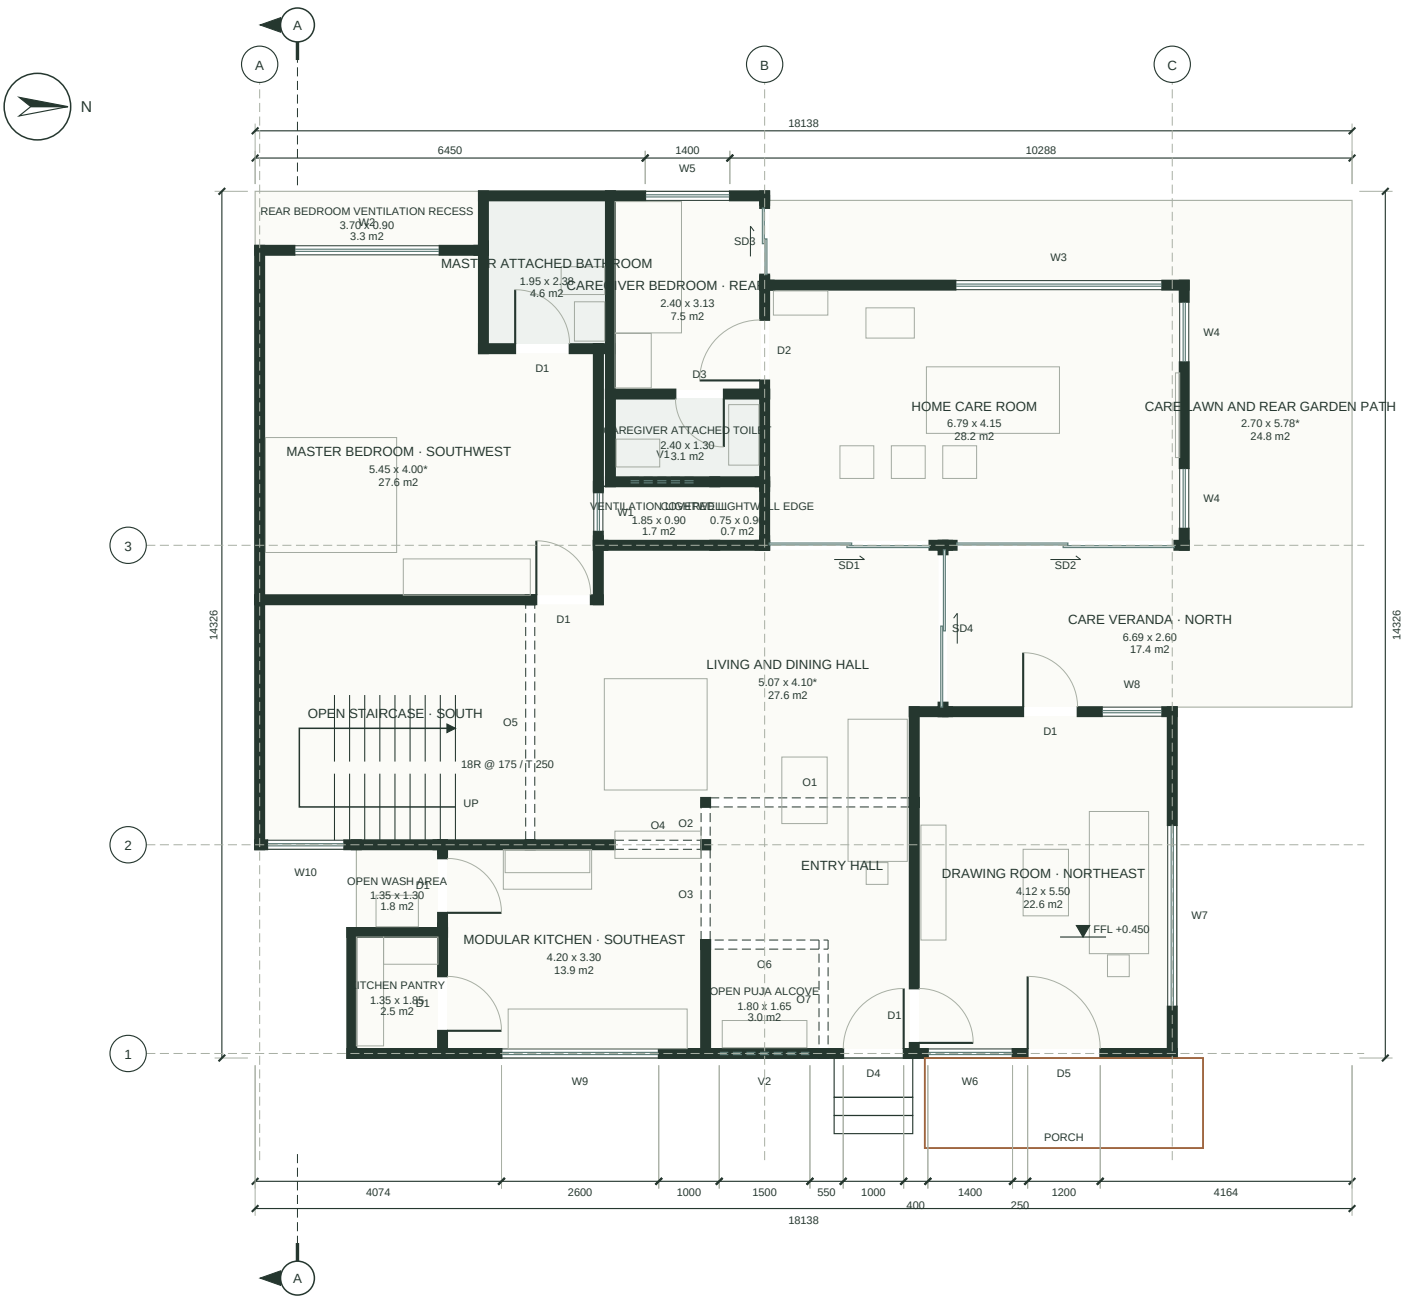

My Desired Home

| SPACE                          | CLEAR SIZE m | AREA m2 |
|--------------------------------|--------------|---------|
| Master attached bathroom       | 1.95 x 2.38  | 4.63    |
| Master bedroom · southwest     | 5.45 x 4.00* | 27.57   |
| Rear bedroom ventilation reces | 3.70 x 0.90  | 3.33    |
| Home care room                 | 6.79 x 4.15  | 28.17   |
| Ventilation lightwell          | 1.85 x 0.90  | 1.67    |
| Care lawn and rear garden path | 2.70 x 5.78* | 24.79   |
| Caregiver bedroom · rear strip | 2.40 x 3.13  | 7.50    |
| Caregiver attached toilet      | 2.40 x 1.30  | 3.12    |
| Covered lightwell edge         | 0.75 x 0.90  | 0.68    |
| Entry hall                     | 3.30 x 2.20* | 9.69    |
| Drawing room · northeast       | 4.12 x 5.50  | 22.64   |
| Modular kitchen · southeast    | 4.20 x 3.30  | 13.86   |
| Kitchen pantry                 | 1.35 x 1.85  | 2.50    |
| Living and dining hall         | 5.07 x 4.10* | 27.57   |
| Open puja alcove               | 1.80 x 1.65  | 2.97    |
| Care veranda · north           | 6.69 x 2.60  | 17.39   |
| Open wash area                 | 1.35 x 1.30  | 1.75    |

DRAWING NOTES

All dimensions in millimetres; levels in metres above natural ground level (NGL).

Room sizes are clear sizes between finished wall faces; \* marks the principal rectangle of an L-shaped room.


Dimension chains: openings, walls, overall. Tags: D door, SD sliding door, O cased opening, W window, V ventilator (see A-601).


Door leaves are drawn in the room they open into. Windows above the +1.2 m cut are dashed; furniture is schematic at true scale.

Grid bubbles are coordination axes only, not column positions. No certified IS 962 or local-code compliance is claimed.

SCALE 1:125 AT A3 / CUT +1200 mm

Dimensions govern; do not scale from a screen.

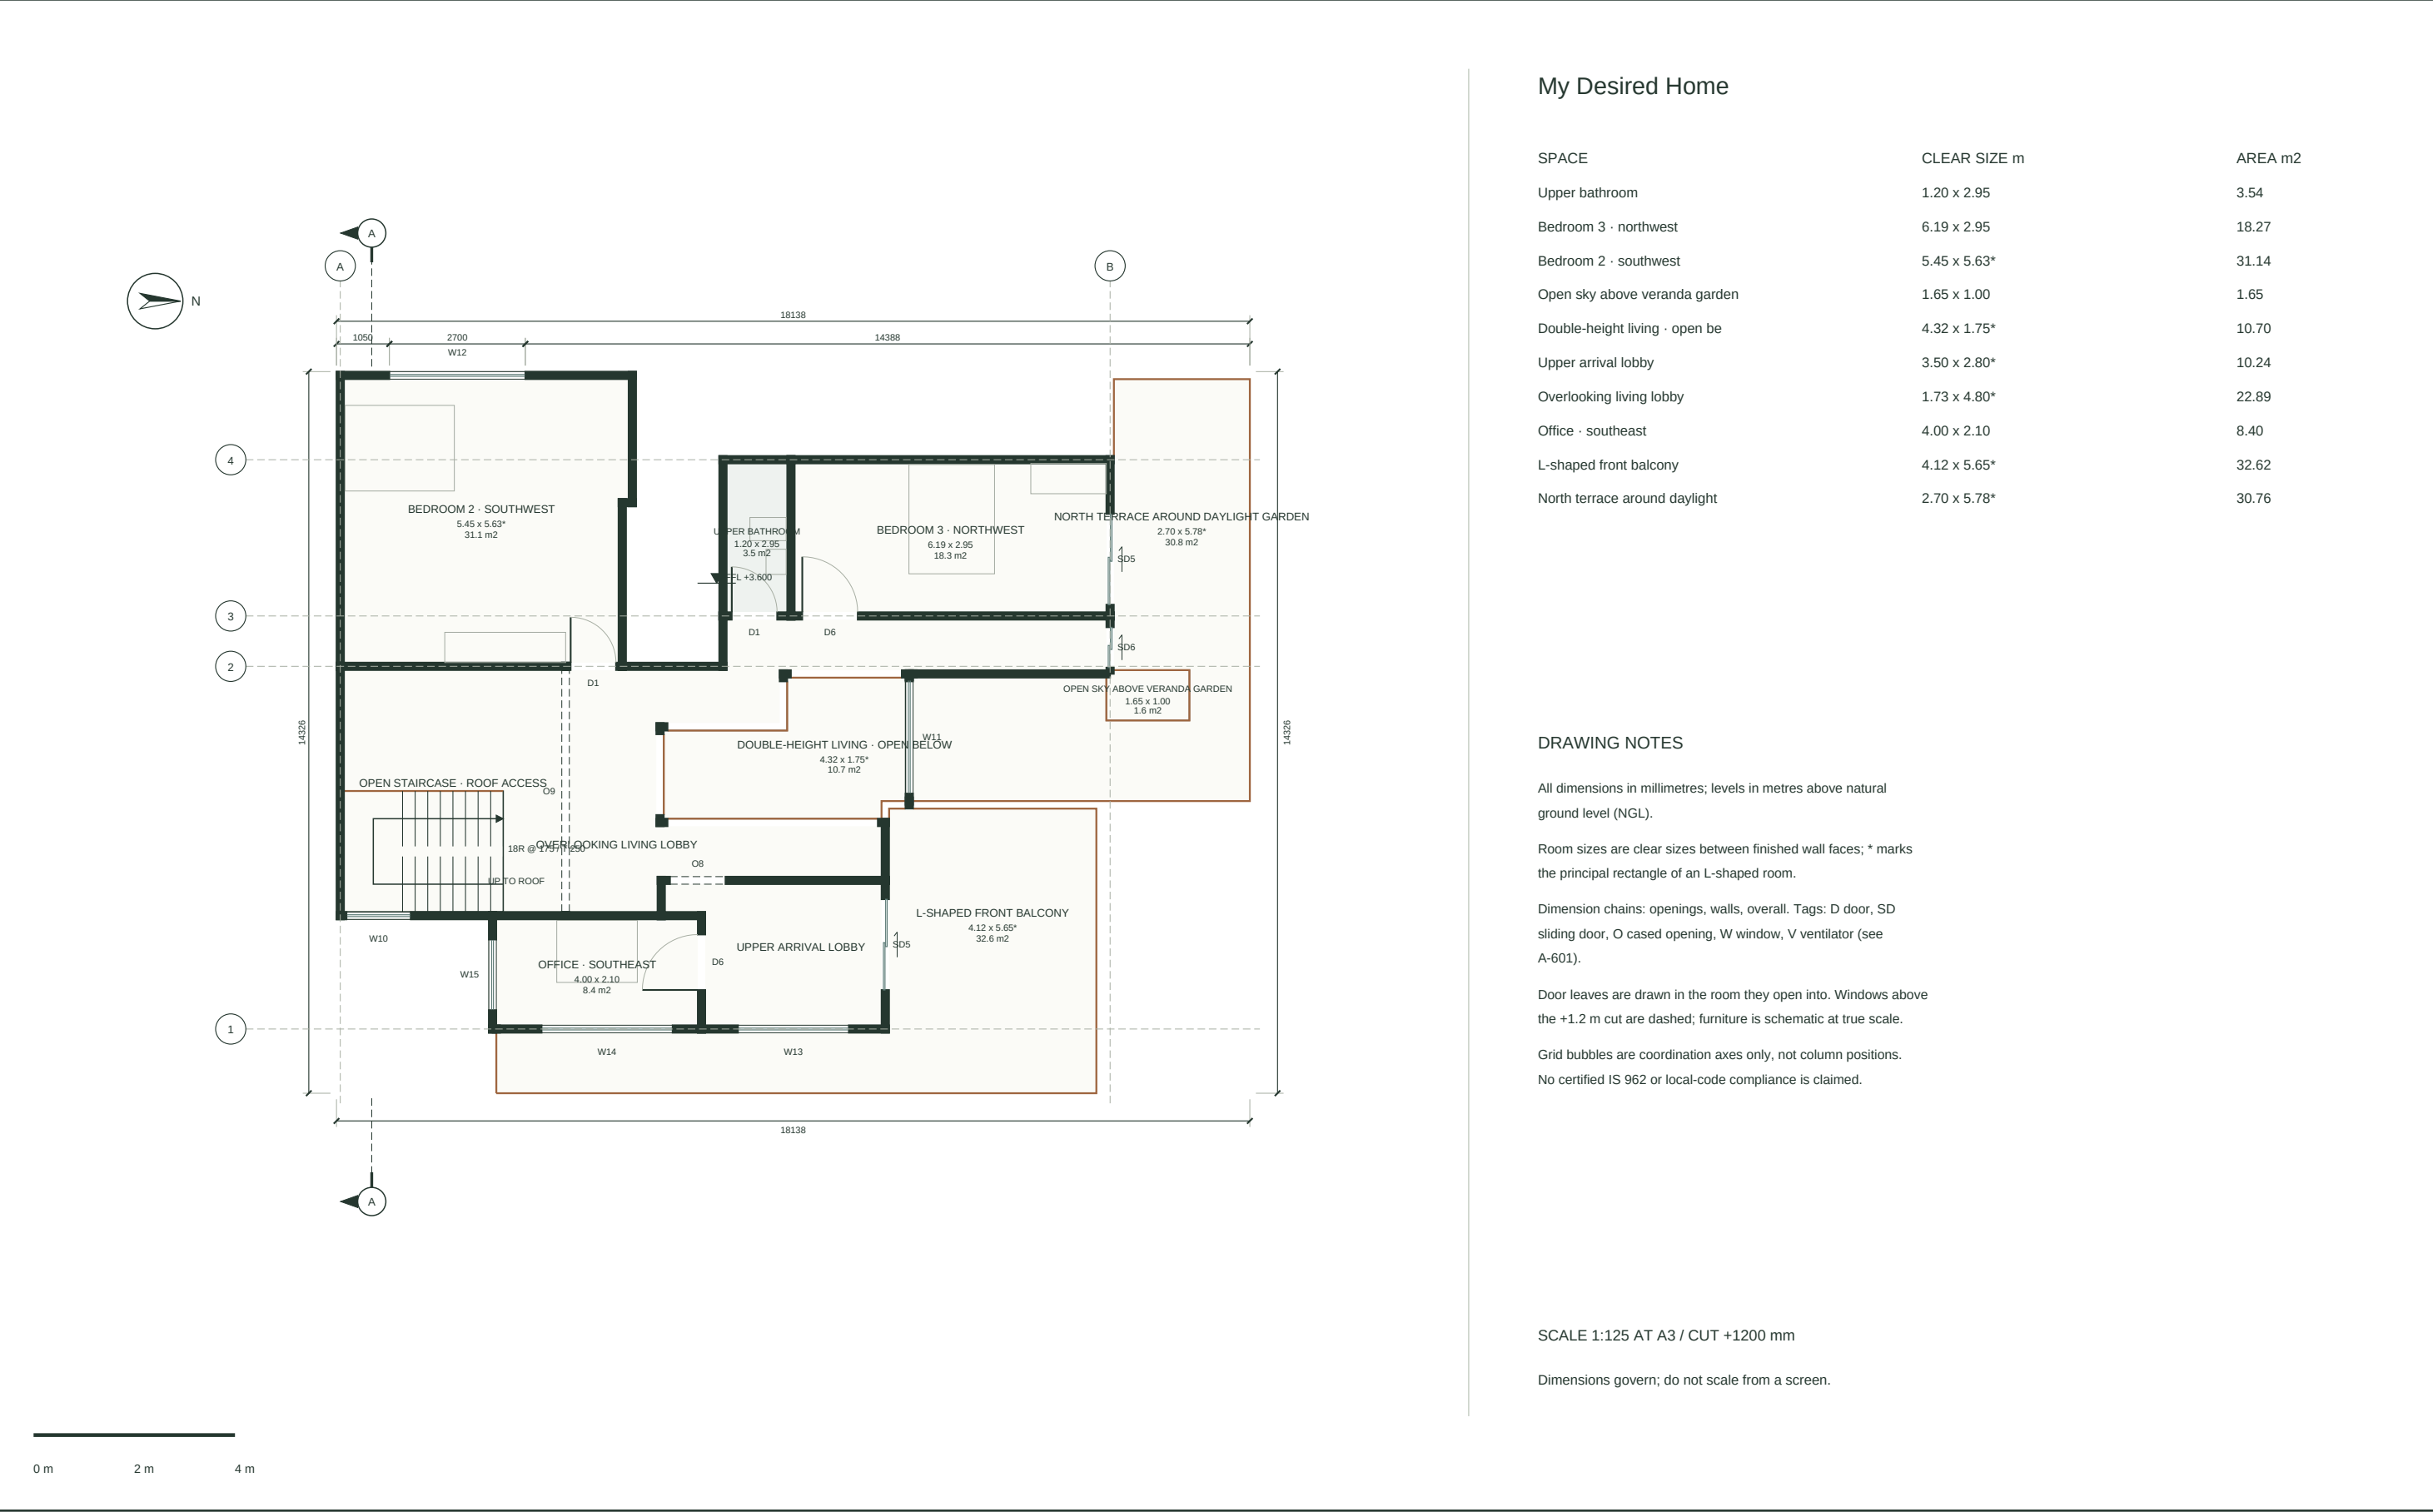

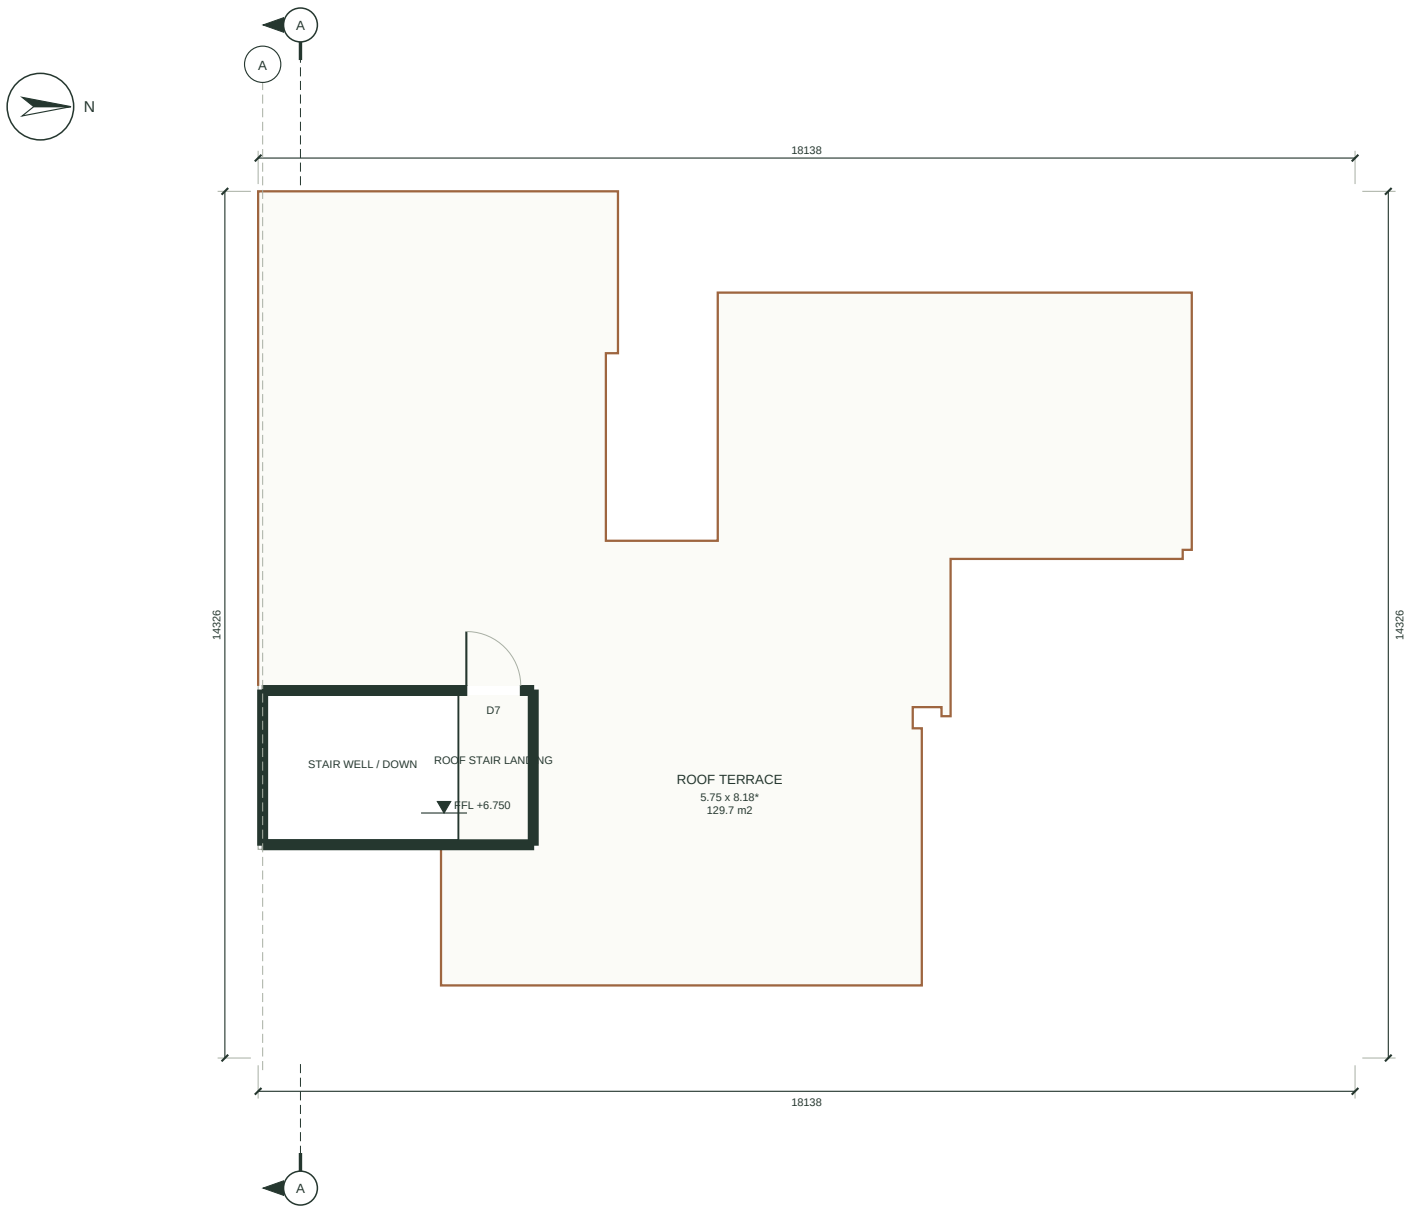

My Desired Home

| SPACE             | AREA m2 |
|-------------------|---------|
| Open roof terrace | 129.72  |

DRAWING NOTES


Roof access level, not an additional occupied storey.

Use the linked stair and its landing door to reach the guarded terrace.

Roof openings and headhouse positions follow the authored stair core.

SCALE 1:125 AT A3 / CUT +1200 mm

Dimensions govern; do not scale from a screen.

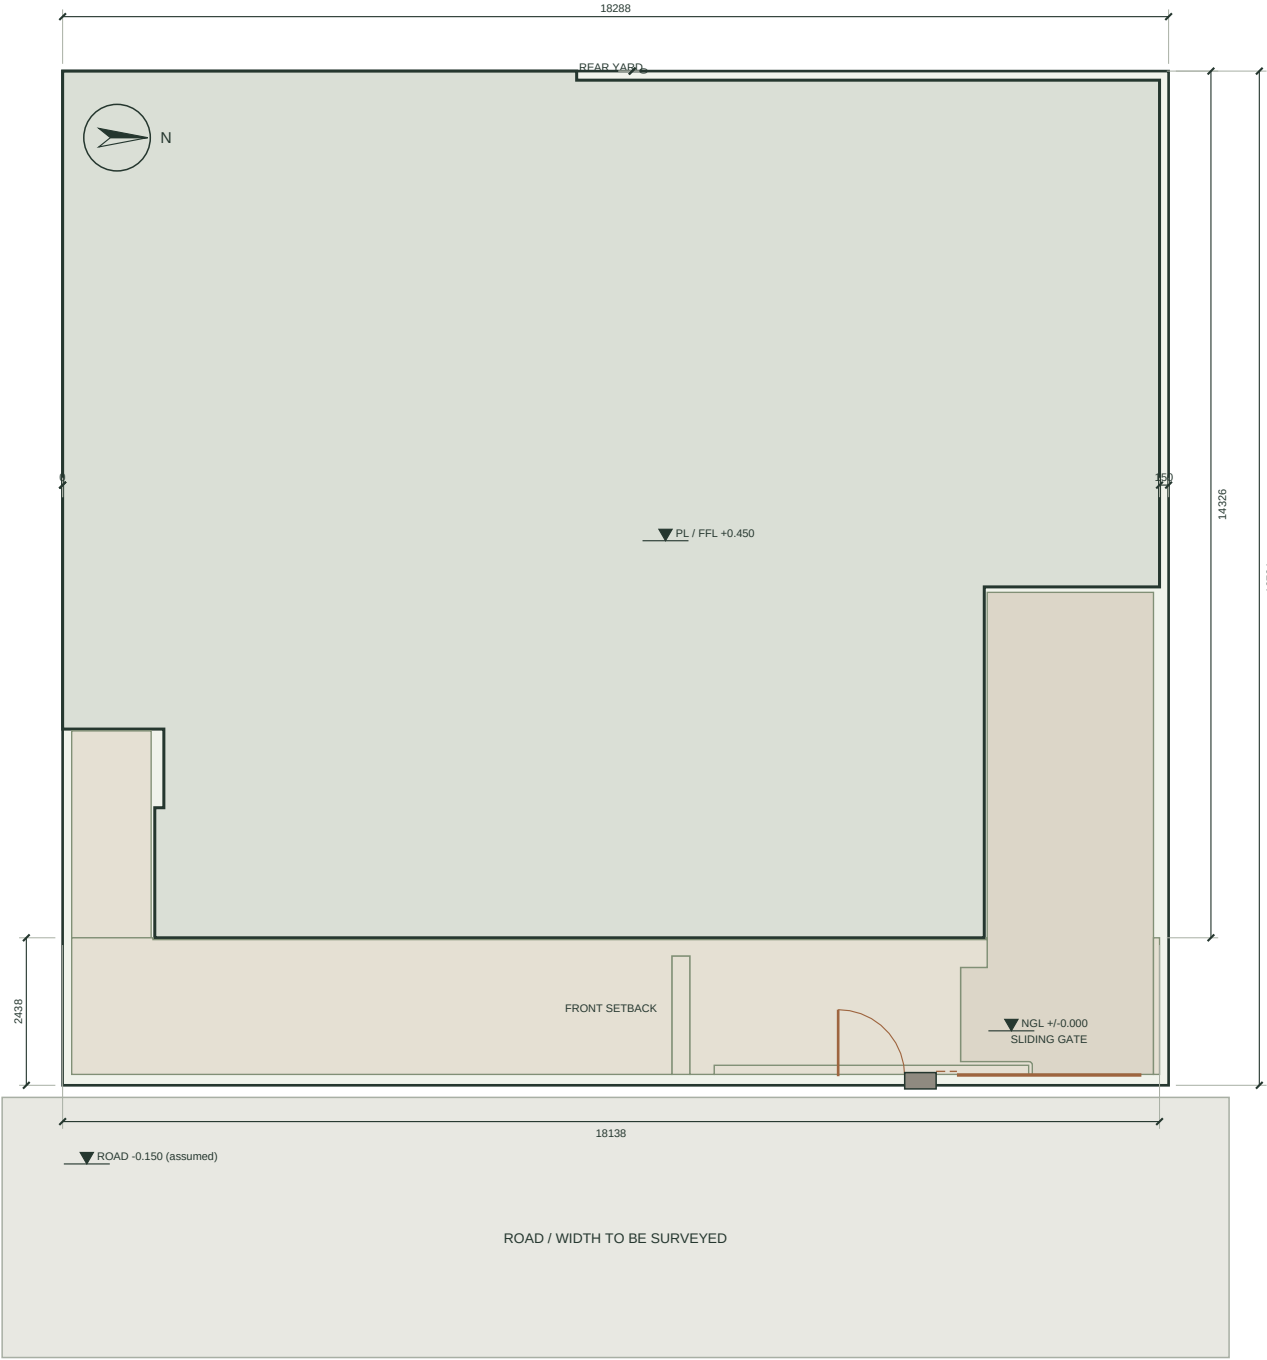

My Desired Home

| AREA STATEMENT | VALUE   | UNIT    |
|----------------|---------|---------|
| Plot           | 306.58  | m2      |
| Footprint      | 236.138 | m2      |
| Gross floors   | 423.319 | m2      |
| Coverage       | 77.02   | percent |
| Geometric FAR  | 1.381   | ratio   |


DRAWING NOTES

- Setbacks shown are design assumptions, not verified bylaws.
- Road width, property line and levels need a survey.
- No surveyed drainage fall or flood datum supplied.
- Default steps are not a step-free route.

SCALE 1:125 AT A3 / CUT +1200 mm

Dimensions govern; do not scale from a screen.

Front elevation

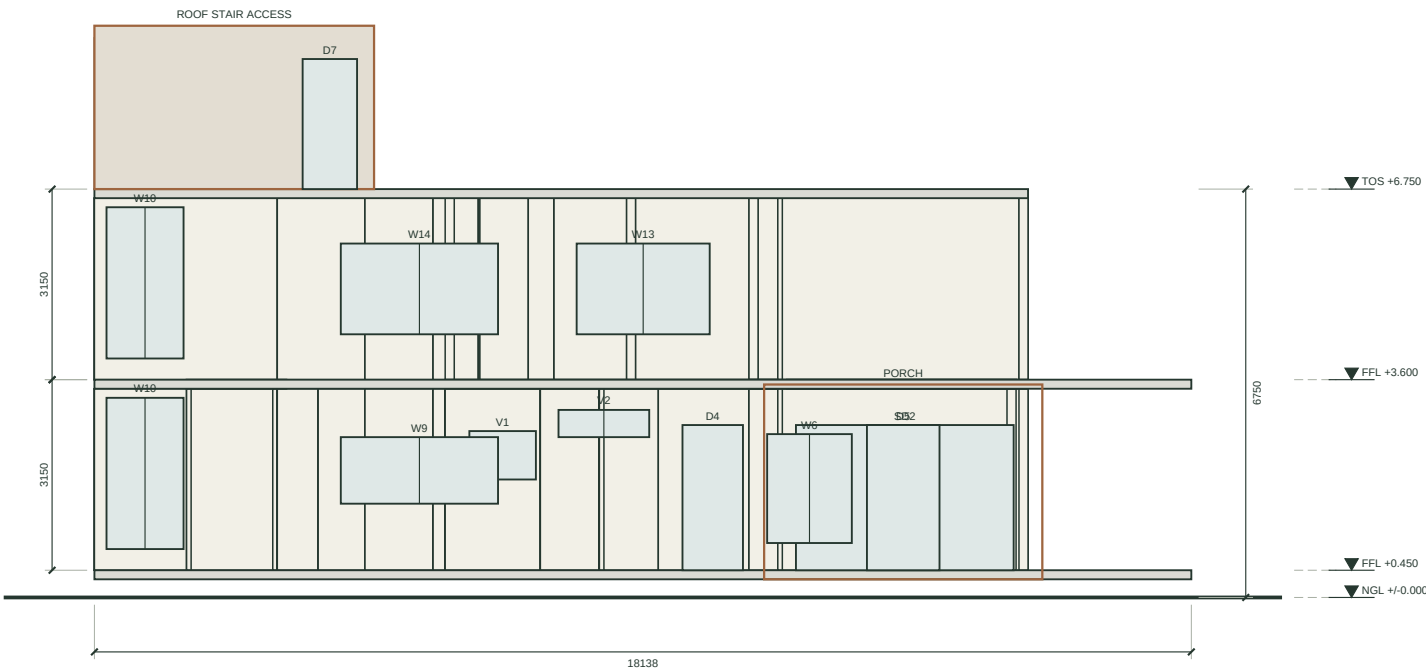

My Desired Home

DRAWING NOTES

Wall and opening heights derive from the building model; levels in metres above NGL.

This elevation records the primary wall plane.

Decorative facade accessories are coordinated in 3D, not fully detailed here.


No cladding anchors or construction joints are designed.

SCALE 1:125 AT A3 / CUT +1200 mm

Dimensions govern; do not scale from a screen.



Rear elevation

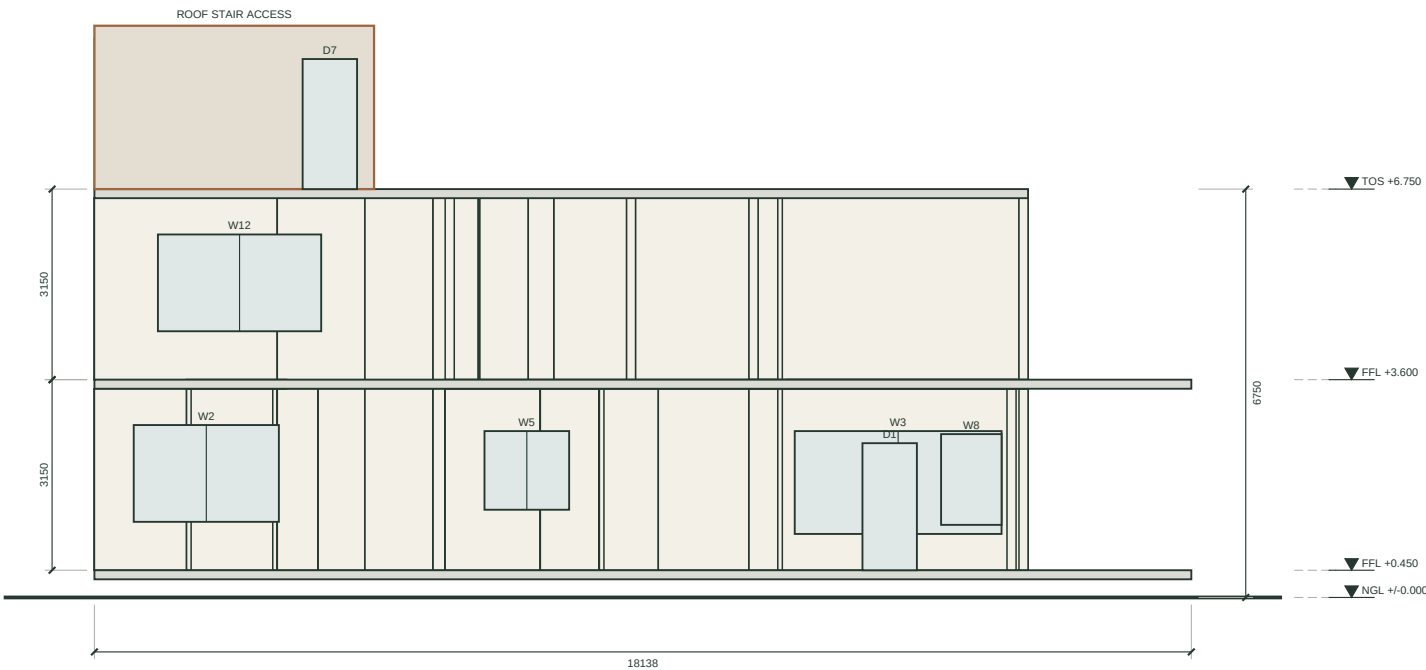

My Desired Home

DRAWING NOTES

Wall and opening heights derive from the building model; levels in metres above NGL.

This elevation records the primary wall plane.

Decorative facade accessories are coordinated in 3D, not fully detailed here.


No cladding anchors or construction joints are designed.

SCALE 1:125 AT A3 / CUT +1200 mm

Dimensions govern; do not scale from a screen.



Left elevation

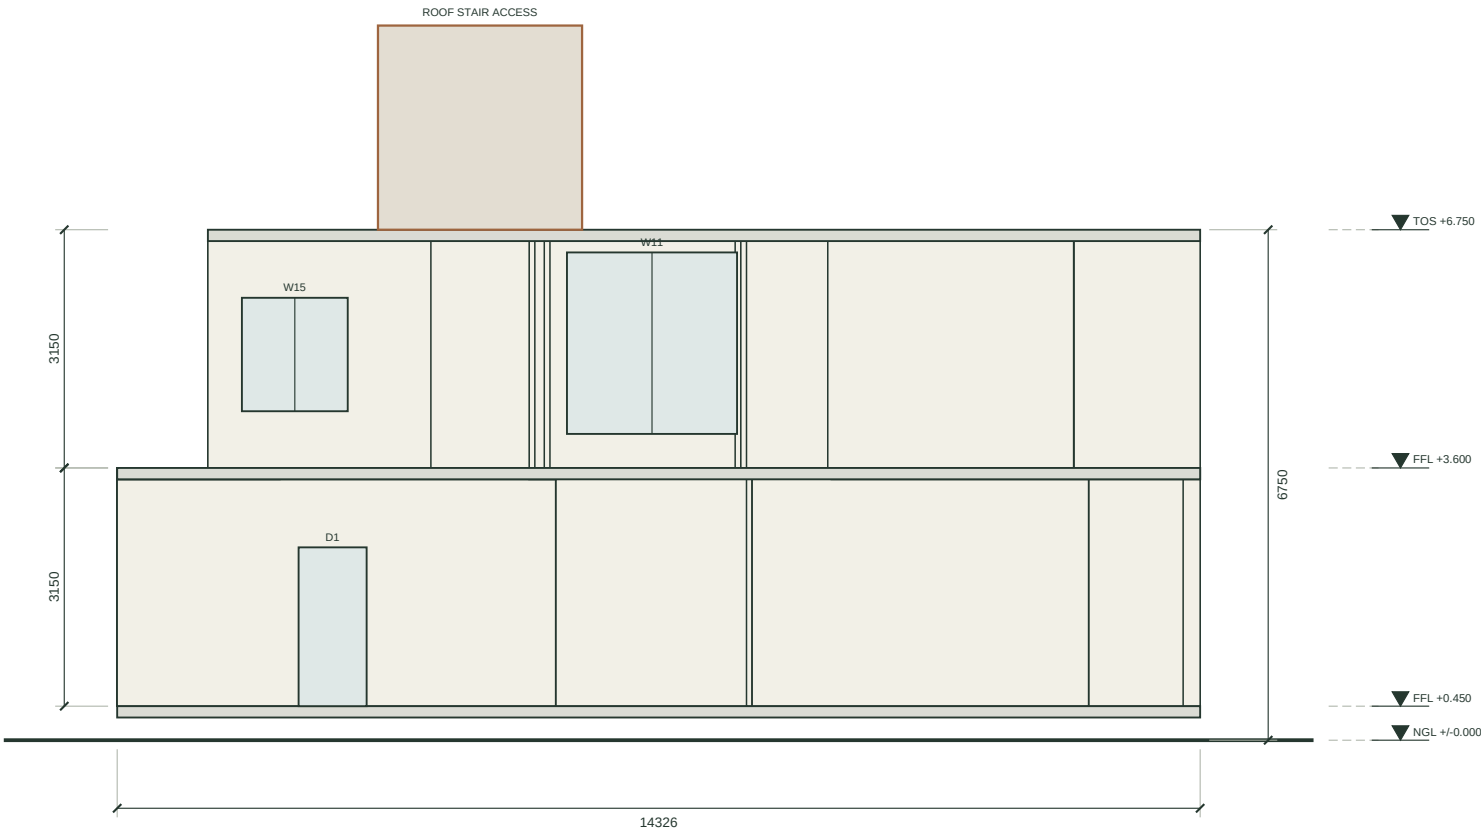

My Desired Home

DRAWING NOTES

Wall and opening heights derive from the building model; levels in metres above NGL.

This elevation records the primary wall plane.

Decorative facade accessories are coordinated in 3D, not fully detailed here.


No cladding anchors or construction joints are designed.

SCALE 1:100 AT A3 / CUT +1200 mm

Dimensions govern; do not scale from a screen.



Right elevation

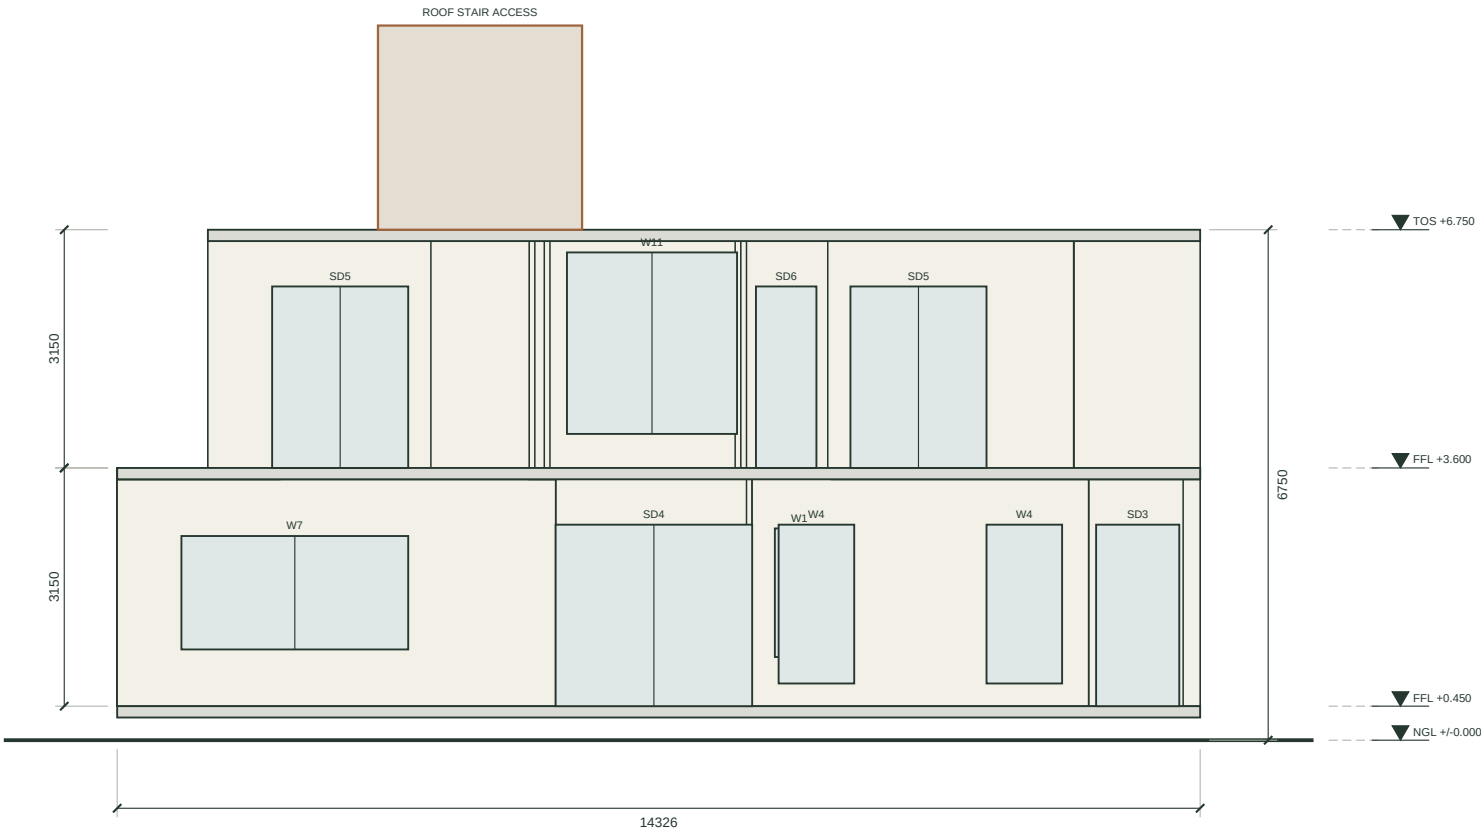

My Desired Home

DRAWING NOTES

Wall and opening heights derive from the building model; levels in metres above NGL.

This elevation records the primary wall plane.

Decorative facade accessories are coordinated in 3D, not fully detailed here.


No cladding anchors or construction joints are designed.

SCALE 1:100 AT A3 / CUT +1200 mm

Dimensions govern; do not scale from a screen.



Section A-A / x = 0.70 m

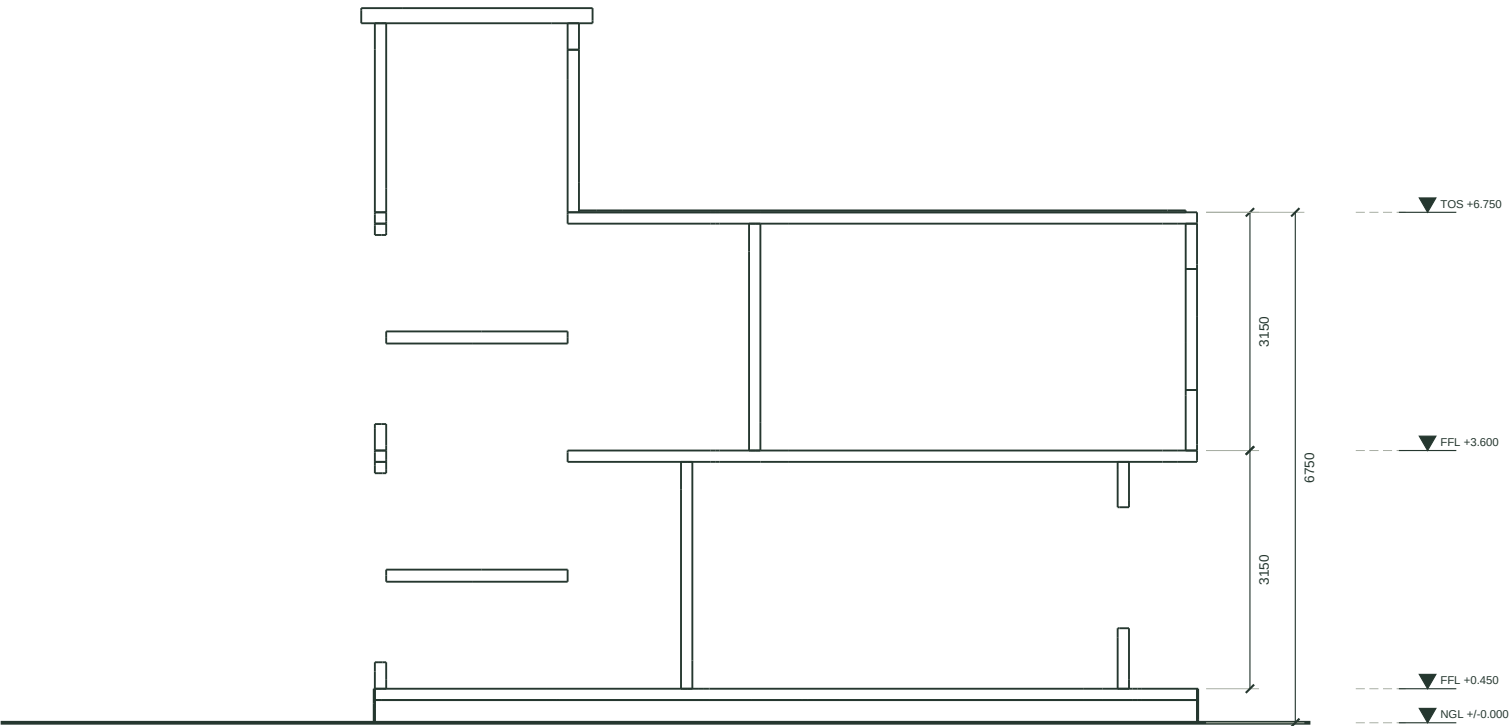

My Desired Home


DRAWING NOTES

- Actual mesh-plane intersections, not a generic stair illustration.
- Cut objects: walls, floor slabs, roof, stair and plinth. Levels in metres above NGL.
- No reinforcement or foundation design is represented.
- Stair headroom and handrails require a separate professional check.

SCALE 1:100 AT A3 / CUT +1200 mm

Dimensions govern; do not scale from a screen.



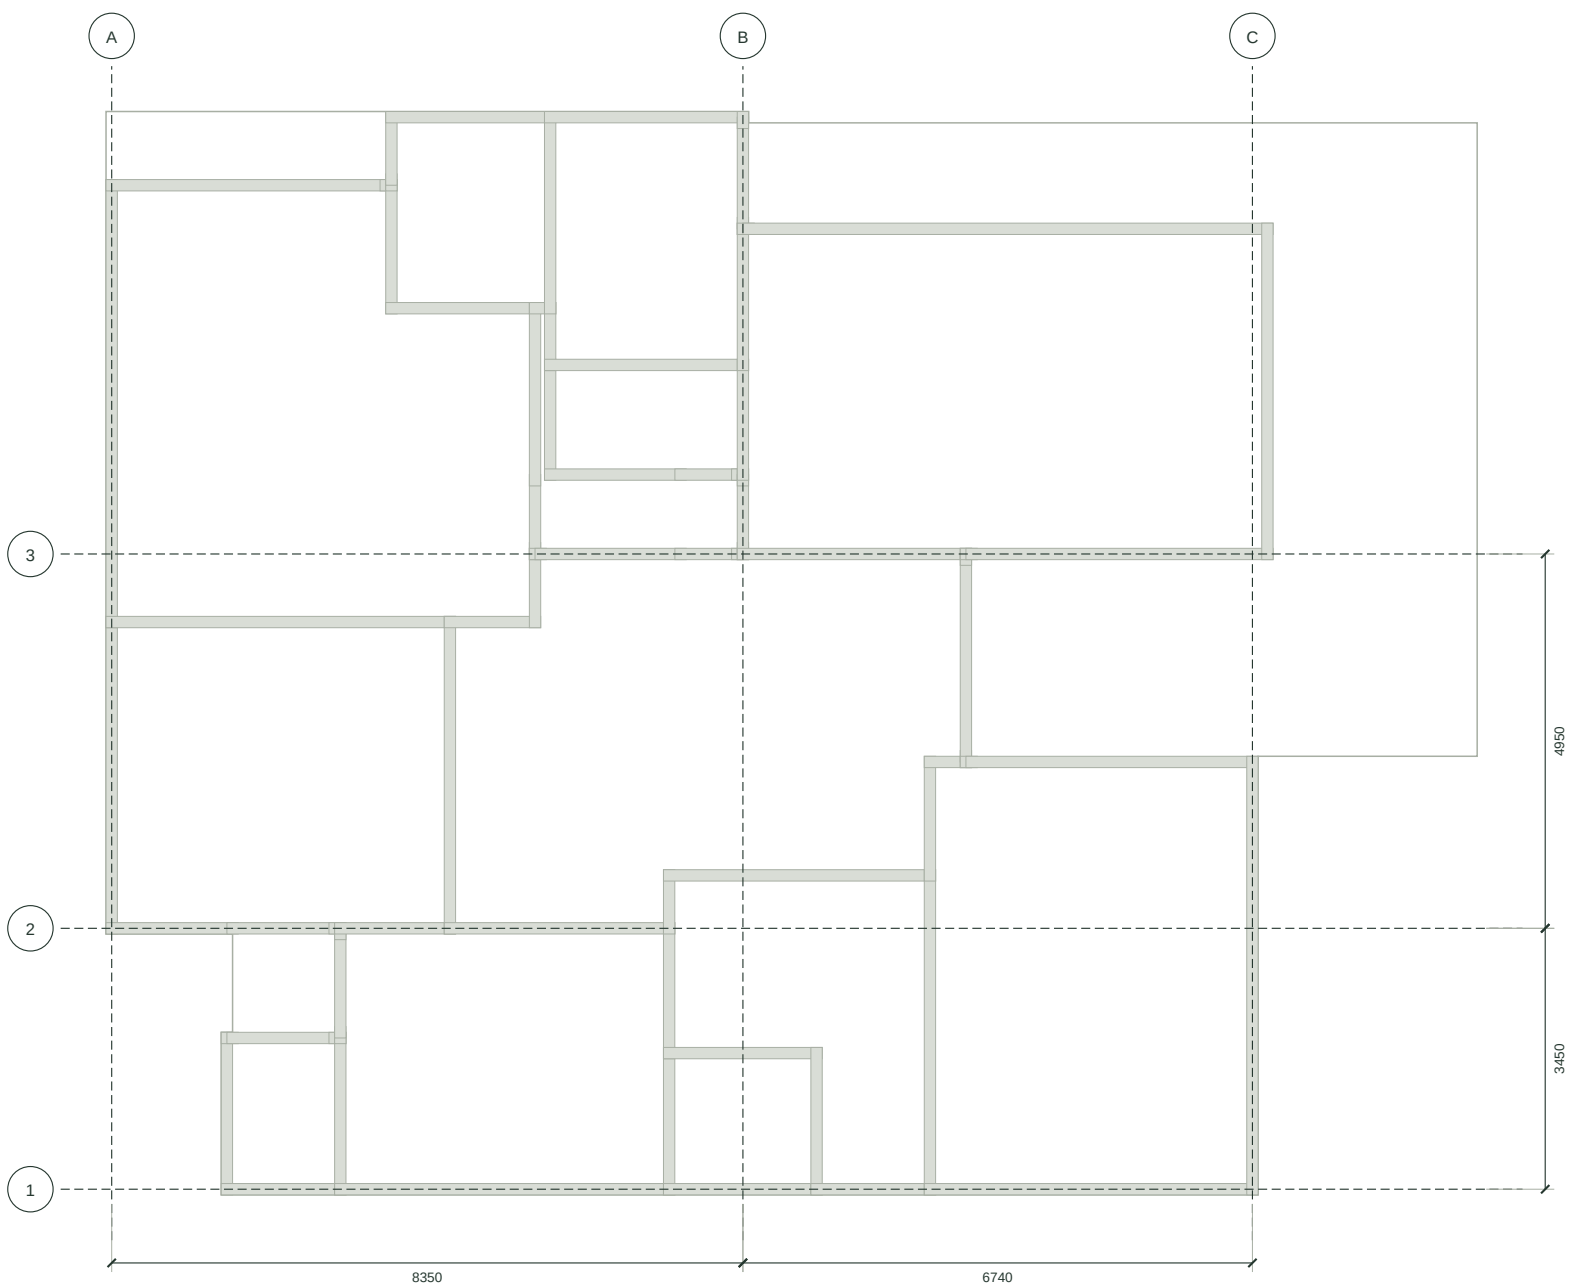

My Desired Home

DRAWING NOTES

Axes follow the outer walls and the long interior walls; they are NOT column locations.

No column, beam, slab or footing is sized or certified.

Engineer must establish an actual load path and lateral system.

No soil-bearing capacity is inferred from a soil photograph.

SCALE 1:100 AT A3 / CUT +1200 mm

Dimensions govern; do not scale from a screen.

FLOORFORGE / REVIEW / SCOPE

|               |                           |
|---------------|---------------------------|
| Geometry      | preliminary_geometry_pass |
| Regulatory    | NOT EVALUATED             |
| Structure     | NOT DESIGNED              |
| Accessibility | NOT CERTIFIED             |

Passing geometric checks is not evidence of construction safety or statutory compliance.

Warning: Master attached bathroom: mechanical exhaust selected; duct route and capacity require design.

Warning: Caregiver attached toilet: mechanical exhaust selected; duct route and capacity require design.

Warning: Upper bathroom: mechanical exhaust selected; duct route and capacity require design.

FLOORFORGE / COST / SCENARIO

|                    |                          |
|--------------------|--------------------------|
| Gross floor area   | 4556.56 ft2              |
| Illustrative range | INR 100.24 - 140.34 lakh |
| Owner budget       | INR 65.0 lakh            |
| Rates              | [2000.0, 2800.0] INR/ft2 |

Illustrative user-editable gross-plan-envelope rates, including open terrace cells. NOT a quote, tender, BOQ or market survey.

Excluded: land, approvals and professional fees, tax treatment, abnormal foundations, lifts, loose furniture, external services

No reinforcement quantities or cement bag counts are invented from floor area.

FLOORFORGE / SITE / SERVICES / STRUCTURE

|                           |                                            |
|---------------------------|--------------------------------------------|
| Soil                      | unknown                                    |
| Foundation recommendation | NOT PROVIDED: requires geotechnical design |
| Solar elevation           | 47.93 degrees                              |
| Vastu score               | 75 / advisory only                         |

A soil name or photograph cannot establish bearing capacity, swelling or an appropriate foundation.

Cluster wet areas; a plumbing designer must size and route stacks, vents and gradients.

No electrical cable sizing, protection coordination or circuit approval.

No medical gas, life-support power or ICU services design.

Preference heuristic from supplied brief, not a safety or scientific rating. Strict requests are flagged, not guaranteed.

Solar method: NOAA-style closed-form solar study; no atmospheric refraction

FLOORFORGE / TIMELINE / ASSUMPTIONS

|                              |                    |
|------------------------------|--------------------|
| Survey, soil and approvals   | Week 0 + 6 weeks   |
| Foundations and substructure | Week 6 + 5 weeks   |
| Frame and roof               | Week 11 + 12 weeks |
| Masonry and services         | Week 19 + 7 weeks  |
| Finishes and joinery         | Week 26 + 8 weeks  |
| Testing and handover         | Week 34 + 2 weeks  |

Illustrative overlapping phases, not a contractual or local construction schedule.

No government review period or supply lead time has been verified.

FLOORFORGE / OPENING SCHEDULE

|     |    |                                                                 |
|-----|----|-----------------------------------------------------------------|
| D1  | x8 | Flush door, hardwood frame / 900 x 2100 / sill 0 mm             |
| D2  | x1 | Flush door, hardwood frame / 1000 x 2100 / sill 0 mm            |
| D3  | x1 | Flush door, water-resistant (WPC) / 800 x 2100 / sill 0 mm      |
| D4  | x1 | Flush door, hardwood frame / 1000 x 2400 / sill 0 mm            |
| D5  | x1 | Main door, solid timber leaf in frame / 1200 x 2400 / sill 0 mm |
| D6  | x2 | Flush door, hardwood frame / 1100 x 2100 / sill 0 mm            |
| D7  | x1 | Flush door, hardwood frame / 900 x 2150 / sill 0 mm             |
| SD1 | x1 | Sliding glazed door, aluminium / 2650 x 2400 / sill 0 mm        |
| SD2 | x1 | Sliding glazed door, aluminium / 3600 x 2400 / sill 0 mm        |
| SD3 | x1 | Sliding glazed door, aluminium / 1100 x 2400 / sill 0 mm        |
| SD4 | x1 | Sliding glazed door, aluminium / 2600 x 2400 / sill 0 mm        |
| SD5 | x2 | Sliding glazed door, aluminium / 1800 x 2400 / sill 0 mm        |
| SD6 | x1 | Sliding glazed door, aluminium / 800 x 2400 / sill 0 mm         |
| O1  | x1 | Cased opening, no leaf / 3300 x 3000 / sill 0 mm                |
| O2  | x1 | Cased opening, no leaf / 850 x 3000 / sill 0 mm                 |
| O3  | x1 | Cased opening, no leaf / 1500 x 3000 / sill 0 mm                |
| O4  | x1 | Cased opening, no leaf / 1425 x 2700 / sill 0 mm                |
| O5  | x1 | Cased opening, no leaf / 3900 x 3000 / sill 0 mm                |
| O6  | x1 | Cased opening, no leaf / 2100 x 3000 / sill 0 mm                |
| O7  | x1 | Cased opening, no leaf / 1950 x 3000 / sill 0 mm                |
| O8  | x1 | Cased opening, no leaf / 1100 x 3000 / sill 0 mm                |
| O9  | x1 | Cased opening, no leaf / 4800 x 3000 / sill 0 mm                |
| W1  | x1 | Sliding window, aluminium / 650 x 1700 / sill 650 mm            |

Nominal wall opening dimensions. Frames, tolerances and clear passage require detailing.

FLOORFORGE / OPENING SCHEDULE

|     |    |                                                                  |
|-----|----|------------------------------------------------------------------|
| W2  | x1 | Sliding window, aluminium / 2400 x 1600 / sill 800 mm            |
| W3  | x1 | Sliding window, aluminium / 3420 x 1700 / sill 600 mm            |
| W4  | x2 | Sliding window, aluminium / 1000 x 2100 / sill 300 mm            |
| W5  | x1 | Sliding window, aluminium / 1400 x 1300 / sill 1000 mm           |
| W6  | x1 | Sliding window, aluminium / 1400 x 1800 / sill 450 mm            |
| W7  | x1 | Sliding window, aluminium / 3000 x 1500 / sill 750 mm            |
| W8  | x1 | Sliding window, aluminium / 1000 x 1500 / sill 750 mm            |
| W9  | x1 | Sliding window, aluminium / 2600 x 1100 / sill 1100 mm           |
| W10 | x2 | Sliding window, aluminium / 1274 x 2500 / sill 350 mm            |
| W11 | x1 | Sliding window, aluminium / 2250 x 2400 / sill 450 mm            |
| W12 | x1 | Sliding window, aluminium / 2700 x 1600 / sill 800 mm            |
| W13 | x1 | Sliding window, aluminium / 2200 x 1500 / sill 750 mm            |
| W14 | x1 | Sliding window, aluminium / 2600 x 1500 / sill 750 mm            |
| W15 | x1 | Sliding window, aluminium / 1400 x 1500 / sill 750 mm            |
| V1  | x1 | Ventilator, obscured glass / louvres / 1100 x 800 / sill 1500 mm |
| V2  | x1 | Ventilator, obscured glass / louvres / 1500 x 450 / sill 2200 mm |

Nominal wall opening dimensions. Frames, tolerances and clear passage require detailing.