

Ground floor



The Verandah House

SPACE	CLEAR AREA	SIZE / m
Dining	7.92 m2	2.93 x 2.77
Living	9.04 m2	3.33 x 2.77
Hall	2.78 m2	1.10 x 2.52
Kitchen	5.95 m2	2.43 x 2.45
Bathroom	3.05 m2	2.43 x 1.25
Utility	2.54 m2	2.43 x 1.05
Bedroom 1	18.55 m2	6.26 x 2.96

DRAWING NOTES

All plan dimensions are millimetres.

Clear areas exclude walls; open zones are named separately.


Nominal door widths are not finished accessible clear widths.

Above-cut windows are dashed. Furniture is schematic at true scale.

No certified IS 962 or local code compliance is claimed.

SCALE 1:75 AT A3 / CUT +1200 mm

Dimensions govern; do not scale from a screen.

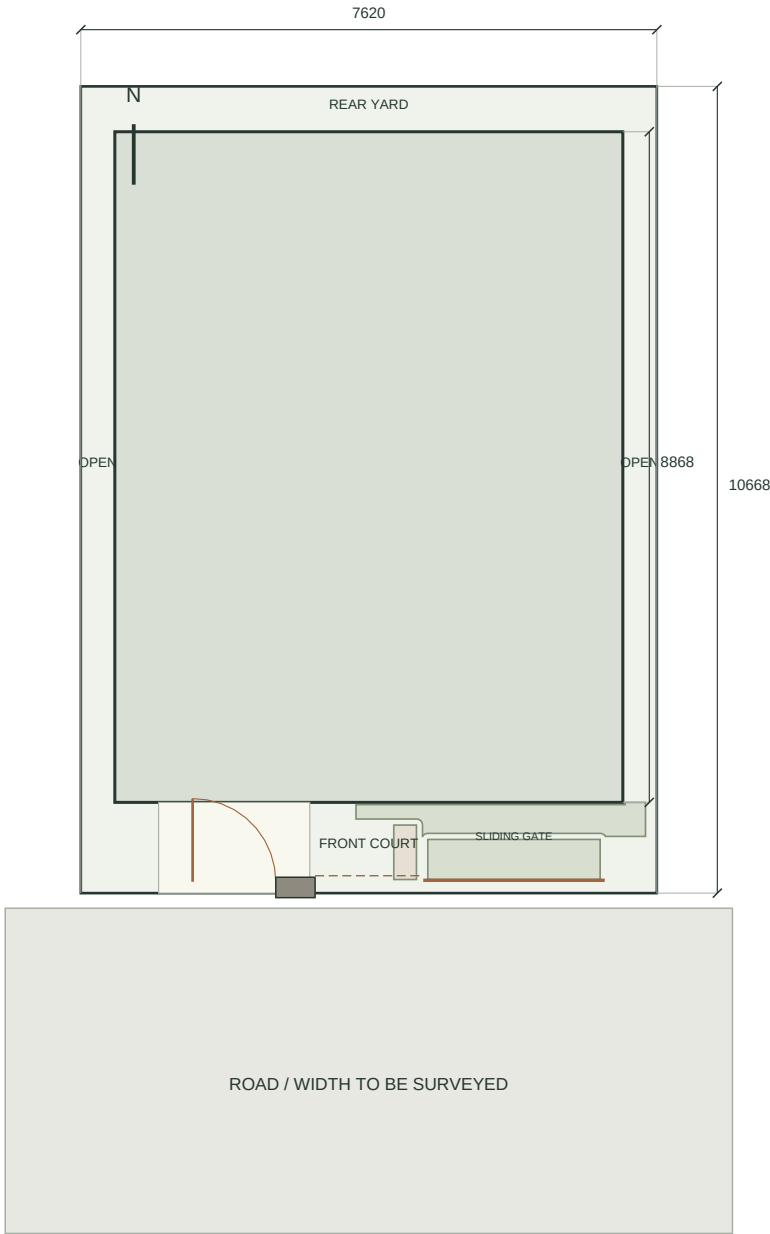

The Verandah House

AREA STATEMENT	VALUE	UNIT
Plot	81.29	m2
Footprint	59.593	m2
Gross floors	59.593	m2
Coverage	73.31	percent
Geometric FAR	0.733	ratio


DRAWING NOTES

- Setbacks are design assumptions, not verified byelaws.
- Road width, property line and levels need a survey.
- No surveyed drainage fall or flood datum supplied.
- Default steps are not a step-free route.

SCALE 1:100 AT A3 / CUT +1200 mm

Dimensions govern; do not scale from a screen.

Front elevation

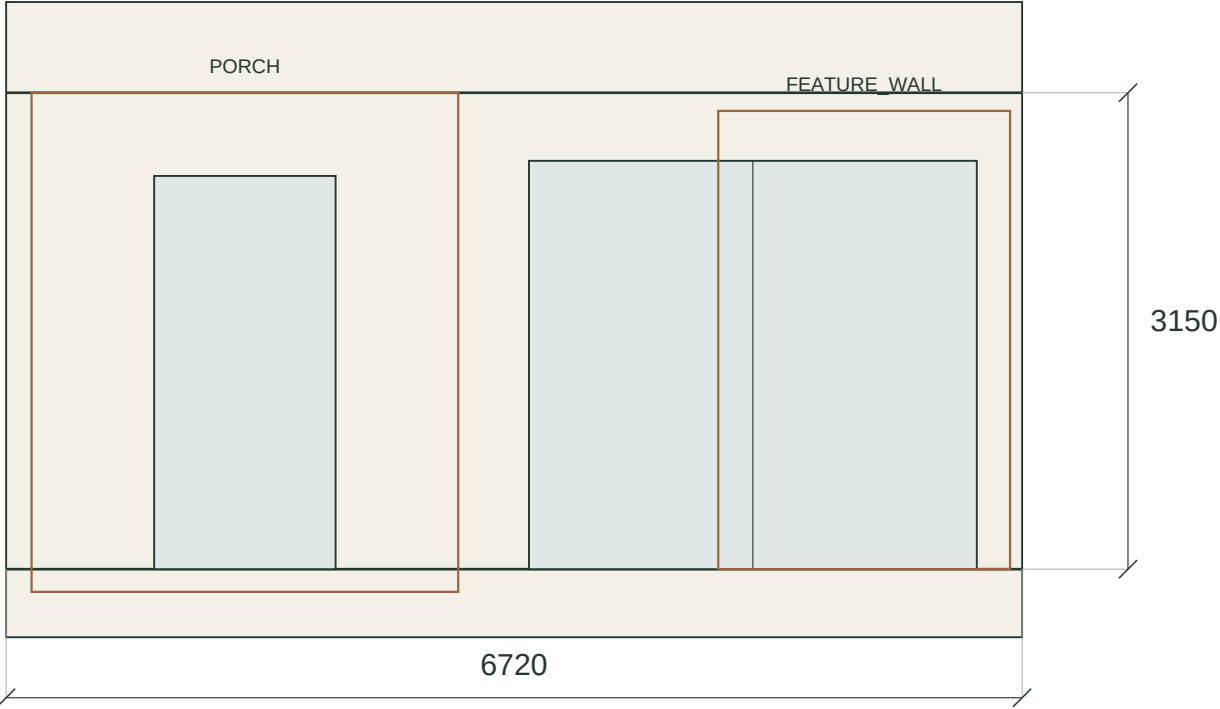

The Verandah House

DRAWING NOTES

Wall and opening heights derive from the building model.

This elevation records the primary wall plane.


Decorative facade accessories are coordinated in 3D, not fully detailed here.

No cladding anchors or construction joints are designed.

SCALE 1:50 AT A3 / CUT +1200 mm

Dimensions govern; do not scale from a screen.

Rear elevation

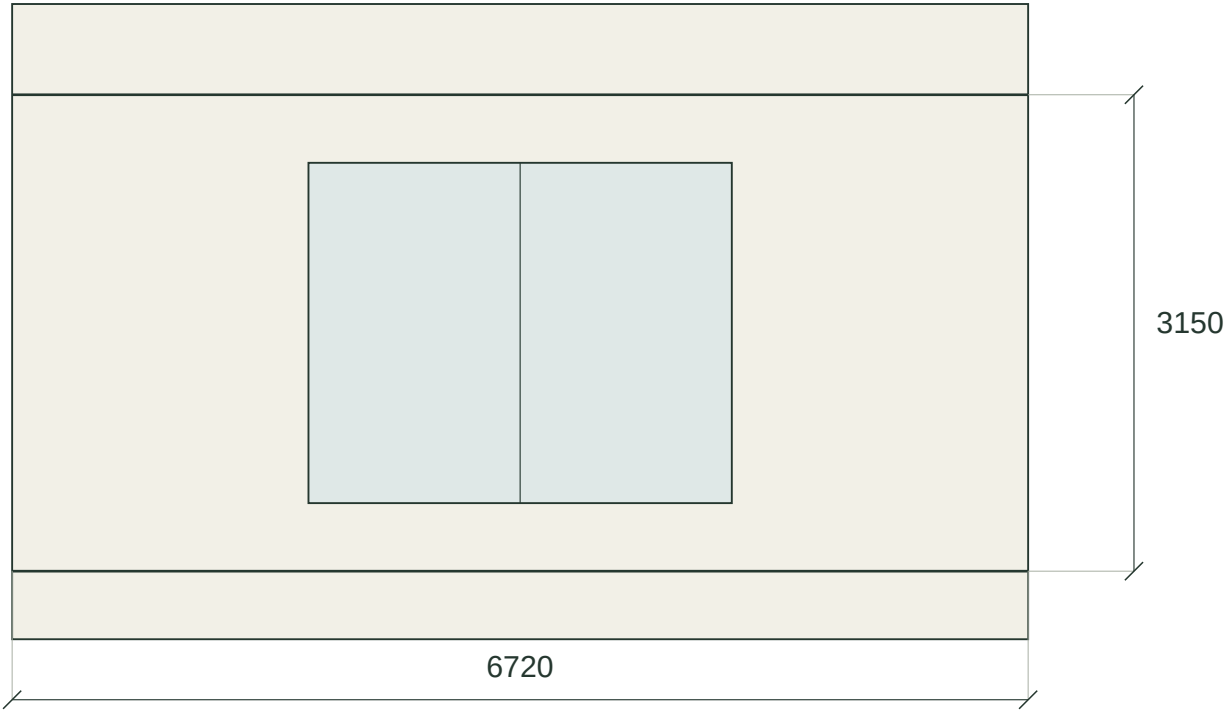

The Verandah House

DRAWING NOTES


- Wall and opening heights derive from the building model.
- This elevation records the primary wall plane.
- Decorative facade accessories are coordinated in 3D, not fully detailed here.
- No cladding anchors or construction joints are designed.

SCALE 1:50 AT A3 / CUT +1200 mm

Dimensions govern; do not scale from a screen.



Left elevation

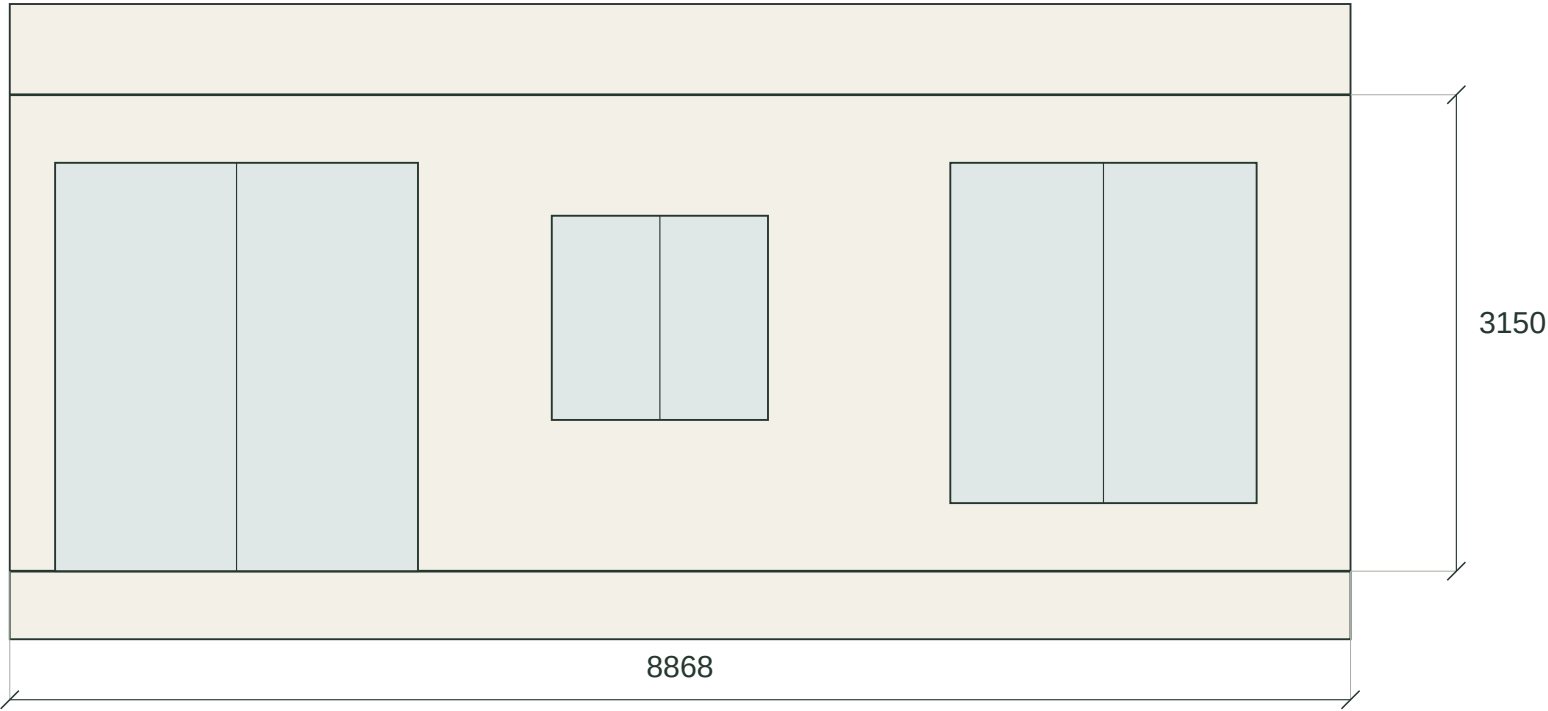

The Verandah House

DRAWING NOTES

Wall and opening heights derive from the building model.

This elevation records the primary wall plane.

Decorative facade accessories are coordinated in 3D, not fully detailed here.


No cladding anchors or construction joints are designed.

SCALE 1:50 AT A3 / CUT +1200 mm

Dimensions govern; do not scale from a screen.



Right elevation

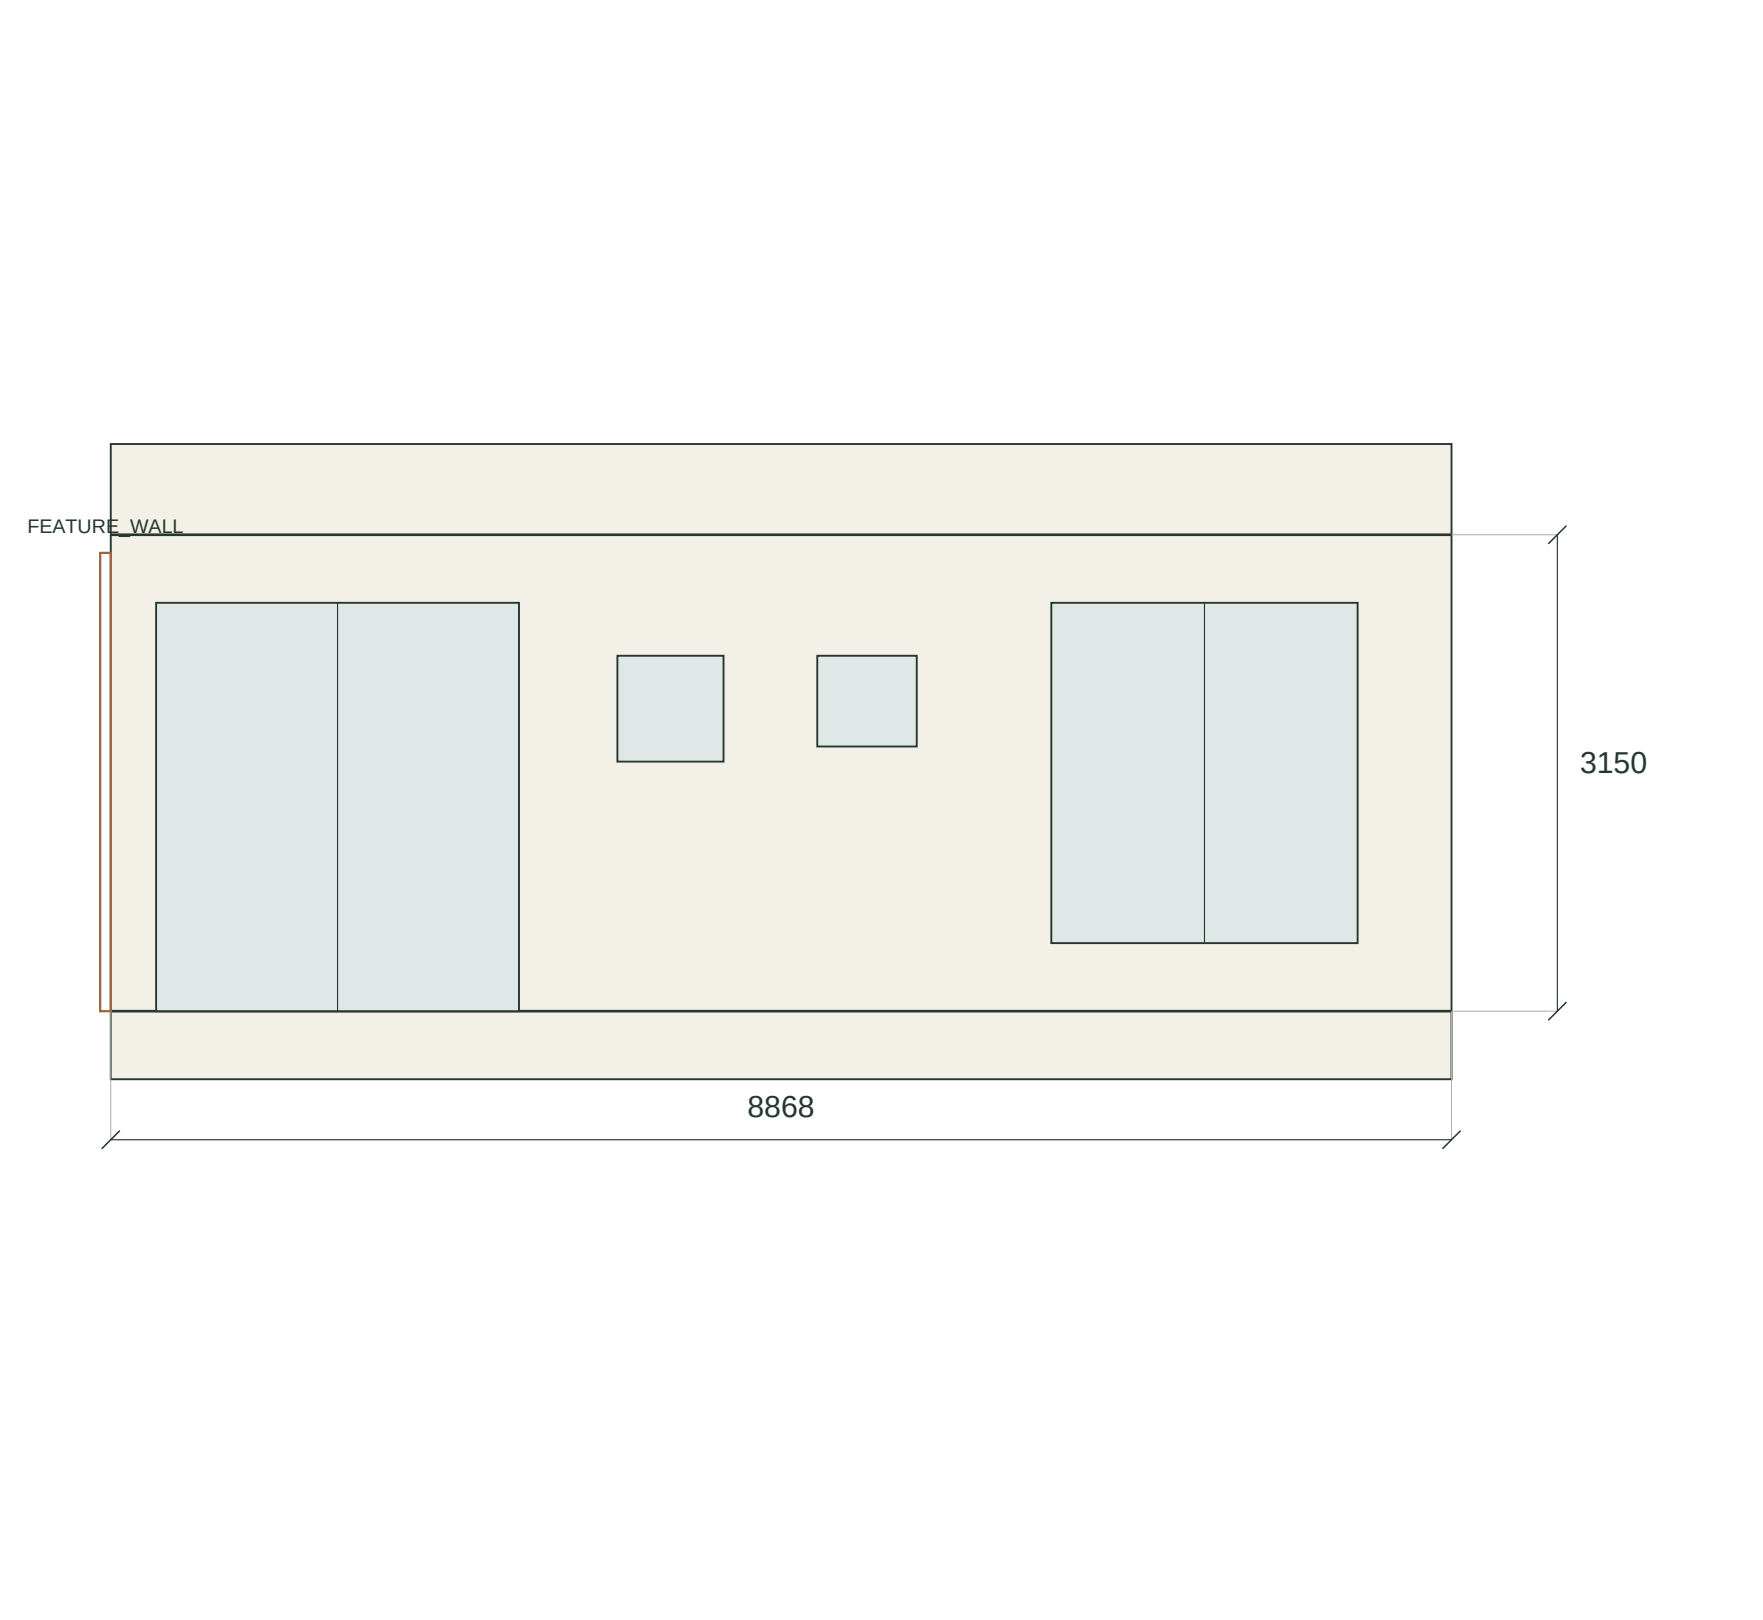

The Verandah House

DRAWING NOTES

Wall and opening heights derive from the building model.

This elevation records the primary wall plane.


Decorative facade accessories are coordinated in 3D, not fully detailed here.

No cladding anchors or construction joints are designed.

SCALE 1:50 AT A3 / CUT +1200 mm

Dimensions govern; do not scale from a screen.

Section A-A / x = 3.36 m

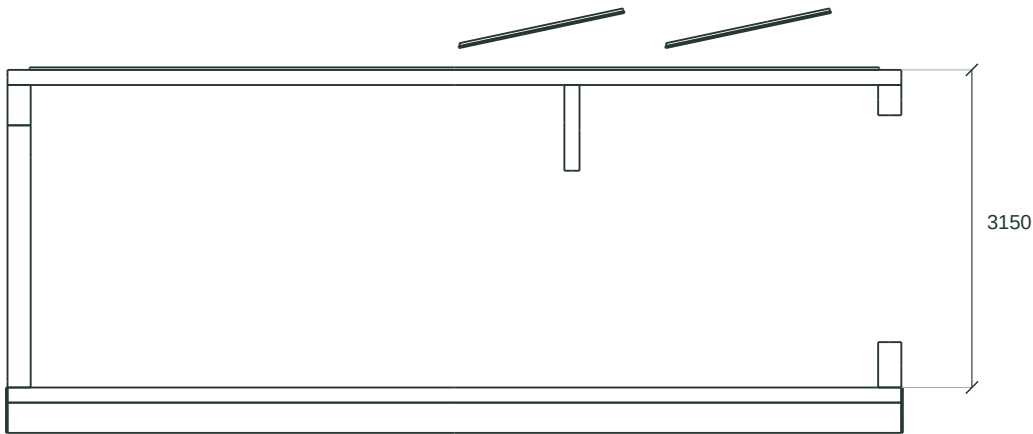

The Verandah House

DRAWING NOTES

Actual mesh-plane intersections, not a generic stair illustration.

Cut objects: walls, floor slabs, roof, stair and plinth.


No reinforcement or foundation design is represented.

Stair headroom and handrails require a separate professional check.

SCALE 1:75 AT A3 / CUT +1200 mm

Dimensions govern; do not scale from a screen.



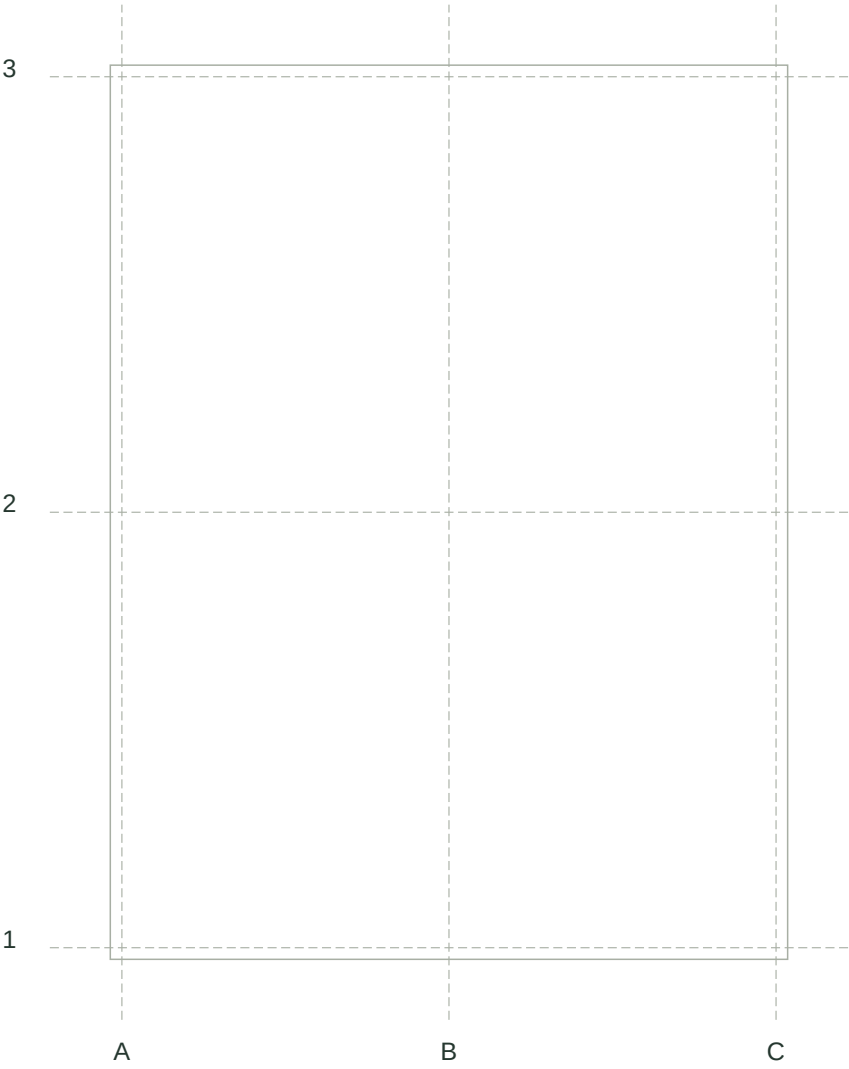

The Verandah House

DRAWING NOTES

Axes shown for coordination only; they are NOT column locations.

No column, beam, slab or footing is sized or certified.

Engineer must establish an actual load path and lateral system.

No soil-bearing capacity is inferred from a soil photograph.

SCALE 1:75 AT A3 / CUT +1200 mm

Dimensions govern; do not scale from a screen.

FLOORFORGE / REVIEW / SCOPE

Geometry	preliminary_geometry_pass
Regulatory	NOT EVALUATED
Structure	NOT DESIGNED
Accessibility	NOT CERTIFIED

Passing geometric checks is not evidence of construction safety or statutory compliance.

FLOORFORGE / COST / SCENARIO

Gross floor area	641.45 ft2
Illustrative range	INR 14.11 - 19.76 lakh
Owner budget	INR 18 lakh
Rates	[2000.0, 2800.0] INR/ft2

Illustrative user-editable gross-plan-envelope rates, including open terrace cells. NOT a quote, tender, BOQ or market survey.

Excluded: land, approvals and professional fees, tax treatment, abnormal foundations, lifts, loose furniture, external services

No reinforcement quantities or cement bag counts are invented from floor area.

FLOORFORGE / SITE / SERVICES / STRUCTURE

Soil	unknown
Foundation recommendation	NOT PROVIDED: requires geotechnical design
Solar elevation	47.93 degrees
Vastu score	0 / advisory only

A soil name or photograph cannot establish bearing capacity, swelling or an appropriate foundation.

Cluster wet areas; a plumbing designer must size and route stacks, vents and gradients.

No electrical cable sizing, protection coordination or circuit approval.

No medical gas, life-support power or ICU services design.

Preference heuristic from supplied brief, not a safety or scientific rating. Strict requests are flagged, not guaranteed.

Solar method: NOAA-style closed-form solar study; no atmospheric refraction

FLOORFORGE / TIMELINE / ASSUMPTIONS

Survey, soil and approvals	Week 0 + 6 weeks
Foundations and substructure	Week 6 + 5 weeks
Frame and roof	Week 11 + 6 weeks
Masonry and services	Week 15 + 7 weeks
Finishes and joinery	Week 22 + 8 weeks
Testing and handover	Week 30 + 2 weeks

Illustrative overlapping phases, not a contractual or local construction schedule.

No government review period or supply lead time has been verified.

FLOORFORGE / OPENING SCHEDULE

F0-N001	window / 2400 x 2700 / sill 0 mm
F0-D002	entry / 1200 x 2600 / sill 0 mm
F0-N003	window / 1430 x 1350 / sill 1000 mm
F0-D004	cased / 1500 x 2150 / sill 0 mm
F0-N005	window / 2026 x 2250 / sill 450 mm
F0-N006	window / 2800 x 2250 / sill 450 mm
F0-D007	door / 950 x 2150 / sill 0 mm
F0-N008	window / 2962 x 2700 / sill 0 mm
F0-D009	door / 850 x 2150 / sill 0 mm
F0-D010	door / 850 x 2150 / sill 0 mm
F0-N011	window / 2400 x 2700 / sill 0 mm
F0-N012	window / 702 x 700 / sill 1650 mm
F0-N013	window / 658 x 600 / sill 1750 mm
F0-N014	window / 2026 x 2250 / sill 450 mm

Nominal wall opening dimensions. Frames, tolerances and clear passage require detailing.